


PROPOSED SHED REFURBISHMENT
48 SIPPY CREEK RD, TANAWHA QLD 4556
SUNSHINE COAST REGIONAL COUNCIL




REAL PROPERTY DESCRIPTION
LOT 427
SP237585

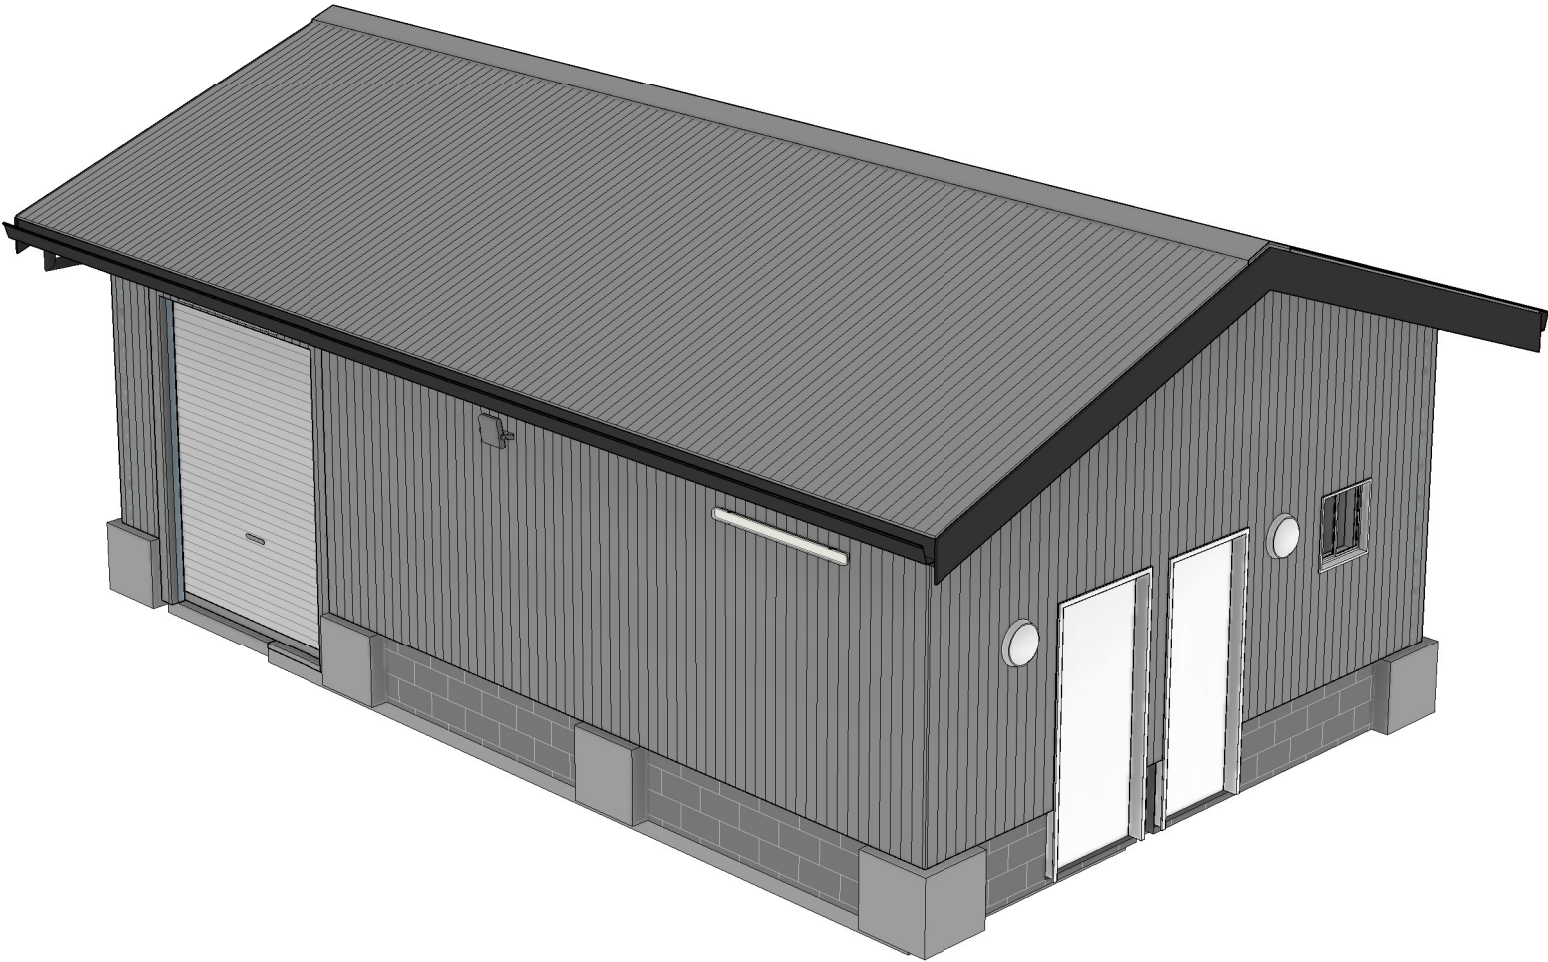

COVERSHEET PERSPECTIVE
SCALE : N.T.S



AERIAL LOCALITY PLAN
SCALE : N.T.S

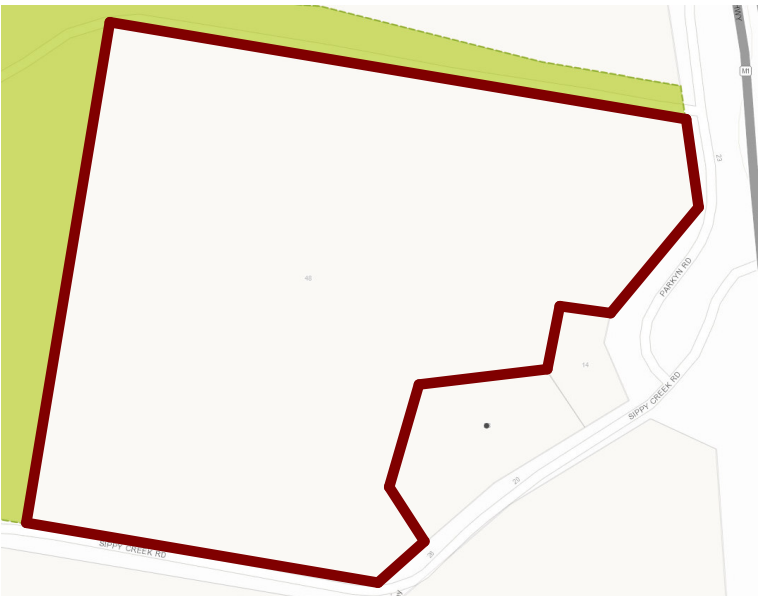

UNITY WATER MAPPING
SCALE : N.T.S

DRAWING REGISTER		
No.	DESCRIPTION	REV.
DESIGN DRAWINGS		
100	COVERSHEET	B
110	STRUCTURAL NOTES	B
200	SITE PLAN	B
201	EXISTING STRUCTURE PHOTOS	B
210	DEMOLITION PLAN	B
300	FLOOR PLANS	B

DRAWING REGISTER		
No.	DESCRIPTION	REV.
301	REFLECTIVE CEILING & ROOF PLANS	B
302	STRUCTURAL FRAMING PLANS	B
310	EXTERNAL ELEVATIONS	B
311	INTERNAL ELEVATIONS	B
312	SECTIONS	B
330	DETAILED SECTIONS - SHEET 1	B
331	DETAILED SECTIONS - SHEET 2	B



CONTOUR

SUNSHINE COAST OFFICE
Building A, Level 1,
6 Innovation Parkway,
Birtinya, 4575, Qld
Ph. (07) 5493 9777
Website: www.ContourCE.com.au

NORTH LAKES OFFICE
Corporate Suite A, Bld 2
2 - 4 Flinders Parade,
North Lakes, 4509, Qld
Ph. (07) 5493 9777
Email: admin@contource.com.au

ABN 62 117 061 659



PLAN DETAILS:

Designed: JT
Drawn: JT
Checked: PB
Datum: 20/12/2021
Date: 11:42:20 AM

PLAN AMENDMENTS:

Rev	Date	Comment	Altered	Checked
B	20.12.2021	FOR TENDER	JT	PB

PROPOSED SHED REFURBISHMENT
48 SIPPY CREEK RD, TANAWHA
SUNSHINE COAST REGIONAL COUNCIL

This plan is Copyright. Other than for the purposes of and subject to the conditions prescribed under the Copyright Act, no part of it may in any form or by any means be reproduced, stored in a retrieval system or transmitted without the prior written permission of Contour Consulting Engineers. The plan shall not be used for construction without prior written approval.

PLAN TITLE:

COVERSHEET

PLAN No: 1417 03 100

FOR TENDER

REVISION: B

GENERAL NOTES:

1. These drawings shall be read in conjunction with all other consultants drawings and specifications.

2. Before proceeding with the works any discrepancies in the engineering drawings shall be referred for decision to the Engineer.

3. Setting out dimensions and sizes of members or elements shall not be obtained by scaling the drawings.

4. All dimensions shown on the engineering drawings shall be checked by the contractor before commencement of fabrication or site works.

5. During construction, the structure shall be maintained in a stable condition. Construction loads must not exceed the safe load capacity of the structure at any time during construction. If in doubt ask the Engineer.

6. All workmanship and materials shall be in accordance the requirements of the current editions including Amendments of the relevant SAA Codes of Practice, except as varied by the Contract Documents and of the By-Laws of the Local Government Authority.

7. Wind loads for this project have been determined in accordance with AS1170.2

Site specific design wind speed factors adopted for this project are as follows:

Importance Level

Region

Basic Regional Wind Speeds

Direction multiplier

Terrain / Height multiplier

Shielding multiplier

Topographic multiplier

Internal pressure coefficient

Limit State Design Wind Speed

= 2

= B

V500 (u) = 57m/s (ultimate)

V100 (p) = 48m/s (permissible)

V25 (s) = 43m/s (service)

Md = 0.95

Mz.cat = 0.87

Ms = 1.00

Mt = 1.00

Cpi = +0.2, -0.3

Vdes = 47.1m/s (N3)

8. Permanent, imposed and other loads (Dead & Live) for this project have been determined in accordance with AS1170.1 - 2002 for the following loadings:

DEAD LOADS

Floors, self weight plus 0.5kPa distributed, gen 1.0Kpa to tiled areas

Roofs, self weight only.

LIVE LOADS

Internal Floors, 5.0kPa distributed, 1.8kN concentrated.

Roofs, 0.25kPa distributed, 1.4kN (Maintenance load only).

SOIL LOADS

Soil Density

Pressure Coefficients

EARTHQUAKE

Importance Level

Annual probability of exceedance

Probability factor

Hazard factor

Site soil class

Structural building height

Earthquake design category

= 1900kg/cu.m

Ka = 0.33, Kp = 3.0, Ko = 0.5

= 2

P = 1/500

Kp = 1.0

Z = 0.05

= Ce

Hn = <12m

= I

STRUCTURAL STEEL WORK NOTES:

1. All steel works is to be carried out in accordance with the current edition of:

AS4100 - SAA steel structures code - AS1554

SAA code for welding in buildings

SA MA 1.8 - Fabrication

SA MA 1.9 - Erection

AISC - Standardized Structural Connection.

2. One full size paper copy of the shop detail drawings are to be submitted to the Engineer and approval of same obtained before commencing fabrication. Approval will not cover dimensional setout.

3. Unless noted otherwise, the size of all fillet welds is to be 6mm, SP category in accordance with AS1554.

Welding electrode grade to be E48XX unless noted otherwise.

4. All bolts to be grade 8.8 high strength structural bolts to AS1252, snug tightened unless notes otherwise.

5. Internal steel work is to be thoroughly cleaned and coated with one coat of red oxide zinc chromate paint (or treated as specified) before erection.

6. Exposed steelwork, bolts, nut and washers to be hot dip galvanized. (HDG600 to AS/NZS 2312:2002

7. Where encased, steel work is to be wrapped in 10 gauge (3.25mm) black wire at 100mm pitch with 50mm cover.

8. The steel fabricator shall provide all bolts necessary for erection of the steel work and bolt holes and cleats necessary for the work as shown, noted or implied on these drawings or the architects drawings and specification.

9. The roof structure has been designed for normal roof loads only and does not allow for any extraneous loads such as hoists, monorails etc. except where shown on drawings.

10. When shop splices are necessary in beams or trusses, the position and details of the splice is to be approved by the Engineer.

STRUCTURAL HOLD-POINTS

ELEMENT/INSPECTION	ACTION REQUIRED BY	TIMING
EXISTING FRAMING INSPECTION	STRUCTURAL ENGINEER TO VISUALLY INSPECT STRUCUTRAL ELEMENTS FOR ADEQUACY.	DIRECTLY AFTER DEMOLITION PHASE IS COMPLETE
STRUCTURAL STEEL FRAMING/ BRACING	STRUCTURAL ENGINEER TO VISUALLY INSPECT ONSITE	PRIOR TO INSTALLATION OF LININGS/CLADDING

NOTE

- REFER NOTES FOR REQUIRED CONCRETE SAMPLES TO BE TESTED PER POUR, ALL TEST RESULTS TO BE SENT TO THE STRUCTURAL ENGINEER FOR REVIEW AND APPROVAL
- PROVIDE MINIMUM 48HOURS NOTICE FOR ALL ONSITE INSPECTIONS

TIMBER NOTES:

1. All timber design and construction shall be in accordance with AS1720 & AS1684 U.N.O.

2. All softwood shall be minimum stress grade F5 or MGP10 U.N.O.

3. All hardwood shall be minimum stress grade F14 U.N.O.

4. All laminated timber to be to G.L.T.A. specifications U.N.O.

5. External timber shall be either hardwood - Durability Class I or II, or impregnated grade F7 pine, pressure treated to AS1604 and re-dried prior to use. Supplementary treatment shall be applied to all cut surfaces. Details of preservative treatment shall be provided to the Engineer.

6. All bolts in timber construction shall be minimum M12 U.N.O and bolts, nuts and washers shall be hot dip galvanised. Bolt holes drilled in timber shall be exact size for bolts and spaced as documented. Where no specified bolts spacing's to be in accordance with AS1720 & As1684. Washers under bolt head and nuts shall be at least 2.5 times bolt diameter.

7. Bolting Schedule:

edge distances

M10 - 50mm

M12 - 60mm

M16 - 80mm

M20 -100mm

spacing

M10 - 50mm

M12 - 60mm

M16 70mm

M20 - 80mm

All bolts to timber work to be grade 4.6/s u.n.o. (not applicable to masonry anchors & cast-in bolts)

Bolts, nuts & washers to be hot dip galvanised.

Bolt holes in steel plates shall provide a snug fit not greater than 0.5mm larger than bolt diameter.

Washers to timber:

M12 bolts.....50sq x 3 thick

M16 bolts.....65sq x 5 thick

M20 bolts.....75sq x 5 thick

M24 bolts.....85sq x 6 thick (refer to detail drawings)

8. At the end of the defects liability period, all bolted connections throughout entire project must be re-tightened.

9. Timber dimensions on the finish width and thickness of timber to be:

a. Seasoned Softwood

b. Unseasoned Softwood

c. Seasoned Hardwood

d. Unseasoned Hardwood

+5.0, -0 mm

+3.0, -3 mm

+2.0, -0 mm

+3.0, -3 mm

10. All timber joints and notches shall be 100mm minimum away from loose knots, severe sloping grain gum veins or other minor defects.

11. All details not shown on the engineering drawings shall be in accordance with AS1684 - 1996 Residential Timber Framing Code and best practices.

12. Roof Trusses Timber trusses shall be supplied pre-cambered by an amount equal to the applied dead load deflection. A design certificate is to be provided prior to truss manufacture and signed by Truss Engineer (RPEQ). Once the trusses are installed the truss engineer shall provide a certificate indicating that the trusses have been installed as required. The certificate should also indicate and cover all bracing and tie-down req'd.



CONTOUR

SUNSHINE COAST OFFICE
Building A, Level 1,
6 Innovation Parkway,
Birtinya, 4575, Qld
Ph. (07) 5493 9777
Website: www.ContourCE.com.au

NORTH LAKES OFFICE
Corporate Suite A, Bld 2
2 - 4 Flinders Parade,
North Lakes, 4509, Qld
Ph. (07) 5493 9777
Email: admin@contource.com.au



PLAN DETAILS:

Designed: JT
Drawn: JT
Checked: PB
Datum:
Date: 20/12/2021 11:42:21 AM

PLAN AMENDMENTS:

Rev	Date	Comment	Altered	Checked
B	20.12.2021	FOR TENDER	JT	PB

PROPOSED SHED REFURBISHMENT
48 SIPPY CREEK RD, TANAWHA
SUNSHINE COAST REGIONAL COUNCIL

© This plan is Copyright. Other than for the purposes of andsubject to the conditons prescribed under the Copyright Act, no part of it may in any form or by any means be reproduced, stored in a retrieval system or transmitted without the prior written permission of Contour Consulting Engineers. The plan shall not be used for construction without prior written approval.


PLAN TITLE:

STRUCTURAL NOTES


FOR TENDER

PLAN No: 1417 03 110

REVISION: B

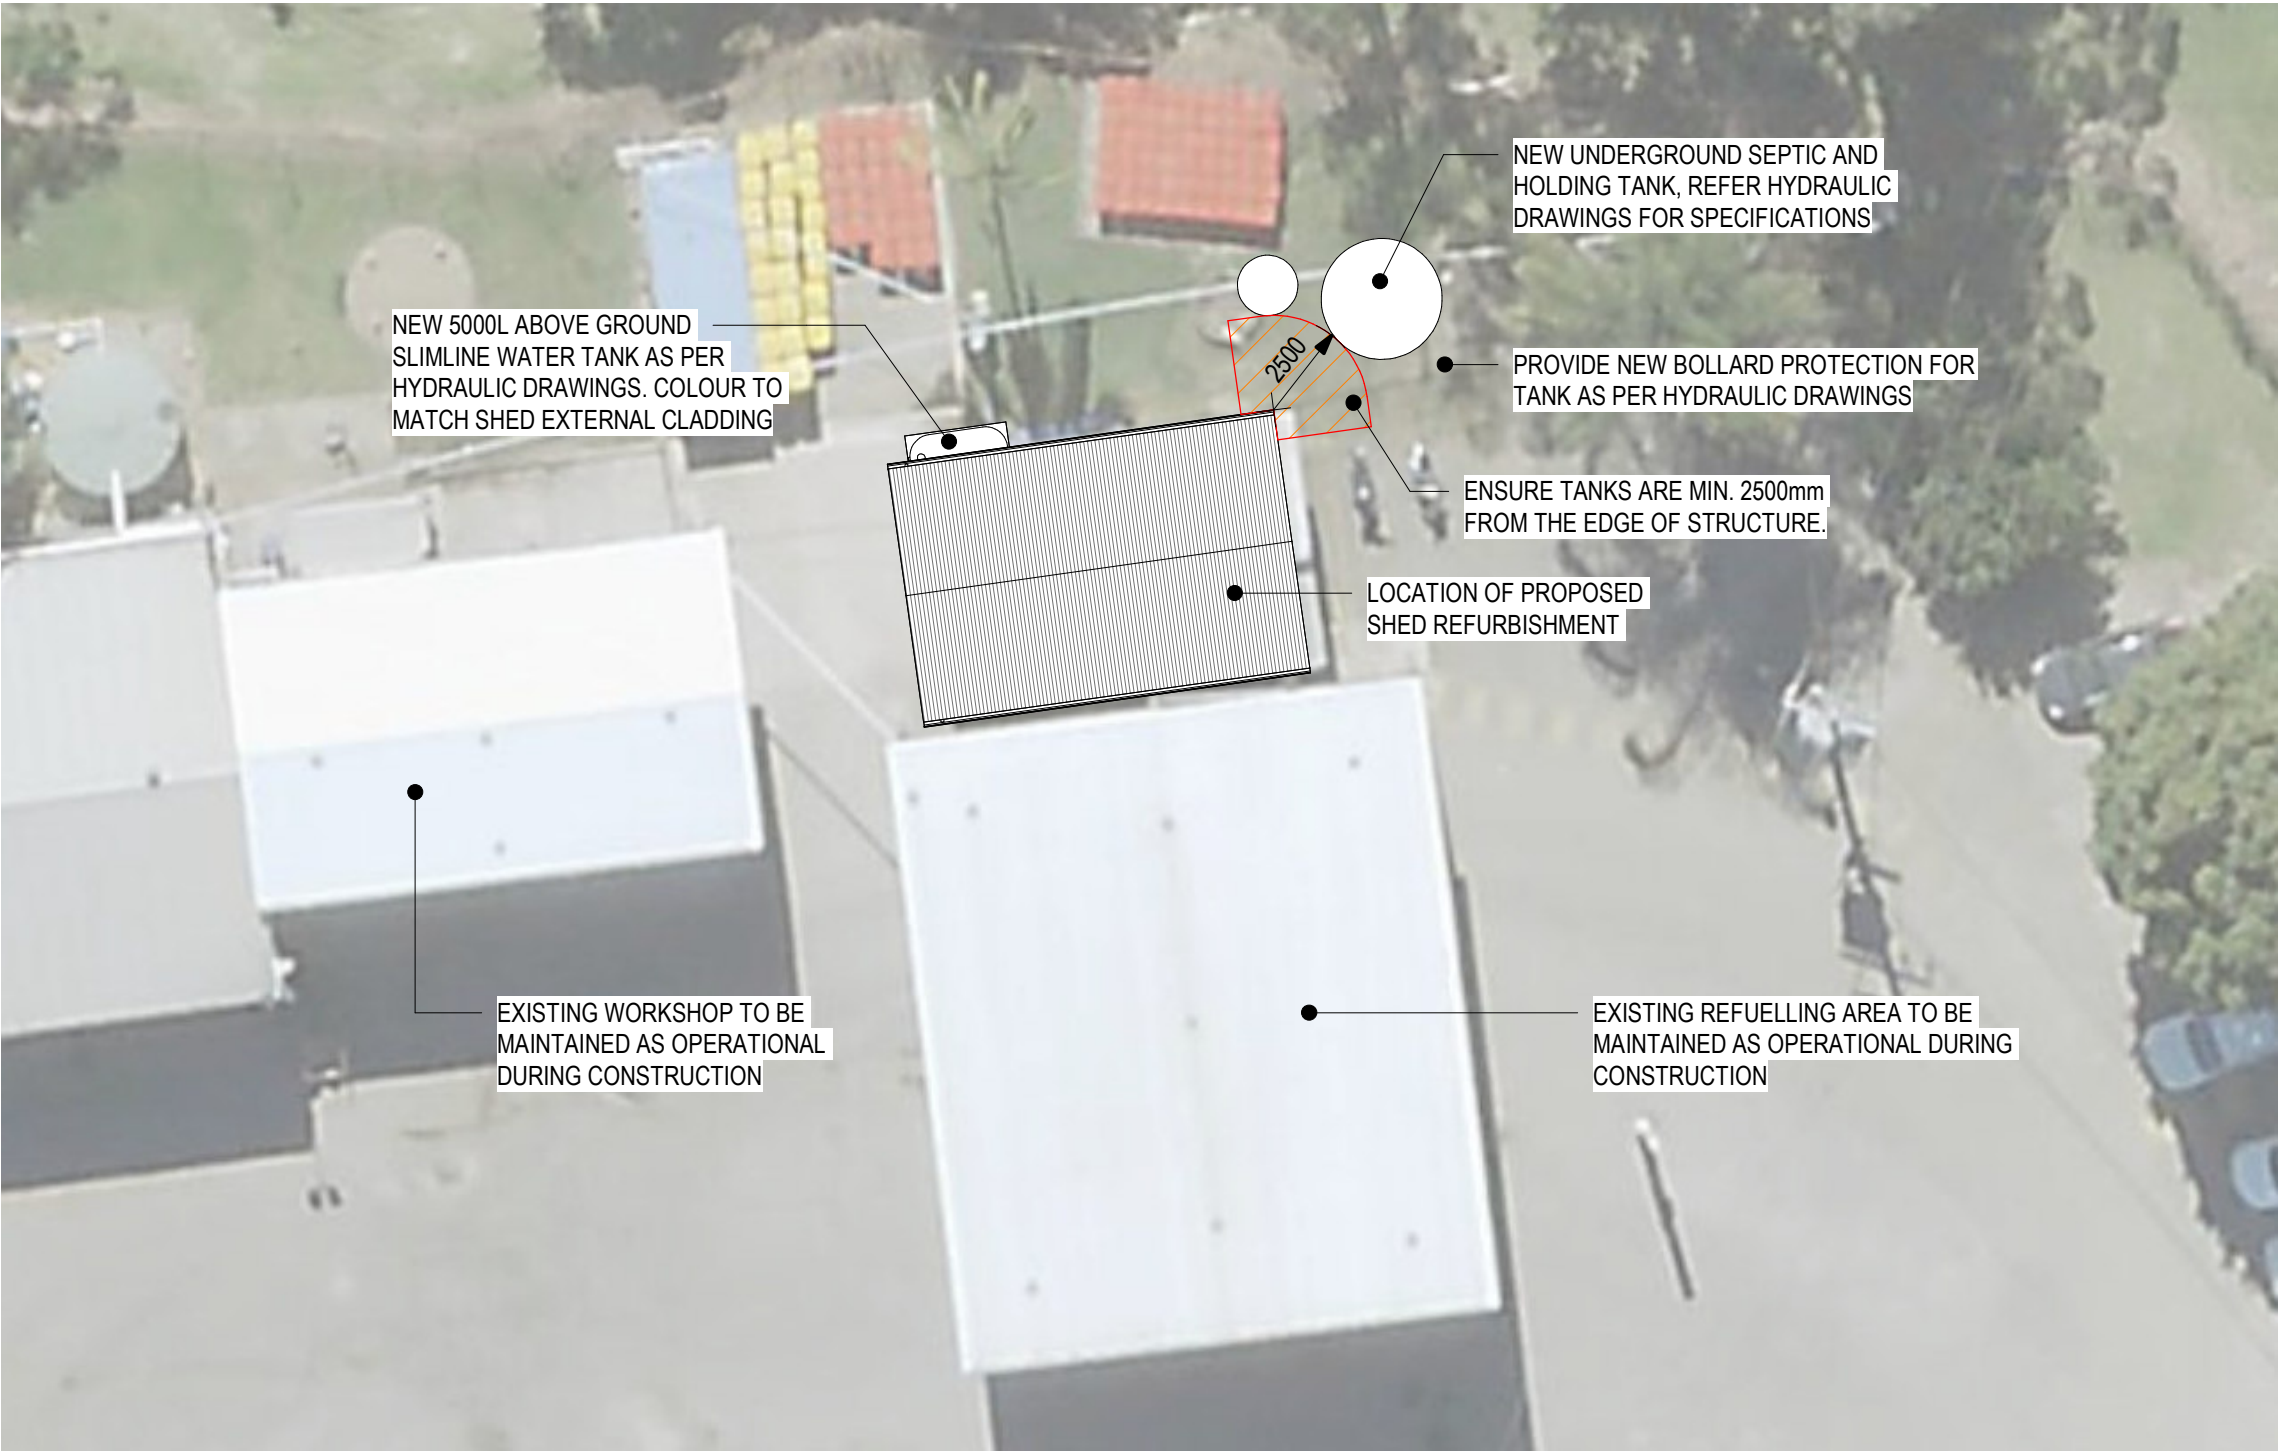

SITE PLAN
SCALE : 1 : 200

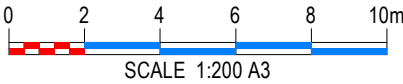



CONTOUR

SUNSHINE COAST OFFICE
Building A, Level 1,
6 Innovation Parkway,
Birtinya, 4575, Qld
Ph. (07) 5493 9777
Website: www.ContourCE.com.au

NORTH LAKES OFFICE
Corporate Suite A, Bld 2
2 - 4 Flinders Parade,
North Lakes, 4509, Qld
Ph. (07) 5493 9777
Email: admin@contource.com.au

A.B.N 62 117 061 659



PLAN DETAILS:

Designed: **JT**
Drawn: **JT**
Checked: **PB**
Datum: **20/12/2021**
Date: **11:42:21 AM**

PLAN AMENDMENTS:

Rev	Date	Comment	Altered	Checked
B	20.12.2021	FOR TENDER	JT	PB

PROPOSED SHED REFURBISHMENT
48 SIPPY CREEK RD, TANAWHA
SUNSHINE COAST REGIONAL COUNCIL

© This plan is Copyright. Other than for the purposes of and subject to the conditions prescribed under the Copyright Act, no part of it may in any form or by any means be reproduced, stored in a retrieval system or transmitted without the prior written permission of Contour Consulting Engineers. The plan shall not be used for construction without prior written approval.

PLAN TITLE:

SITE PLAN

PLAN No: **1417 03 200**

FOR TENDER

REVISION: **B**



**SOUTHERN BUILDING ELEVATION
(EXISTING PHOTO)**



**WESTERN BUILDING ELEVATION
(EXISTING PHOTO)**



**NORTHERN BUILDING ELEVATION
(EXISTING PHOTO)**



**EAST BUILDING ELEVATION
(EXISTING PHOTO)**

PLAN DETAILS:

Designed: JT
Drawn: JT
Checked: PB
Datum: 20/12/2021
Date: 11:42:21 AM

PLAN AMENDMENTS:

Rev	Date	Comment	Altered	Checked
B	20.12.2021	FOR TENDER	JT	PB

**PROPOSED SHED REFURBISHMENT
48 SIPPY CREEK RD, TANAWHA
SUNSHINE COAST REGIONAL COUNCIL**

This plan is Copyright. Other than for the purposes of and subject to the conditions prescribed under the Copyright Act, no part of it may in any form or by any means be reproduced, stored in a retrieval system or transmitted without the prior written permission of Contour Consulting Engineers. The plan shall not be used for construction without prior written approval.


PLAN TITLE:

EXISTING STRUCTURE PHOTOS

PLAN No: **1417 03 201**



FOR TENDER

REVISION: **B**

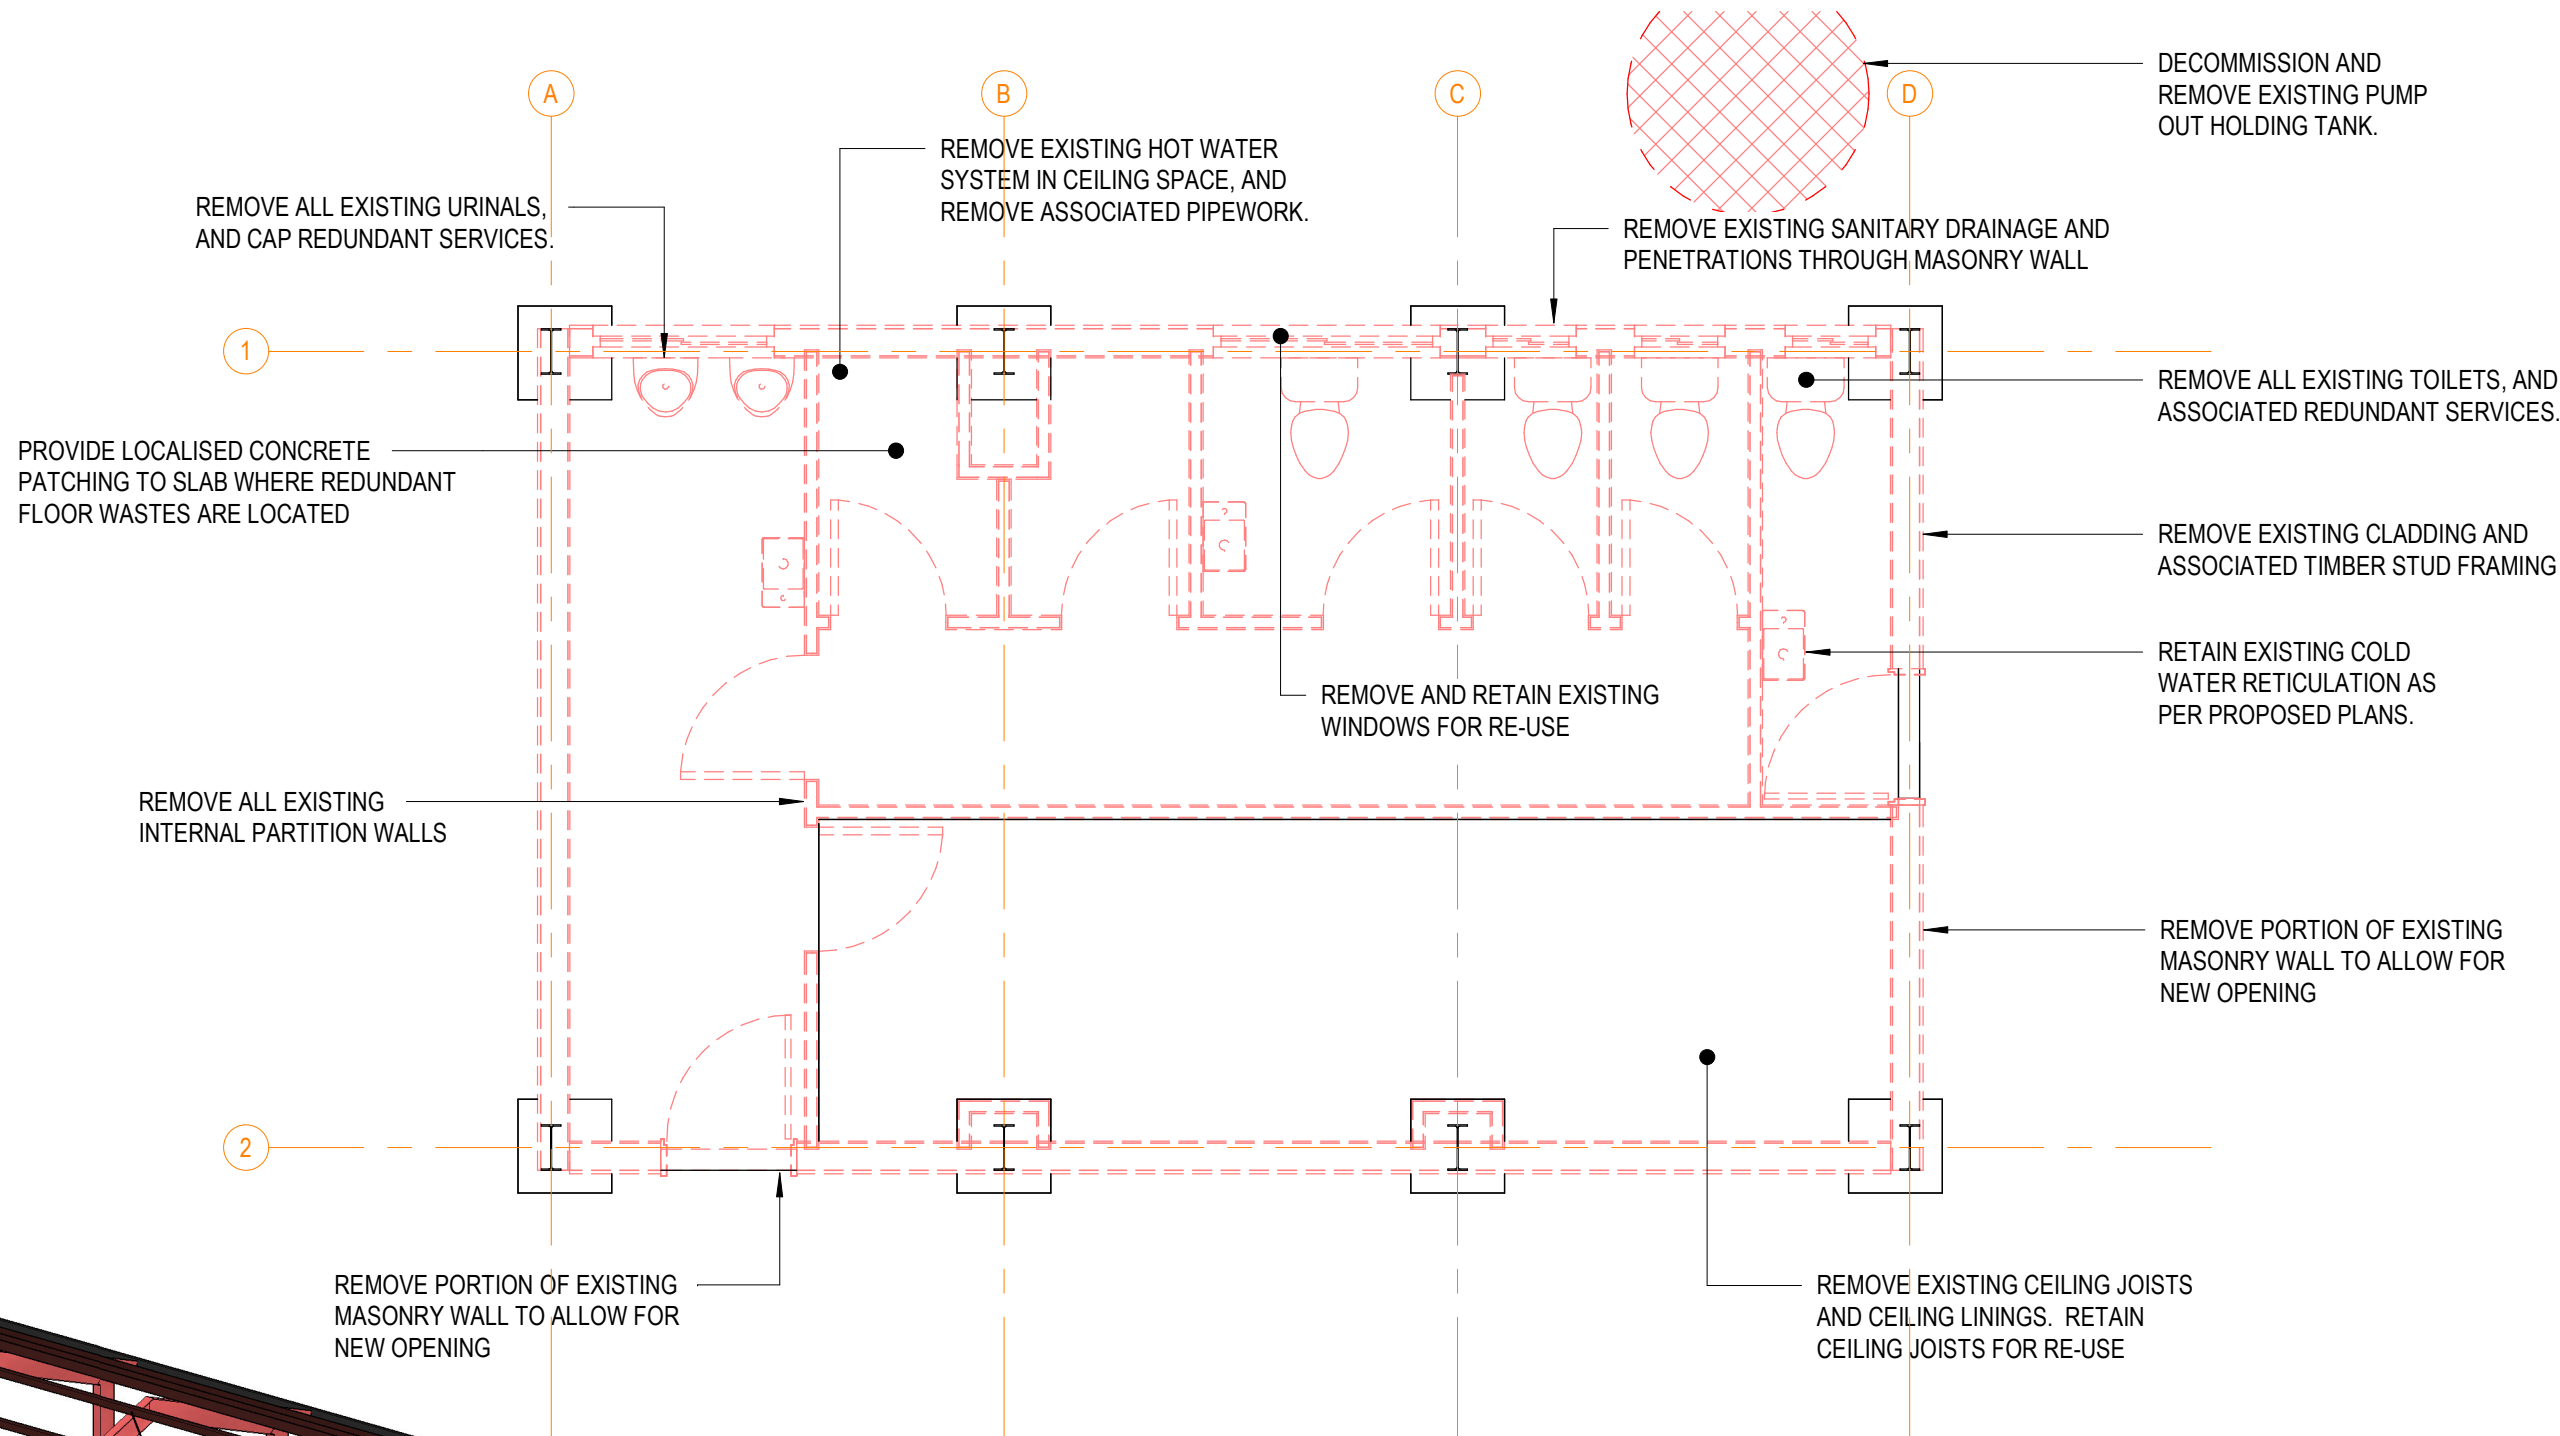

DEMOLITION PLAN
SCALE : 1 : 50

CONTRACTOR TO TREAT ALL EXISTING STEEL MEMBERS & CONNECTIONS WITH A WIRE BRUSH, APPROVED RUST CONVERTER AND AN APPROVED PROTECTIVE COATING SYSTEM . REPLACE DETERIORATED BOLTS/NUTS AS REQUIRED

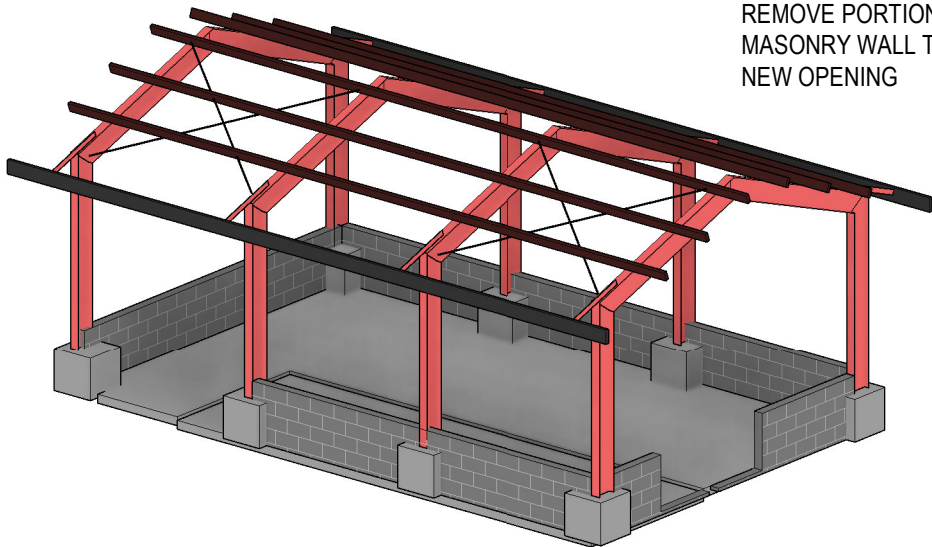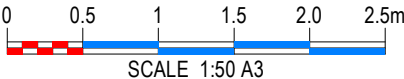

POST-DEMOLITION 3D PERSPECTIVE
SCALE : N.T.S



CONTOUR

SUNSHINE COAST OFFICE
Building A, Level 1,
6 Innovation Parkway,
Birtinya, 4575, Qld
Ph. (07) 5493 9777
Website: www.ContourQE.com.au

NORTH LAKES OFFICE
Corporate Suite A, Bld 2
2 - 4 Flinders Parade,
North Lakes, 4509, Qld
Ph. (07) 5493 9777
Email: admin@contour.com.au

ABN 62 117 061 659



PLAN DETAILS:

Designed: JT
Drawn: JT
Checked: PB
Datum: 20/12/2021
Date: 11:42:22 AM

PLAN AMENDMENTS:

Rev	Date	Comment	Altered	Checked
B	20.12.2021	FOR TENDER	JT	PB

PROPOSED SHED REFURBISHMENT
48 SIPPY CREEK RD, TANAWHA
SUNSHINE COAST REGIONAL COUNCIL

© This plan is Copyright. Other than for the purposes of and subject to the conditions prescribed under the Copyright Act, no part of it may in any form or by any means be reproduced, stored in a retrieval system or transmitted without the prior written permission of Contour Consulting Engineers. The plan shall not be used for construction without prior written approval.

PLAN TITLE:

DEMOLITION PLAN

PLAN No: **1417 03 210**

FOR TENDER

REVISION: **B**



NEW 5000L ABOVE GROUND SLIMLINE
WATER TANK AS PER HYDRAULIC
DRAWINGS. COLOUR TO MATCH SHED
EXTERNAL CLADDING

PROVIDE KINGSPAN AIRCELL
INSULATION TO ALL EXTERNAL
WALLS AND ROOF

NEW EXTERNAL COLORBOND
CLADDING FIXED TO BATTENS
AND STEEL STUD FRAMING.

TYPICALLY PROVIDE GROUTED CONCRETE
DOOR THRESHOLD RAMPS COMPLIANT TO
AS1428 TO ALL NEW SWING DOORS AND
ROLLER DOORS

PROVIDE APPROX 50mm CONCRETE
TOPPING SLAB TO EXISTING SET
DOWN TO MATCH FINISHED FLOOR
LEVEL

PROVIDE PROTECTIVE FLOOR
COATING TO THE DOCUMENT
STORAGE AREA

PROVIDE NEW FLOOR AND
SKIRTING TILES TO TOILET

RE-USE EXISTING WINDOWS
WHERE POSSIBLE

PROVIDE NEW INTERNAL STEEL STUD
FRAMED WALLS AND FC LININGS TO
DOCUMENT STORAGE AND TOILET

LANDSCAPE STORAGE
CONC

DOCUMENT STORAGE
CONC

PROPOSED FLOOR PLAN

SCALE : 1 : 50

ABBREVIATIONS

ABREVIATION	DESCRIPTION
DP	DOWNPIPE - PVC
LT1	INTERNAL LIGHT - AS PER ELECTRICAL ENGINEER
LT2	INTERNAL LIGHT - AS PER ELECTRICAL ENGINEER
LT3	INTERNAL LIGHT - AS PER ELECTRICAL ENGINEER
LT4	EXTERNAL LIGHT - AS PER ELECTRICAL ENGINEER
MEG	METAL EAVES GUTTER - COLORBOND
MG	MIRROR GLASS
MRS	METAL ROOF SHEETING - COLORBOND
MXT	MIXER - BASIN
RC	RIDGE CAPPING
SK-CT	CERAMIC TILE SKIRTING
SNK	SINK - STAINLESS STEEL
VDN	VANITY BASIN
WC	TOILET SUITE

LEGEND

FLOOR FINISHES

CT	CERAMIC TILES
CONC	CONCRETE FLOOR

WALL FINISHES

WT-A	TRIMDEK CLADDING ON TOP HAT BATTENS FIXED TO 76mm STEEL STUD WALL
WT-B	9mm FC LINING BOTH SIDES FIXED TO 76mm STEEL STUD WALL
WT-C	9mm FC LINING ONE SIDE FIXED TO 64mm STEEL STUD WALL

CEILING FINISHES


FC	FIBRE CEMENT SHEETING
----	-----------------------

WINDOW SCHEDULE

MARK	WINDOW STYLE	HEIGHT	WIDTH	MATERIAL	GLAZING	REMARKS
01	XO SLIDING WINDOW	600	1200	ALUMINIUM	CLEAR GLASS	USE EXISTING WINDOWS WHERE POSSIBLE
02	XO SLIDING WINDOW	600	1500	ALUMINIUM	CLEAR GLASS	USE EXISTING WINDOWS WHERE POSSIBLE
03	XO SLIDING WINDOW	600	600	ALUMINIUM	OPAQUE GLASS	USE EXISTING WINDOWS WHERE POSSIBLE
04	XO SLIDING WINDOW	600	600	ALUMINIUM	OPAQUE GLASS	USE EXISTING WINDOWS WHERE POSSIBLE

DOOR SCHEDULE

MARK	HEIGHT	WIDTH	FINISH	FRAME MATERIAL	COMMENTS
01	2700	2050	STEEL	STEEL	ROLLER DOOR TO MATCH COLORBOND WALL CLADDING
02	2100	820	TIMBER SOLID CORE	STEEL	
03	2100	920	TIMBER SOLID CORE	STEEL	

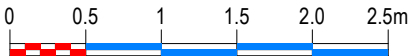

SCALE 1:50 A3



CONTOUR

SUNSHINE COAST OFFICE
Building A, Level 1,
6 Innovation Parkway,
Birtinya, 4575, Qld
Ph. (07) 5493 9777
Website: www.ContourCE.com.au

NORTH LAKES OFFICE
Corporate Suite A, Bld 2
2 - 4 Flinders Parade,
North Lakes, 4509, Qld
Ph. (07) 5493 9777
Email: admin@contource.com.au

A.B.N. 62 117 061 659



PLAN DETAILS:

Designed: **JT**
Drawn: **JT**
Checked: **PB**
Datum:
Date: **20/12/2021**
11:42:22 AM

PLAN AMENDMENTS:

Rev	Date	Comment	Altered	Checked
B	20.12.2021	FOR TENDER	JT	PB

PROPOSED SHED REFURBISHMENT
48 SIPPY CREEK RD, TANAWHA
SUNSHINE COAST REGIONAL COUNCIL

© This plan is Copyright. Other than for the purposes of and subject to the conditions prescribed under the Copyright Act, no part of it may in any form or by any means be reproduced, stored in a retrieval system or transmitted without the prior written permission of Contour Consulting Engineers. The plan shall not be used for construction without prior written approval.


PLAN TITLE:

FLOOR PLANS


PLAN No: **1417 03 300**

FOR TENDER

REVISION: **B**

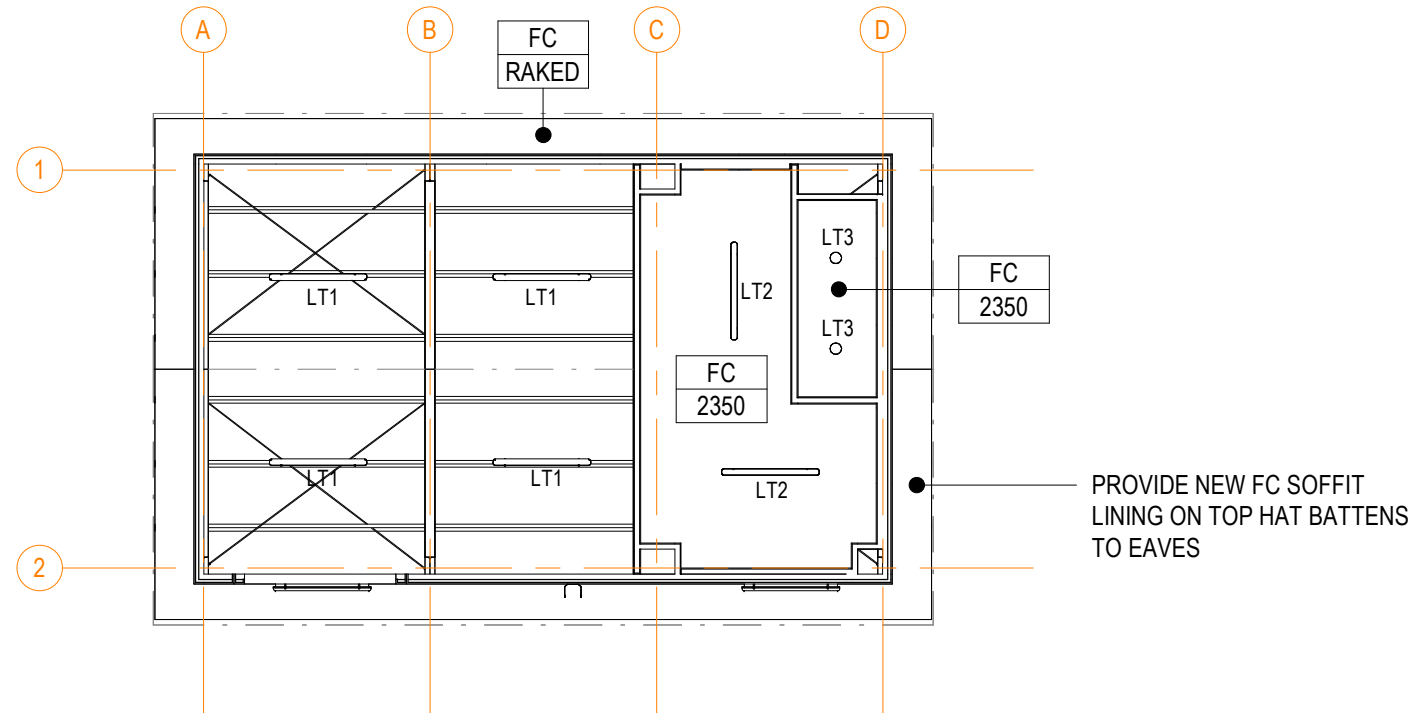

REFLECTIVE CEILING PLAN
SCALE : 1 : 100

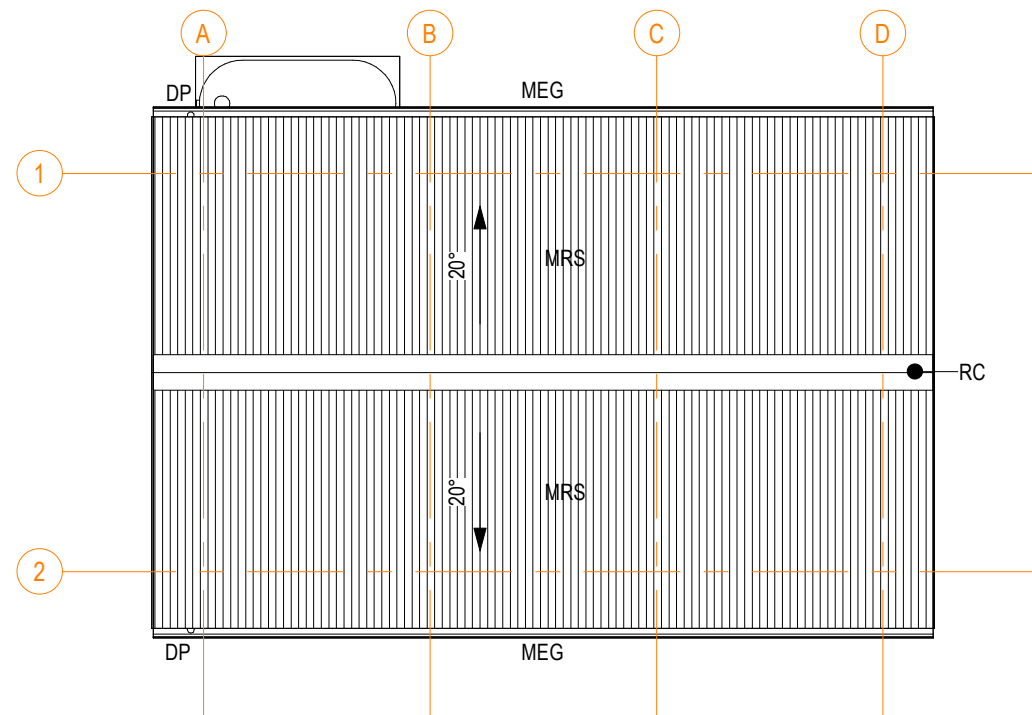

ROOF PLAN
SCALE : 1 : 100

ABBREVIATIONS	
ABREVIATION	DESCRIPTION
DP	DOWNPIPE - PVC
LT1	INTERNAL LIGHT - AS PER ELECTRICAL ENGINEER
LT2	INTERNAL LIGHT - AS PER ELECTRICAL ENGINEER
LT3	INTERNAL LIGHT - AS PER ELECTRICAL ENGINEER
LT4	EXTERNAL LIGHT - AS PER ELECTRICAL ENGINEER
MEG	METAL EAVES GUTTER - COLORBOND
MG	MIRROR GLASS
MRS	METAL ROOF SHEETING - COLORBOND
MXT	MIXER - BASIN
RC	RIDGE CAPPING
SK-CT	CERAMIC TILE SKIRTING
SNK	SINK - STAINLESS STEEL
VBN	VANITY BASIN
WC	TOILET SUITE

LEGEND

FLOOR FINISHES


CT	CERAMIC TILES
CONC	CONCRETE FLOOR

WALL FINISHES

WT-A	TRIMDEK CLADDING ON TOP HAT BATTENS FIXED TO 76mm STEEL STUD WALL
WT-B	9mm FC LINING BOTH SIDES FIXED TO 76mm STEEL STUD WALL
WT-C	9mm FC LINING ONE SIDE FIXED TO 64mm STEEL STUD WALL

CEILING FINISHES

FC	FIBRE CEMENT SHEETING
----	-----------------------

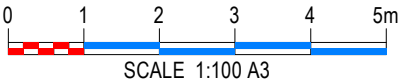



CONTOUR

SUNSHINE COAST OFFICE
Building A, Level 1,
6 Innovation Parkway,
Birtinya, 4575, Qld
Ph. (07) 5493 9777
Website: www.ContourCE.com.au

NORTH LAKES OFFICE
Corporate Suite A, Bld 2
2 - 4 Flinders Parade,
North Lakes, 4509, Qld
Ph. (07) 5493 9777
Email: admin@contource.com.au

A.B.N. 62 117 061 659



PLAN DETAILS:

Designed:	JT
Drawn:	JT
Checked:	PB
Datum:	
Date:	20/12/2021 11:42:23 AM

PLAN AMENDMENTS:

Rev	Date	Comment	Altered	Checked
B	20.12.2021	FOR TENDER	JT	PB

PROPOSED SHED REFURBISHMENT
48 SIPPY CREEK RD, TANAWHA
SUNSHINE COAST REGIONAL COUNCIL

© This plan is Copyright. Other than for the purposes of and subject to the conditions prescribed under the Copyright Act, no part of it may in any form or by any means be reproduced, stored in a retrieval system or transmitted without the prior written permission of Contour Consulting Engineers. The plan shall not be used for construction without prior written approval.

PLAN TITLE:

REFLECTIVE CEILING & ROOF PLANS

FOR TENDER


PLAN No: **1417 03 301**

REVISION: **B**



CONTRACTOR TO CONTACT STRUCTURAL ENGINEER FOR APPROVAL IF ANY MEMBERS DO NOT MATCH THE NOMINATED SPECIFICATION OR SEVERE CORROSION IS IDENTIFIED DURING DEMOLITION


CONTRACTOR TO TREAT ALL EXISTING STEEL MEMBERS & CONNECTIONS WITH A WIRE BRUSH, APPROVED RUST CONVERTER AND AN APPROVED PROTECTIVE COATING SYSTEM. REPLACE DETERIORATED BOLTS/NUTS AS REQUIRED

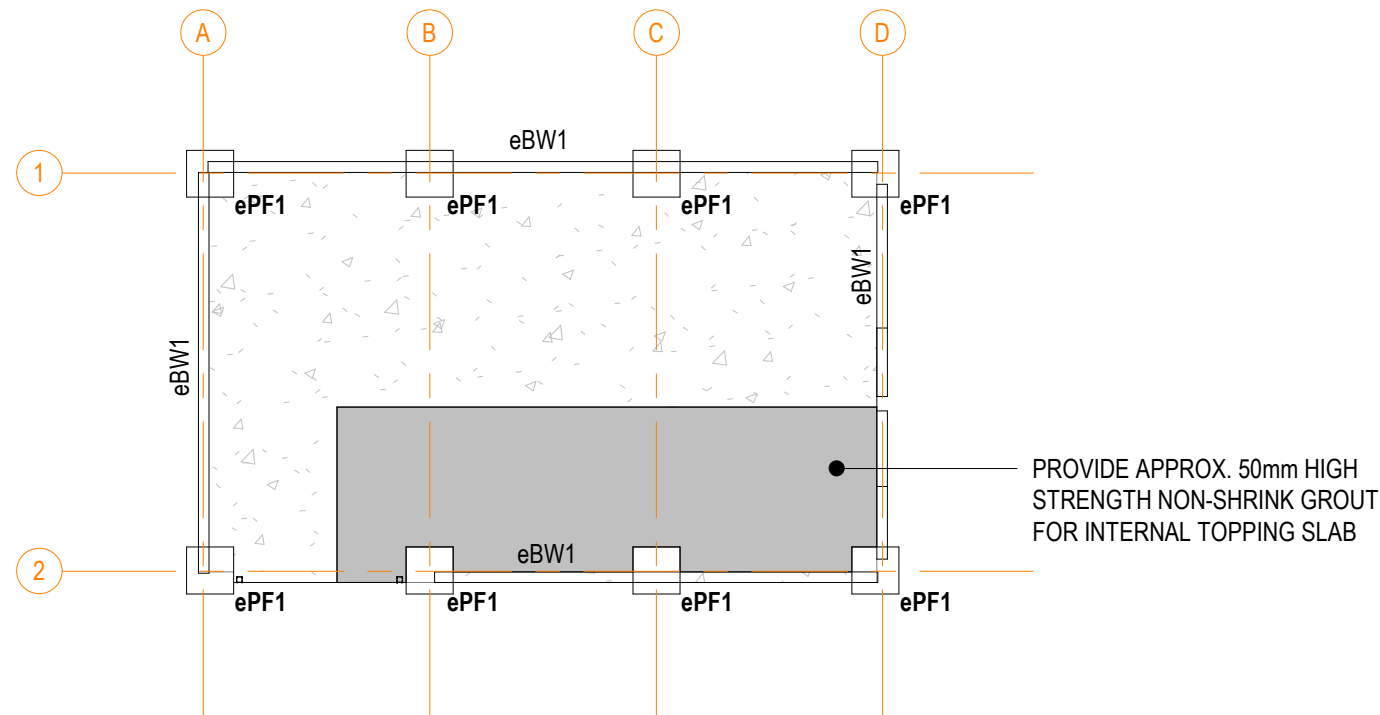

FOOTING & SLAB PLAN

SCALE : 1 : 100

PROVIDE NEW STEEL STRUTS FIXED TO EXISTING PORTAL FRAMES

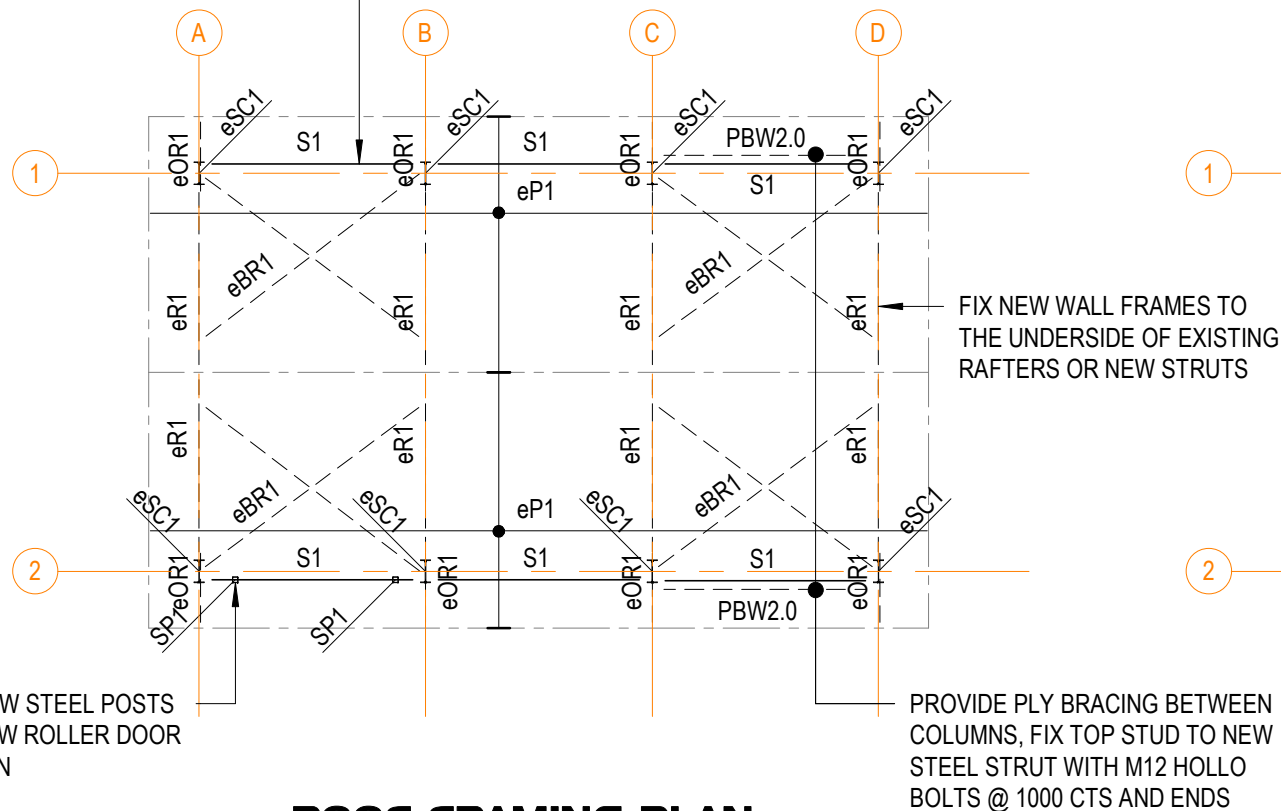


ROOF FRAMING PLAN

SCALE : 1 : 100

PROVIDE NEW STEEL POSTS FOR THE NEW ROLLER DOOR CONNECTION

PROVIDE PLY BRACING BETWEEN COLUMNS, FIX TOP STUD TO NEW STEEL STRUT WITH M12 HOLLO BOLTS @ 1000 CTS AND ENDS

PROVIDE NEW STEEL STUD WALL SYSTEM TO MANUFACTURERS SPECIFICATIONS

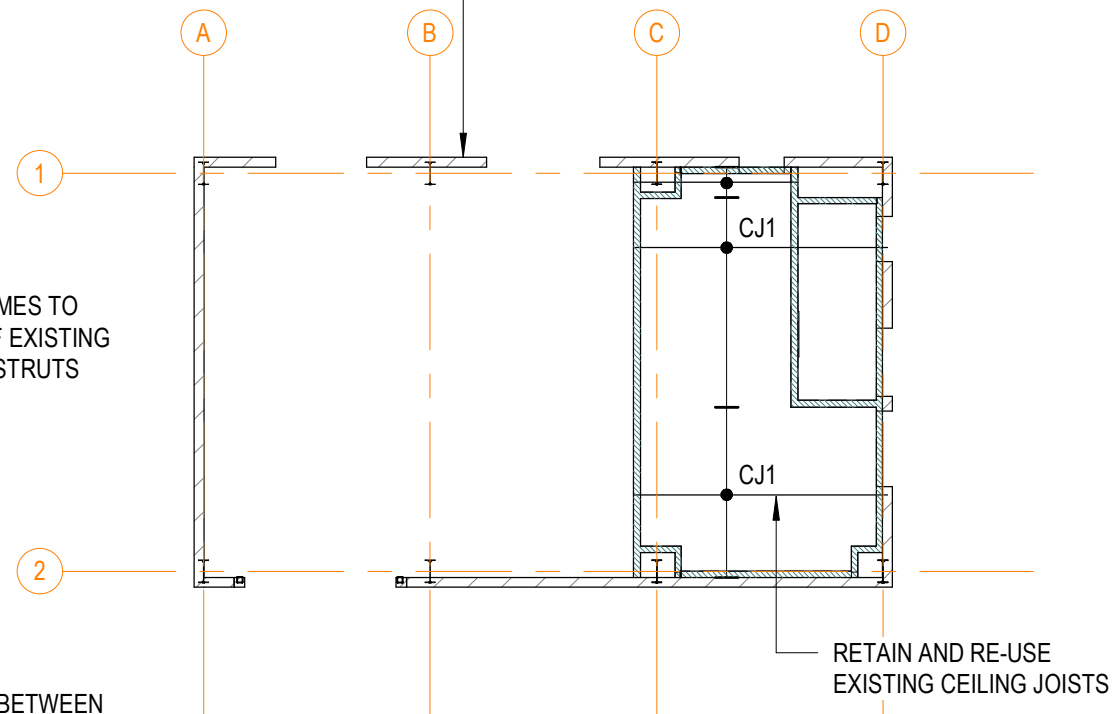

CEILING FRAMING PLAN

SCALE : 1 : 100

SCHEDULE

FOOTINGS	
ePF1	EXISTING 620SQ x 600DEEP RAISED CONCRETE PAD FOOTING
FOOTINGS	
eBW1	EXISTING 150 SERIES MASONRY WALL
COLUMNS/POSTS	
eSC1	EXISTING 300DEEP CASTELLATED STEEL COLUMN
SP1	75x3.5 SHS STEEL POST
ROOF FRAME	
eR1	EXISTING 300DEEP CASTELLATED STEEL RAFTERS
eOR1	EXISTING 75EA OUTRIGGER
eP1	EXISTING 125x38 HWD PURLINS @900CTS TYPICALLY
BRACING	
S1	75x3.5 SHS STRUT
PBW	6mm PLY BRACING WALL FIXED WITH 10g TEK SCREWS @ 150CTS TO STUDS AND NOGGINGS.
eBR1	12DIA BRACING ROD

LEGEND

	M12 ROD
	PBW1.2
	PLY BRACING WALL 1.2 LONG
	LOAD BEARING STRUCTURAL ELEMENT UNDER
	LOAD BEARING STRUCTURAL ELEMENT OVER

GENERAL NOTES

- REFER SHEET 110 FOR GENERAL NOTES

SETOUT AND LEVELS

REFER ARCHITECT'S DRAWINGS FOR ALL LEVELS, CLEARANCES, STEPS, FALLS AND SETOUT.

TIMBER CLASS


CLASS 3 AND 4 TIMBERS CLEAR OF THE GROUND AND EXPOSED TO THE WEATHER TO BE PRESERVATIVE TREATED TO MIN. LEVEL H3, WHERE THESE TIMBERS ARE IN CONTACT WITH THE GROUND PRESERVATIVE TREATMENT TO BE MIN. H5

TIMBER PROTECTION

ENGINEERED TIMBER PRODUCTS ARE TO BE PROTECTED FROM THE WEATHER DURING CONSTRUCTION. THOSE PRODUCTS TO BE USED IN A PERMANENT EXTERNAL ENVIRONMENT SHALL BE END AND TOP CAPPED. ALL MEMBERS SHALL BE PRIMED AND PAINTED IN ACCORDANCE WITH THE MANUFACTURERS SPECIFICATIONS TO ENSURE CONTINUED SATISFACTORY PERFORMANCE OF THE MEMBER. REFER TO MANUFACTURERS SPECIFICATIONS FOR PARTICULAR DETAILS RELATING TO INDIVIDUAL PRODUCTS

TIE DOWN AND BRACING NOTE

CONTRACTOR TO ENSURE ALL TIE DOWN TO BE CONTINUOUS TO SLAB ON GROUND. REFER TO MANUFACTURERS SPECIFICATIONS FOR PARTICULAR PRODUCT DETAILS.

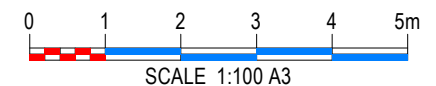

PLAN DETAILS:

Designed: JT
Drawn: JT
Checked: PB
Datum: JT
Date: 20/12/2021
11:42:23 AM

PLAN AMENDMENTS:

Rev	Date	Comment	Altered	Checked
B	20.12.2021	FOR TENDER	JT	PB

PROPOSED SHED REFURBISHMENT 48 SIPPY CREEK RD, TANAWHA SUNSHINE COAST REGIONAL COUNCIL

© This plan is Copyright. Other than for the purposes of and subject to the conditions prescribed under the Copyright Act, no part of it may in any form or by any means be reproduced, stored in a retrieval system or transmitted without the prior written permission of Contour Consulting Engineers. The plan shall not be used for construction without prior written approval.


PLAN TITLE:

STRUCTURAL FRAMING PLANS


PLAN No: 1417 03 302

FOR TENDER

REVISION: B

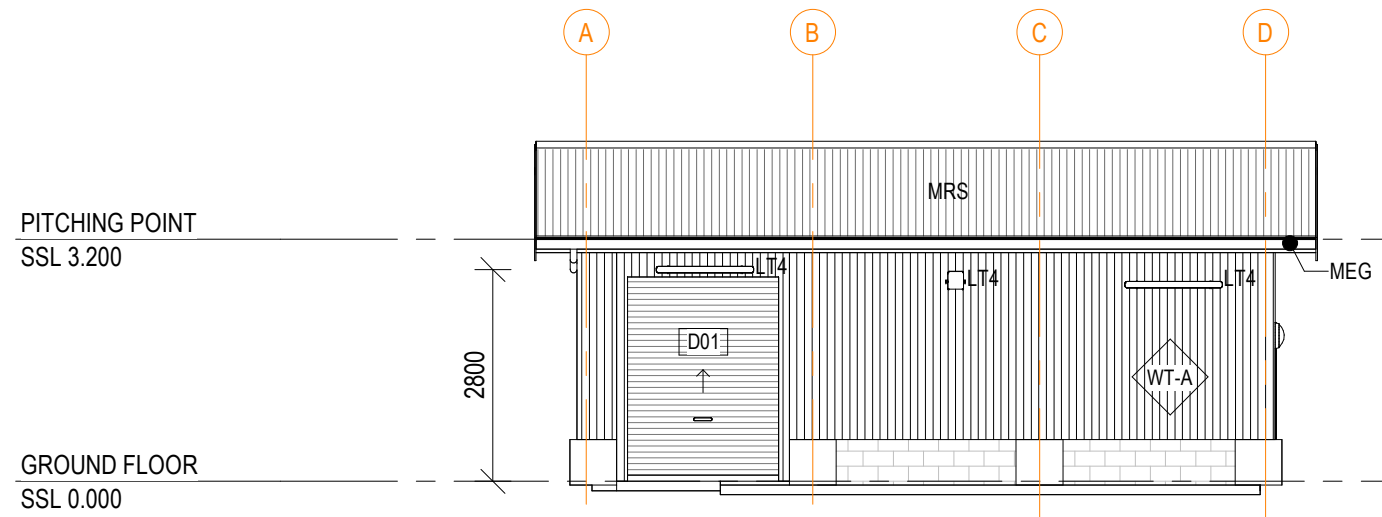


A
300
ELEVATION
SCALE : 1 : 100

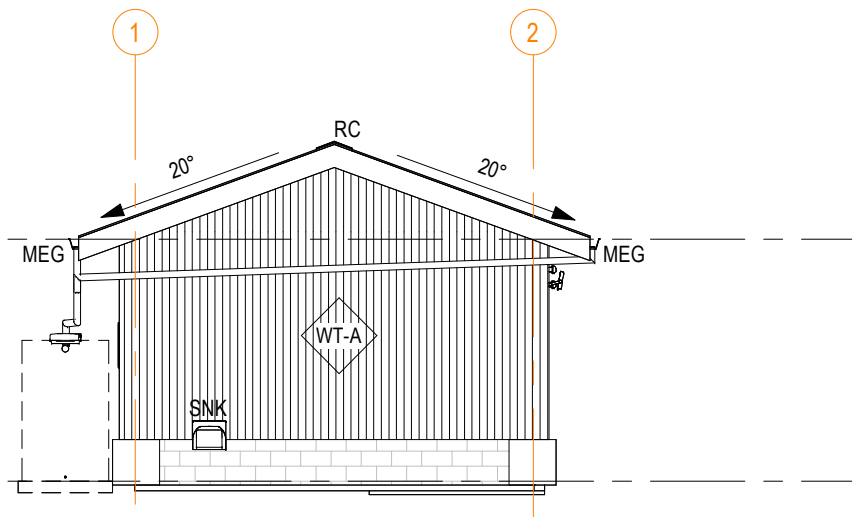


B
300
ELEVATION
SCALE : 1 : 100

- LEGEND**
- FLOOR FINISHES**
 CT CERAMIC TILES
 CONC CONCRETE FLOOR
- WALL FINISHES**
 WT-A TRIMDEK CLADDING ON TOP HAT BATTENS
 FIXED TO 76mm STEEL STUD WALL
 WT-B 9mm FC LINING BOTH SIDES FIXED TO 76mm
 STEEL STUD WALL
 WT-C 9mm FC LINING ONE SIDE FIXED TO 64mm
 STEEL STUD WALL
- CEILING FINISHES**
 FC FIBRE CEMENT SHEETING


ABBREVIATIONS	
ABREVIATION	DESCRIPTION
DP	DOWNPIPE - PVC
LT1	INTERNAL LIGHT - AS PER ELECTRICAL ENGINEER
LT2	INTERNAL LIGHT - AS PER ELECTRICAL ENGINEER
LT3	INTERNAL LIGHT - AS PER ELECTRICAL ENGINEER
LT4	EXTERNAL LIGHT - AS PER ELECTRICAL ENGINEER
MEG	METAL EAVES GUTTER - COLORBOND
MG	MIRROR GLASS
MRS	METAL ROOF SHEETING - COLORBOND
MXT	MIXER - BASIN
RC	RIDGE CAPPING
SK-CT	CERAMIC TILE SKIRTING
SNK	SINK - STAINLESS STEEL
VBN	VANITY BASIN
WC	TOILET SUITE

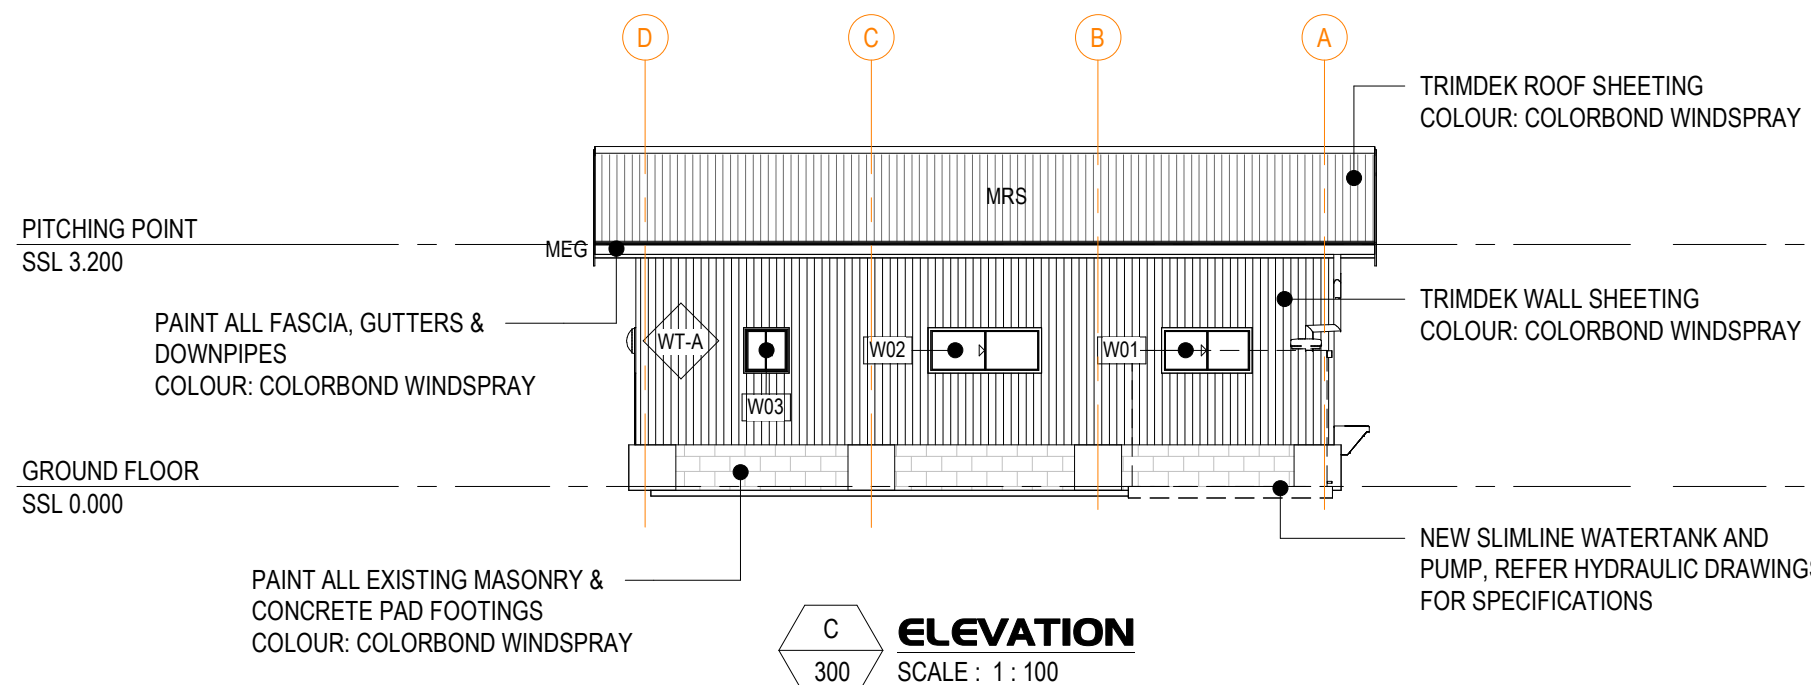

C
300
ELEVATION
SCALE : 1 : 100

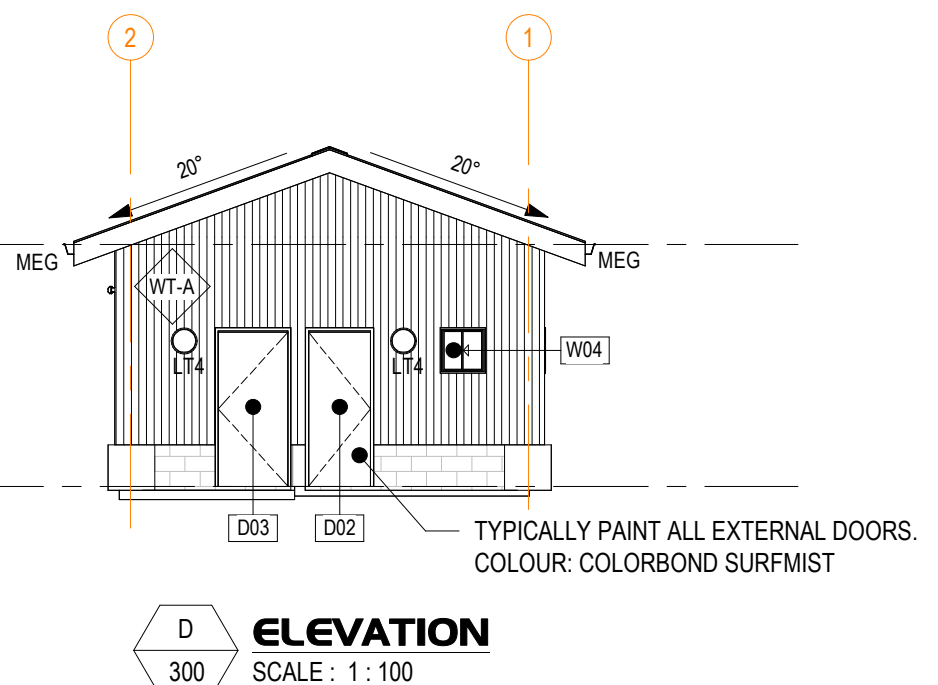

D
300
ELEVATION
SCALE : 1 : 100

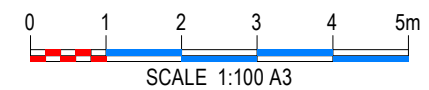

CONTOUR

SUNSHINE COAST OFFICE
 Building A, Level 1,
 6 Innovation Parkway,
 Birtinya, 4575, Qld
 Ph. (07) 5493 9777
 Website: www.ContourCE.com.au

NORTH LAKES OFFICE
 Corporate Suite A, Bld 2
 2 - 4 Flinders Parade,
 North Lakes, 4509, Qld
 Ph. (07) 5493 9777
 Email: admin@contource.com.au

ABN 62 117 061 659

ISO 14001:2015
 UKAS
 MANAGEMENT
 SYSTEMS
 8007

PLAN DETAILS:		PLAN AMENDMENTS:		Altered	Checked
Designed:	JT	Rev	Date	Comment	
Drawn:	JT	B	20.12.2021	FOR TENDER	
Checked:	PB				
Date:	20/12/2021				
	11:42:24 AM				

PROPOSED SHED REFURBISHMENT
48 SIPPY CREEK RD, TANAWHA
SUNSHINE COAST REGIONAL COUNCIL


© This plan is Copyright. Other than for the purposes of and subject to the conditions prescribed under the Copyright Act, no part of it may in any form or by any means be reproduced, stored in a retrieval system or transmitted without the prior written permission of Contour Consulting Engineers. The plan shall not be used for construction without prior written approval.

PLAN TITLE:
EXTERNAL ELEVATIONS


PLAN No: **1417 03 310**

REVISION: **B**


FOR TENDER

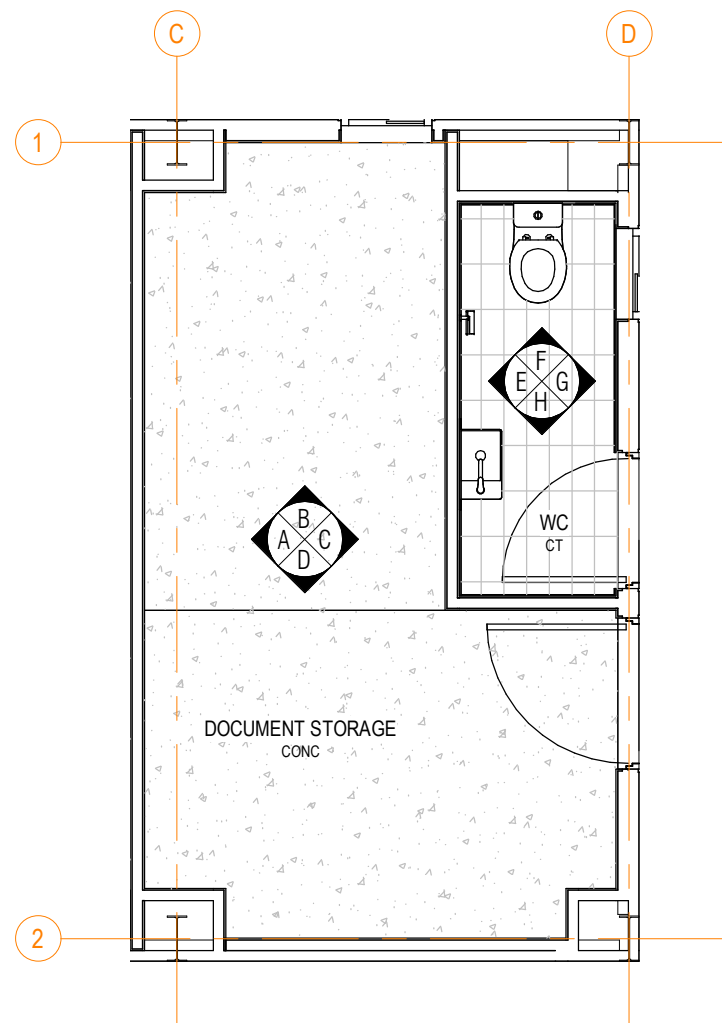

**DOCUMENT STORAGE AND TOILET
KEY PLAN**
SCALE : 1 : 50

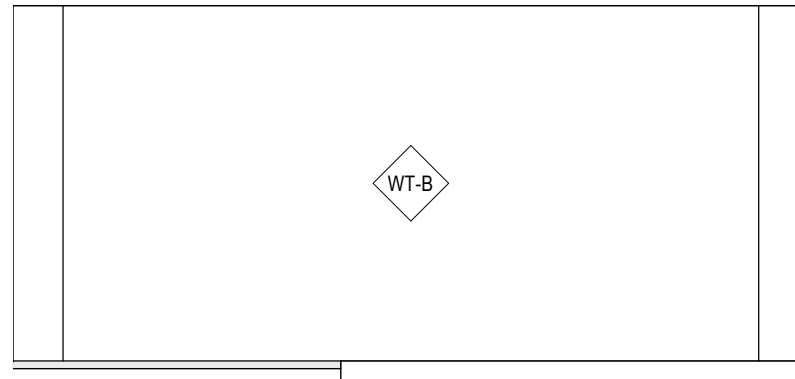


**A
311**
ELEVATION
SCALE : 1 : 50

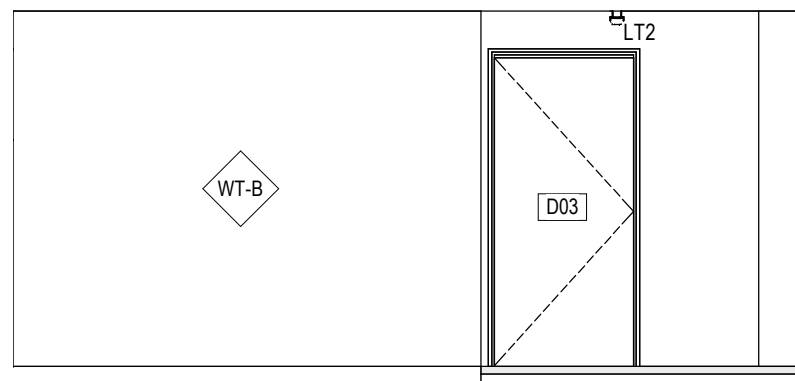


**C
311**
ELEVATION
SCALE : 1 : 50


TYPICALLY FRAME AND
SHEET AROUND EXISTING
STEEL COLUMNS

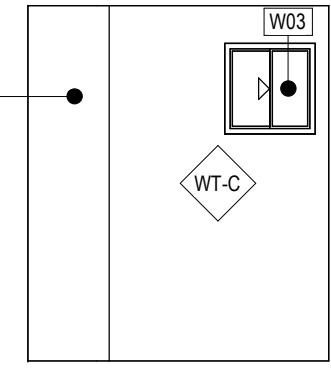


**B
311**
ELEVATION
SCALE : 1 : 50

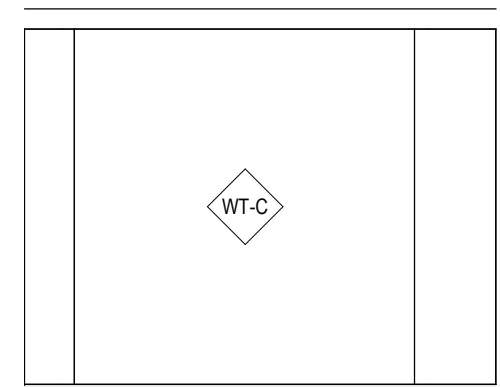


**D
311**
ELEVATION
SCALE : 1 : 50

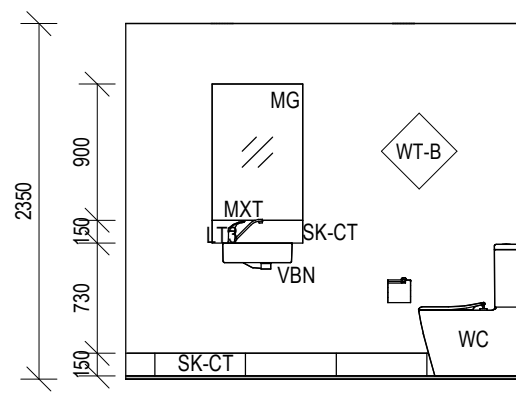


**E
311**
ELEVATION
SCALE : 1 : 50

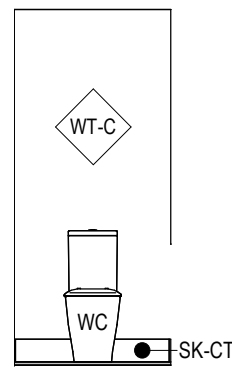

**F
311**
ELEVATION
SCALE : 1 : 50

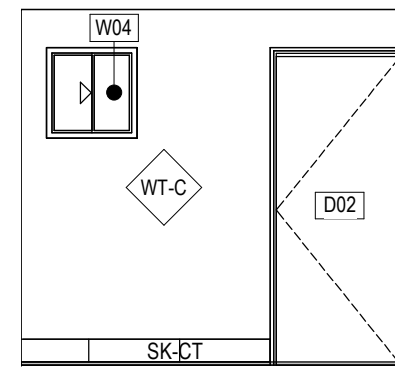

**G
311**
ELEVATION
SCALE : 1 : 50

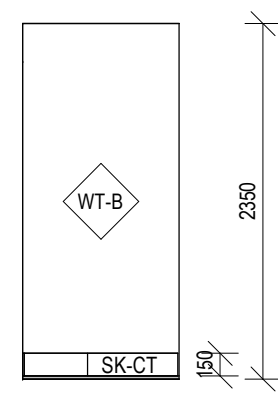

**H
311**
ELEVATION
SCALE : 1 : 50

PLAN DETAILS:

Designed: **JT**
Drawn: **JT**
Checked: **PB**
Datum: **20/12/2021**
Date: **11:42:24 AM**

PLAN AMENDMENTS:

Rev	Date	Comment	Altered	Checked
B	20.12.2021	FOR TENDER	JT	PB

**PROPOSED SHED REFURBISHMENT
48 SIPPY CREEK RD, TANAWHA
SUNSHINE COAST REGIONAL COUNCIL**

© This plan is Copyright. Other than for the purposes of and subject to the conditions prescribed under the Copyright Act, no part of it may in any form or by any means be reproduced, stored in a retrieval system or transmitted without the prior written permission of Contour Consulting Engineers. The plan shall not be used for construction without prior written approval.

PLAN TITLE:

INTERNAL ELEVATIONS

PLAN No: **1417 03 311**

FOR TENDER

REVISION: **B**

LEGEND

FLOOR FINISHES

CT CERAMIC TILES
CONC CONCRETE FLOOR

WALL FINISHES

WT-A TRIMDEK CLADDING ON TOP HAT BATTENS
FIXED TO 76mm STEEL STUD WALL
WT-B 9mm FC LINING BOTH SIDES FIXED TO 76mm
STEEL STUD WALL
WT-C 9mm FC LINING ONE SIDE FIXED TO 64mm
STEEL STUD WALL


CEILING FINISHES

FC FIBRE CEMENT SHEETING

SUSPEND LIGHTS OFF EXISTING
PURLINS TO AVOID CROSS
BRACING BELOW.

PITCHING POINT
SSL 3.200

GROUND FLOOR
SSL 0.000

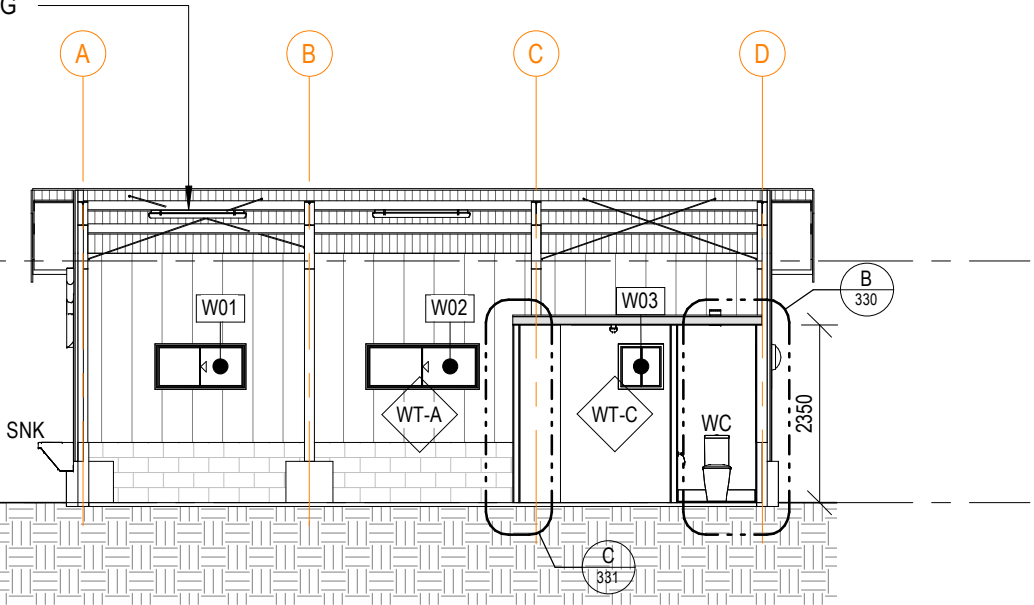


E
300
SECTION
SCALE : 1 : 100

ABBREVIATIONS

ABREVIATION	DESCRIPTION
DP	DOWNPIPE - PVC
LT1	INTERNAL LIGHT - AS PER ELECTRICAL ENGINEER
LT2	INTERNAL LIGHT - AS PER ELECTRICAL ENGINEER
LT3	INTERNAL LIGHT - AS PER ELECTRICAL ENGINEER
LT4	EXTERNAL LIGHT - AS PER ELECTRICAL ENGINEER
MEG	METAL EAVES GUTTER - COLORBOND
MG	MIRROR GLASS
MRS	METAL ROOF SHEETING - COLORBOND
MXT	MIXER - BASIN
RC	RIDGE CAPPING
SK-CT	CERAMIC TILE SKIRTING
SNK	SINK - STAINLESS STEEL
VBN	VANITY BASIN
WC	TOILET SUITE

PITCHING POINT
SSL 3.200


GROUND FLOOR
SSL 0.000

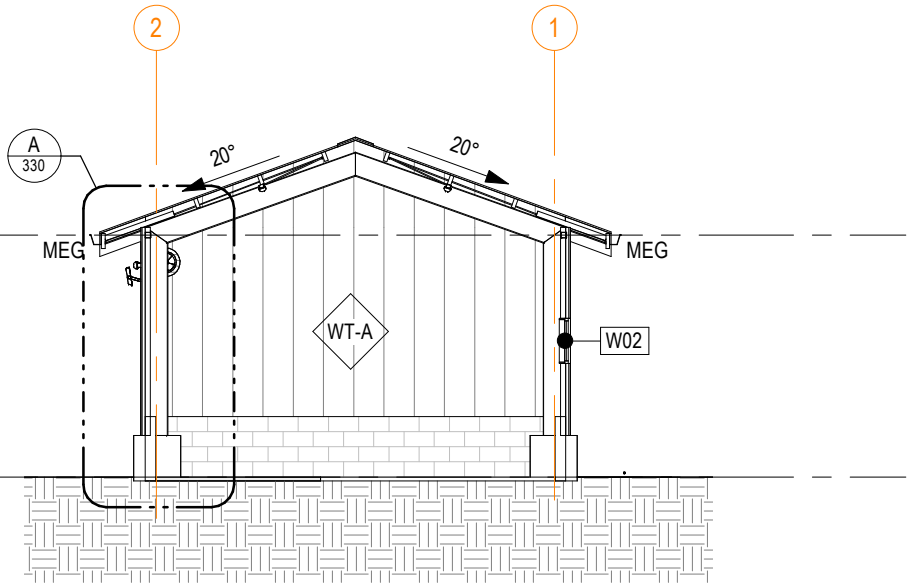


F
300
SECTION
SCALE : 1 : 100

PITCHING POINT
SSL 3.200

GROUND FLOOR
SSL 0.000

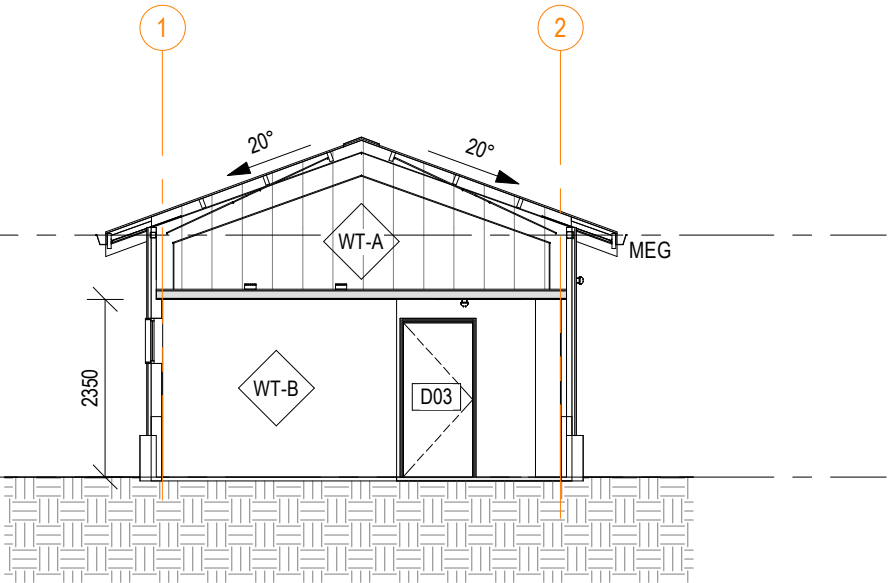

G
300
SECTION
SCALE : 1 : 100

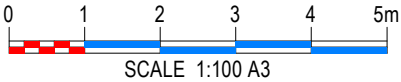

PLAN DETAILS:

Designed: JT
Drawn: JT
Checked: PB
Datum: 20/12/2021
Date: 11:42:25 AM

PLAN AMENDMENTS:

Rev	Date	Comment	Altered	Checked
B	20.12.2021	FOR TENDER	JT	PB

**PROPOSED SHED REFURBISHMENT
48 SIPPY CREEK RD, TANAWHA
SUNSHINE COAST REGIONAL COUNCIL**

© This plan is Copyright. Other than for the purposes of and subject to the conditions prescribed under the Copyright Act, no part of it may in any form or by any means be reproduced, stored in a retrieval system or transmitted without the prior written permission of Contour Consulting Engineers. The plan shall not be used for construction without prior written approval.


PLAN TITLE:

SECTIONS

PLAN No: **1417 03 312**

FOR TENDER

REVISION: **B**

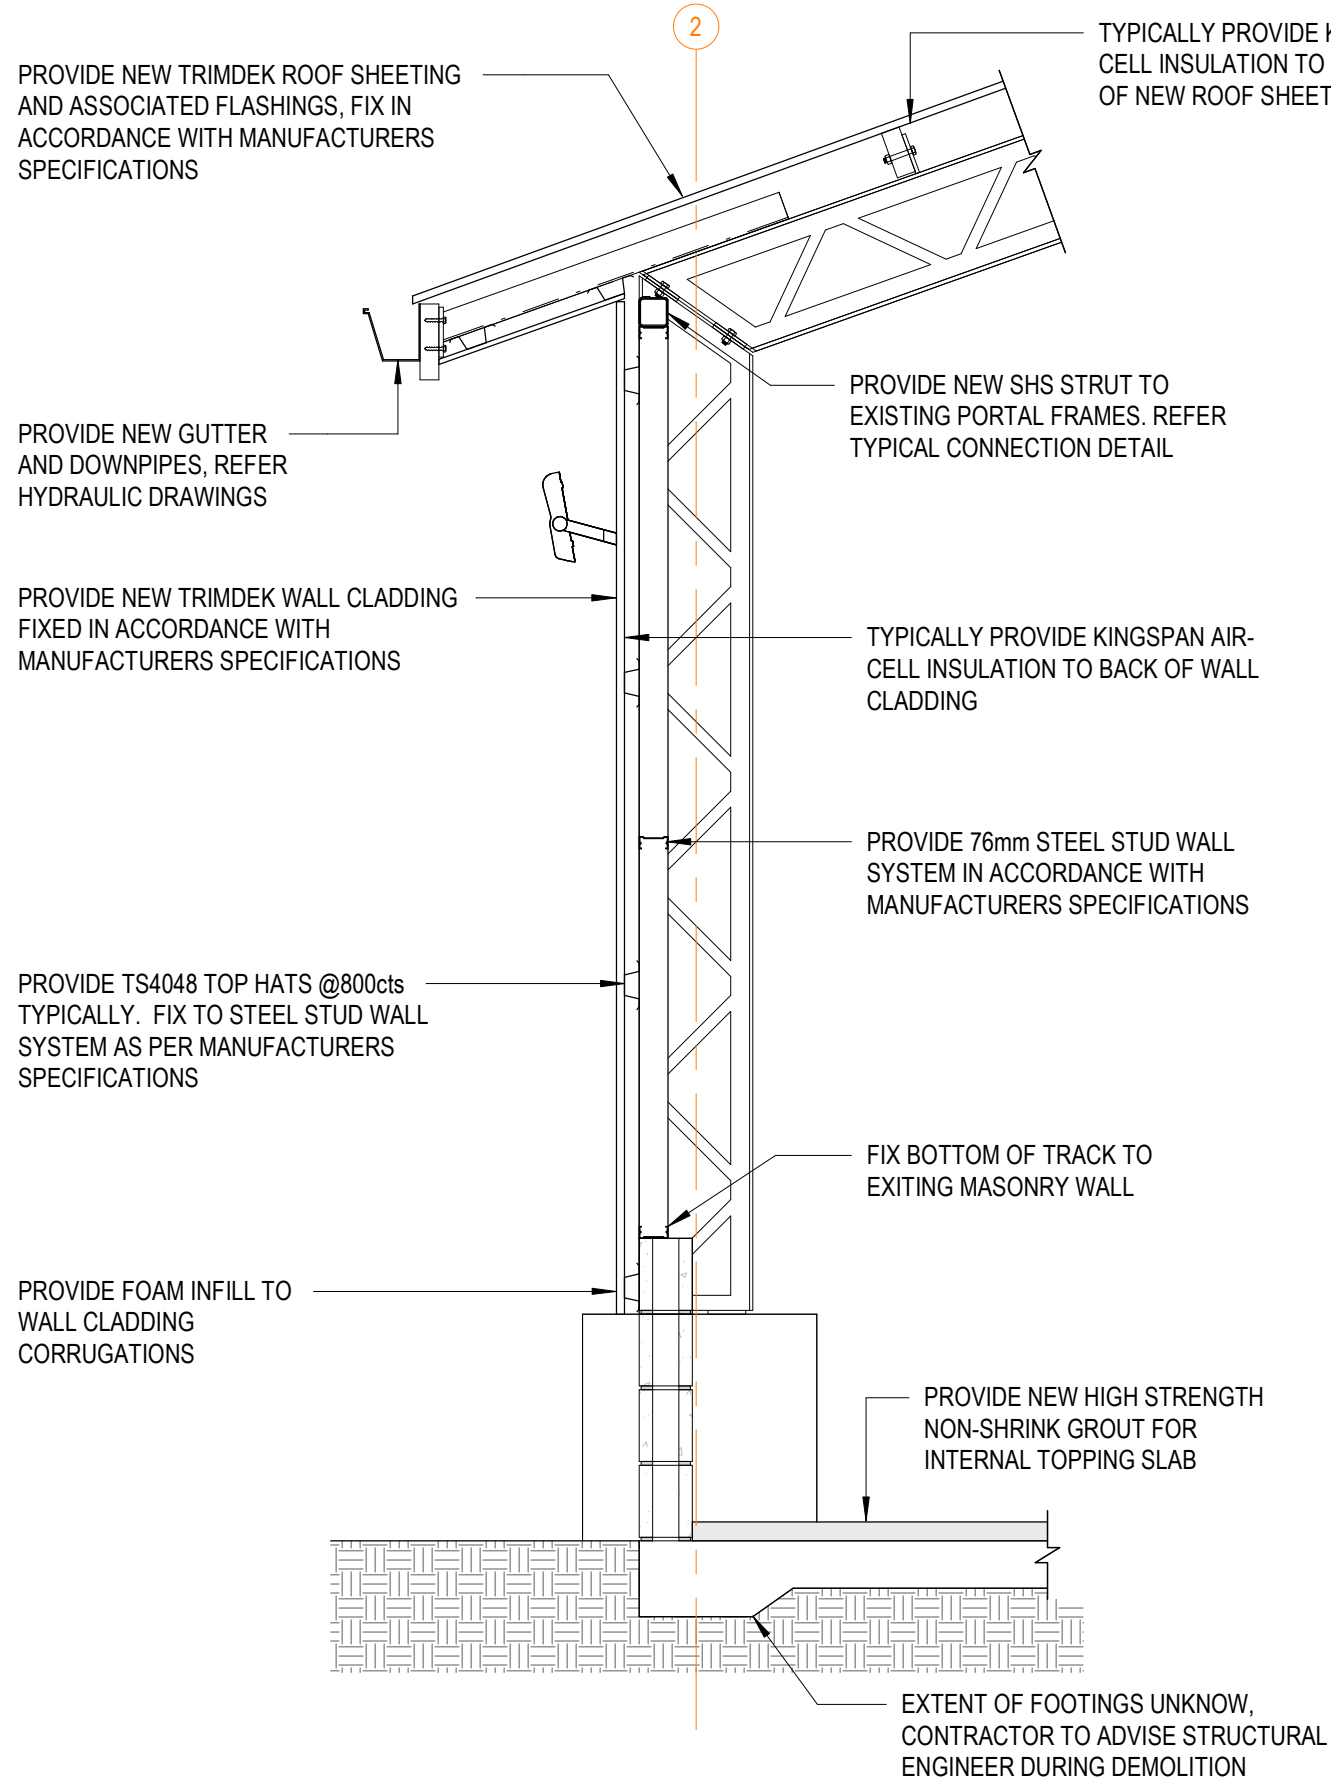

A
312
DETAIL
SCALE : 1 : 20

RE-USE EXISTING CEILING JOISTS @ 450cts TYPICAL. FIX TO STEEL STUD FRAMING WITH 1/FRAMING ANCHOR WITH 4/10g TEK SCREWS PER LEG.

PROVIDE NEW LIGHT FIXTURES IN ACCORDANCE WITH ELECTRICAL ENGINEERS DRAWINGS


PROVIDE 76mm STEEL STUD WALL SYSTEM FOR EXTERNAL WALL CLADDING IN ACCORDANCE WITH MANUFACTURERS SPECIFICATIONS

TYPICALLY PROVIDE KINGSPAN AIR-CELL INSULATION TO BACK OF WALL CLADDING


PROVIDE 64mm STEEL STUD WALL SYSTEM TO FOR INTERNAL WALL LININGS IN ACCORDANCE WITH MANUFACTURERS SPECIFICATIONS

PROVIDE NEW 9mm FC WALL/ CEILING LININGS, DIRECT FIXED TO STUD WALL AND EXISTING MASONRY WALLS

PROVIDE NEW 600x600 FLOOR TILES AND 150x600 WALL SKIRTING TILES TO TOILET

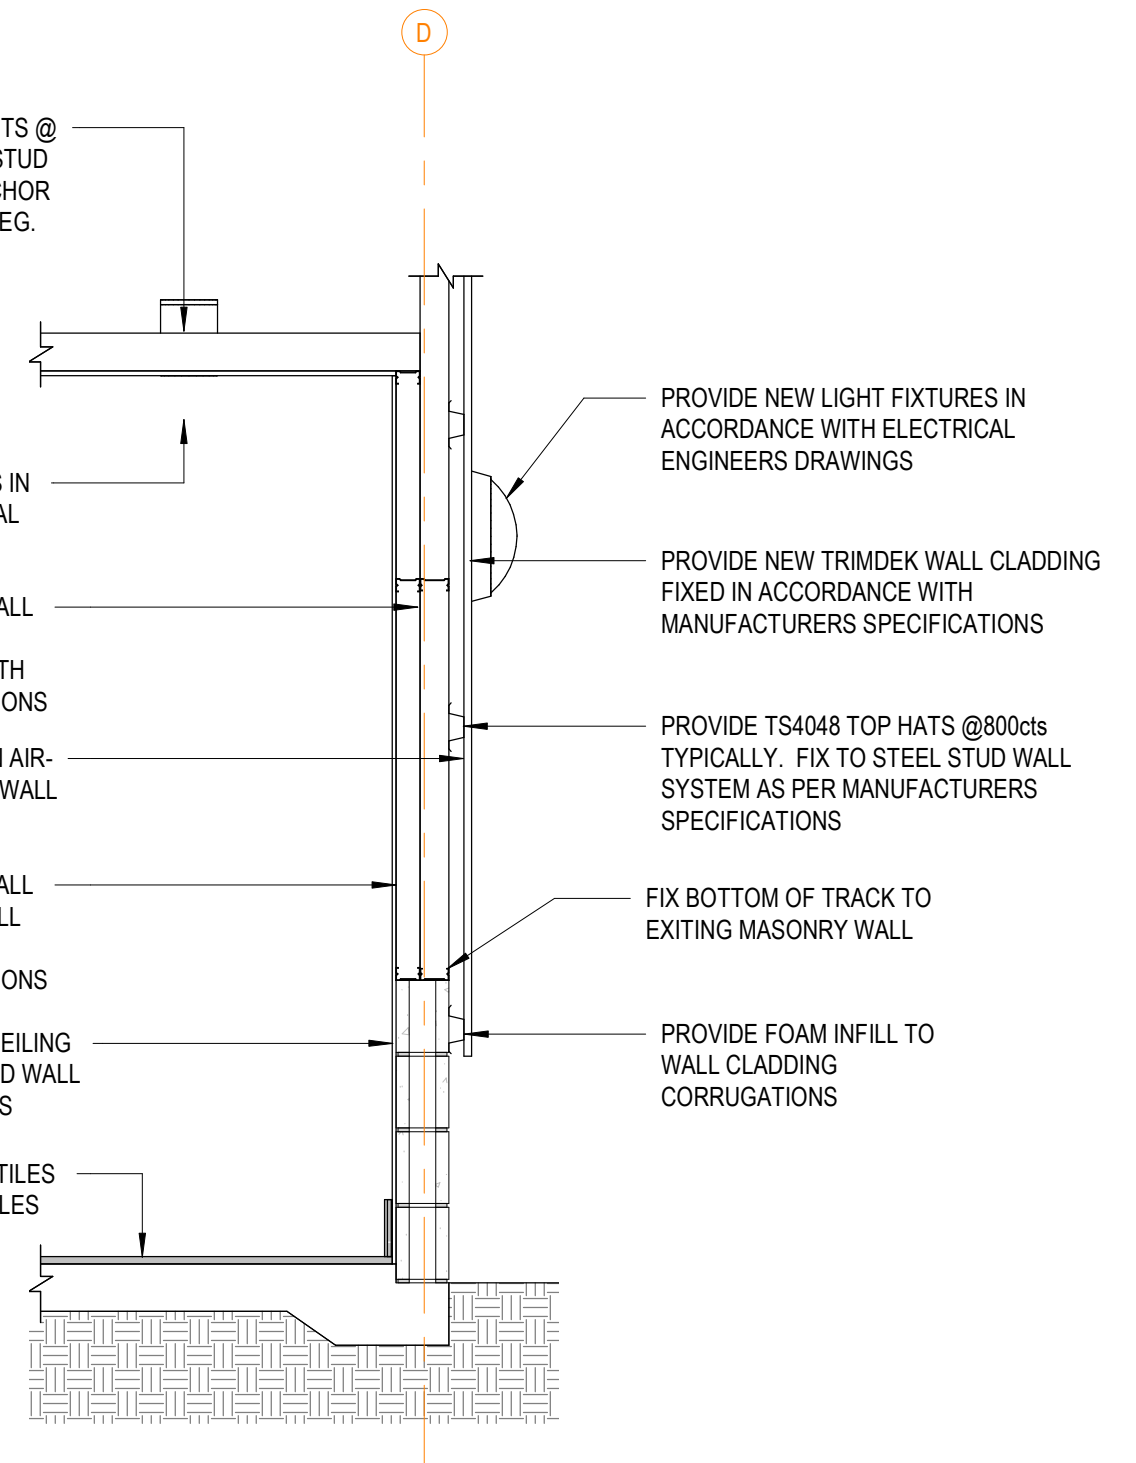

B
312
DETAIL
SCALE : 1 : 20

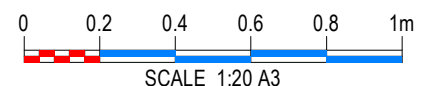

PLAN DETAILS:

Designed: JT
Drawn: JT
Checked: PB
Datum: 20/12/2021
Date: 11:42:25 AM

PLAN AMENDMENTS:

Rev	Date	Comment	Altered	Checked
B	20.12.2021	FOR TENDER	JT	PB

**PROPOSED SHED REFURBISHMENT
48 SIPPY CREEK RD, TANAWHA
SUNSHINE COAST REGIONAL COUNCIL**

© This plan is Copyright. Other than for the purposes of and subject to the conditions prescribed under the Copyright Act, no part of it may in any form or by any means be reproduced, stored in a retrieval system or transmitted without the prior written permission of Contour Consulting Engineers. The plan shall not be used for construction without prior written approval.

PLAN TITLE:

DETAILED SECTIONS - SHEET 1

PLAN No: **1417 03 330**

FOR TENDER

REVISION: **B**

RE-USE EXISTING CEILING JOISTS @ 450cts TYPICAL. FIX TO STEEL STUD FRAMING WITH 1/FRAMING ANCHOR WITH 4/10g TEK SCREWS PER LEG.


PROVIDE 76mm STEEL STUD WALL SYSTEM FOR INTERNAL LOAD BEARING WALLS IN ACCORDANCE WITH MANUFACTURERS SPECIFICATIONS

PROVIDE NEW 9mm FC WALL LININGS, DIRECT FIXED TO STUD WALL AND EXISTING MASONRY WALLS

PROVIDE NEW 9mm FC CEILING LININGS, DIRECT FIXED TO CEILING JOISTS


FIX BOTTOM OF TRACK TO EXISTING CONCRETE SLAB

C
312
DETAIL
SCALE : 1 : 20

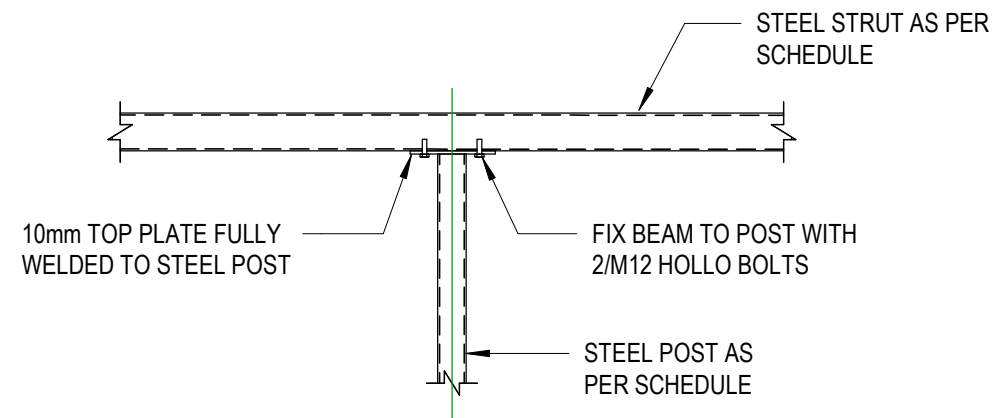

TYPICAL POST TO BEAM CONNECTION

SCALE : 1 : 20

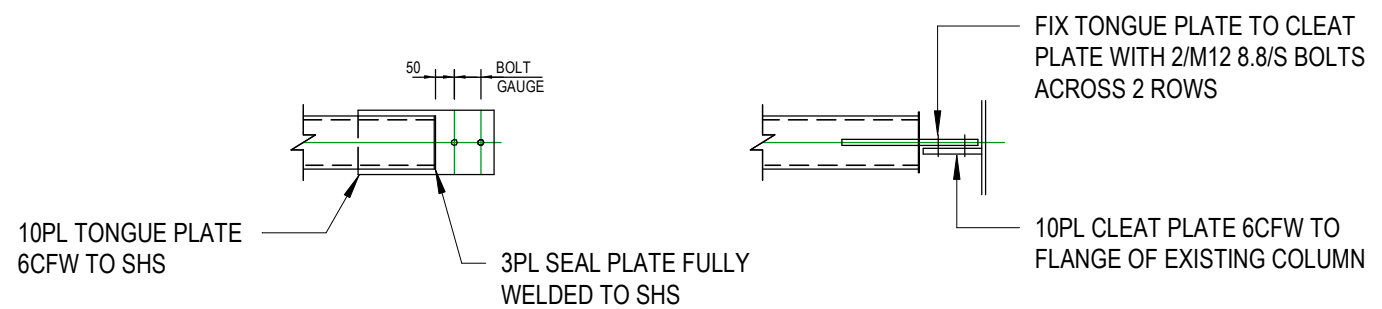

PLAN

SECTION

TYPICAL SHS STRUT CONNECTION

SCALE : 1 : 20

FIX BASE PLATE TO SLAB WITH 2/M12 4.6/S BOLTS. USE CHEMSET REO502.

PROVIDE HIGH STRENGTH NON-SHRINK GROUT UNDER BASE PLATE

STEEL POST AS PER SCHEDULE


10mm BASE PLATE FULLY WELDED TO STEEL POST

SLAB AS SPECIFIED

CHEMSET REO502
SIZE: M12
EDGE DISTANCE: 165mm
ANCHOR SPACING: 330mm
EMBEDMENT: 120mm min.

TYPICAL POST TO SLAB CONNECTION

SCALE : 1 : 20

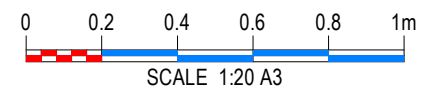

PLAN DETAILS:

Designed: JT
Drawn: JT
Checked: PB
Datum: 20/12/2021
Date: 11:42:26 AM

PLAN AMENDMENTS:

Rev	Date	Comment	Altered	Checked
B	20.12.2021	FOR TENDER	JT	PB

PROPOSED SHED REFURBISHMENT 48 SIPPY CREEK RD, TANAWHA SUNSHINE COAST REGIONAL COUNCIL

© This plan is Copyright. Other than for the purposes of and subject to the conditions prescribed under the Copyright Act, no part of it may in any form or by any means be reproduced, stored in a retrieval system or transmitted without the prior written permission of Contour Consulting Engineers. The plan shall not be used for construction without prior written approval.

PLAN TITLE:

DETAILED SECTIONS - SHEET 2

PLAN No: 1417 03 331

FOR TENDER

REVISION: B