



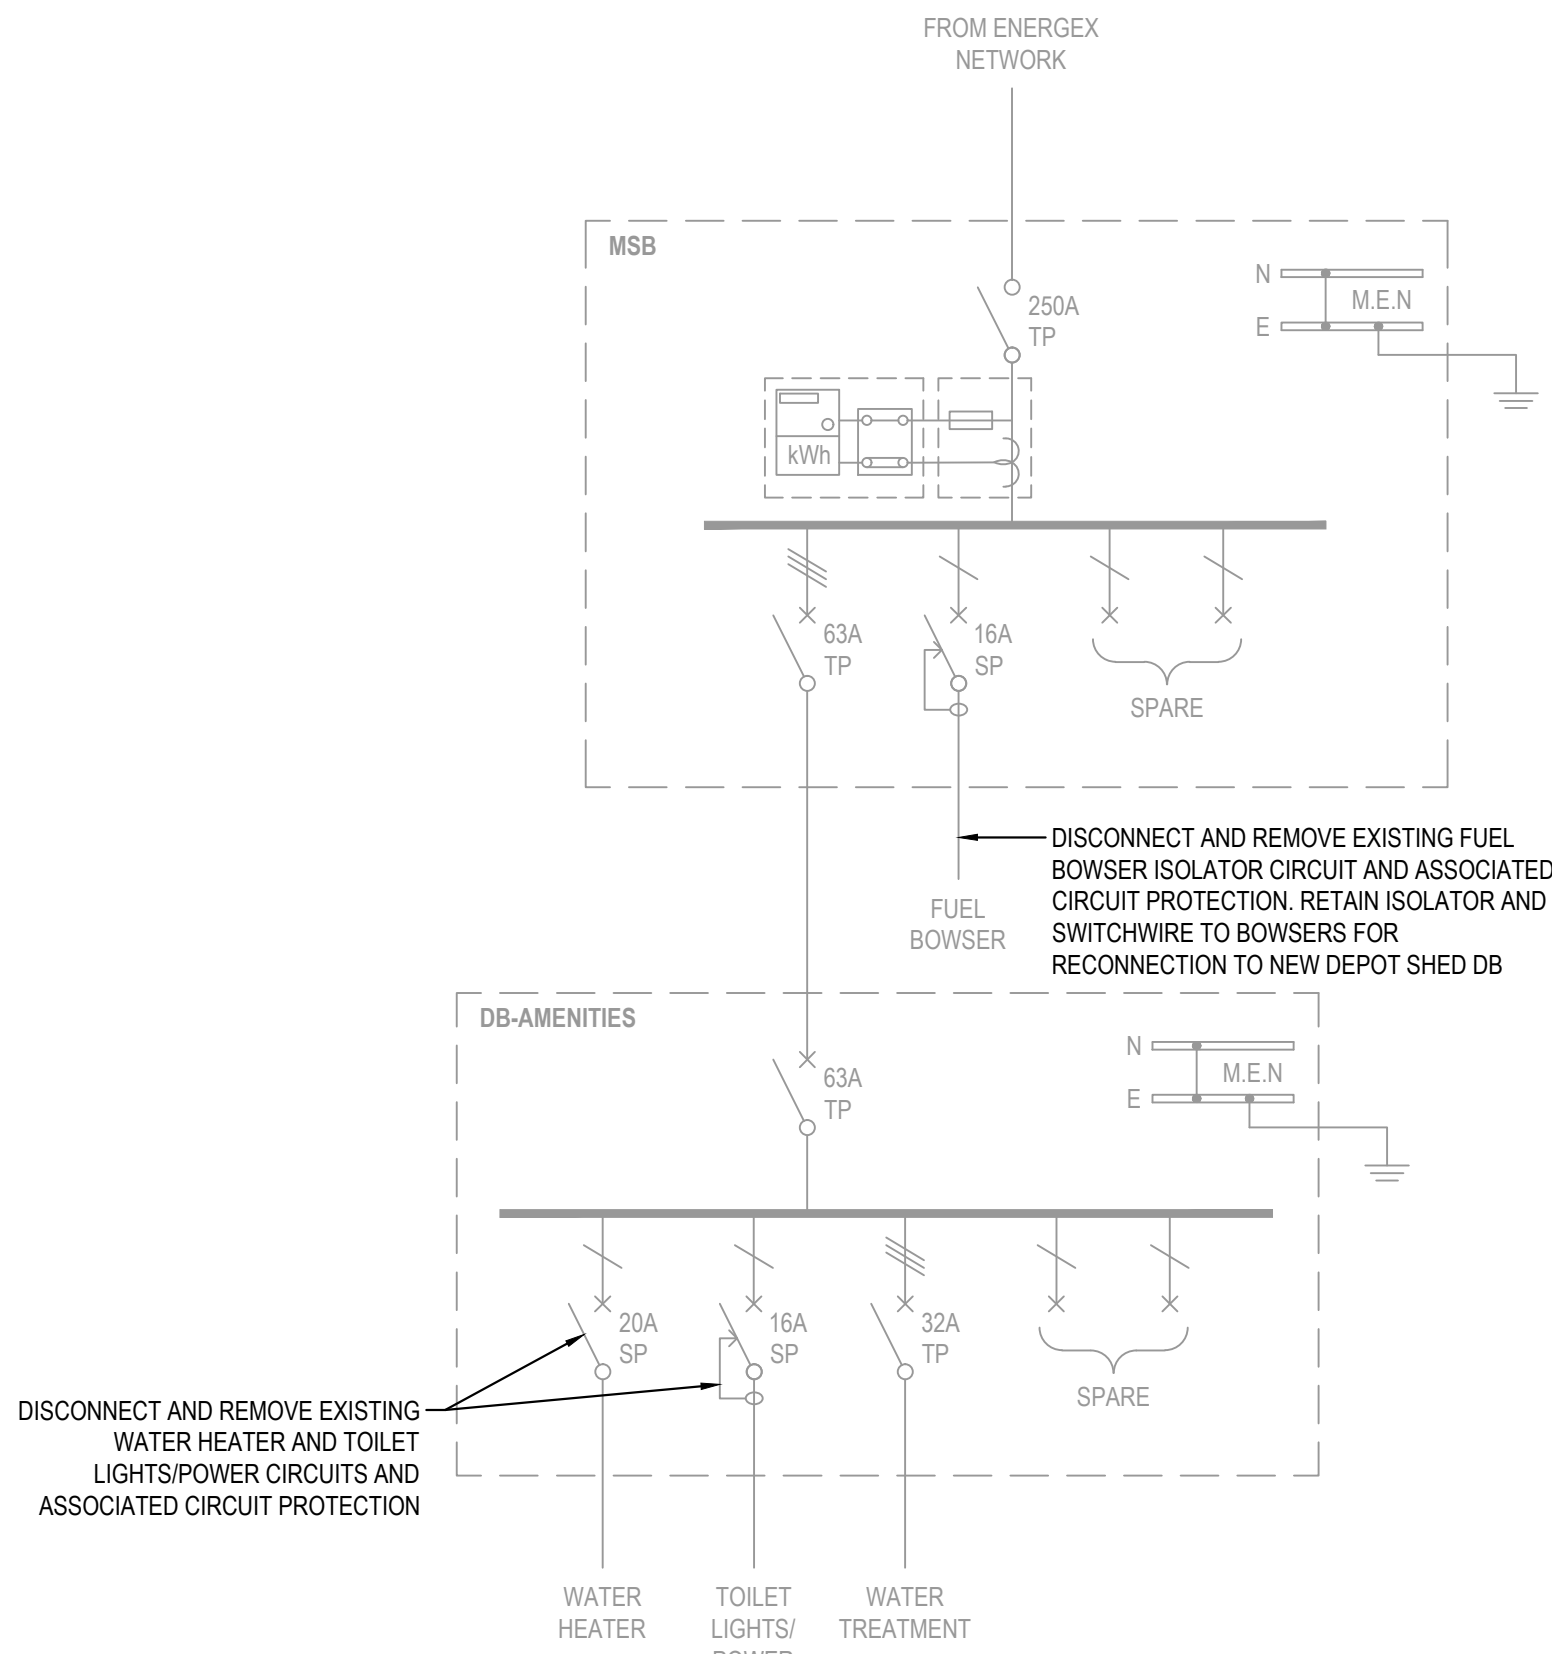


EXISTING SINGLE LINE DIAGRAM

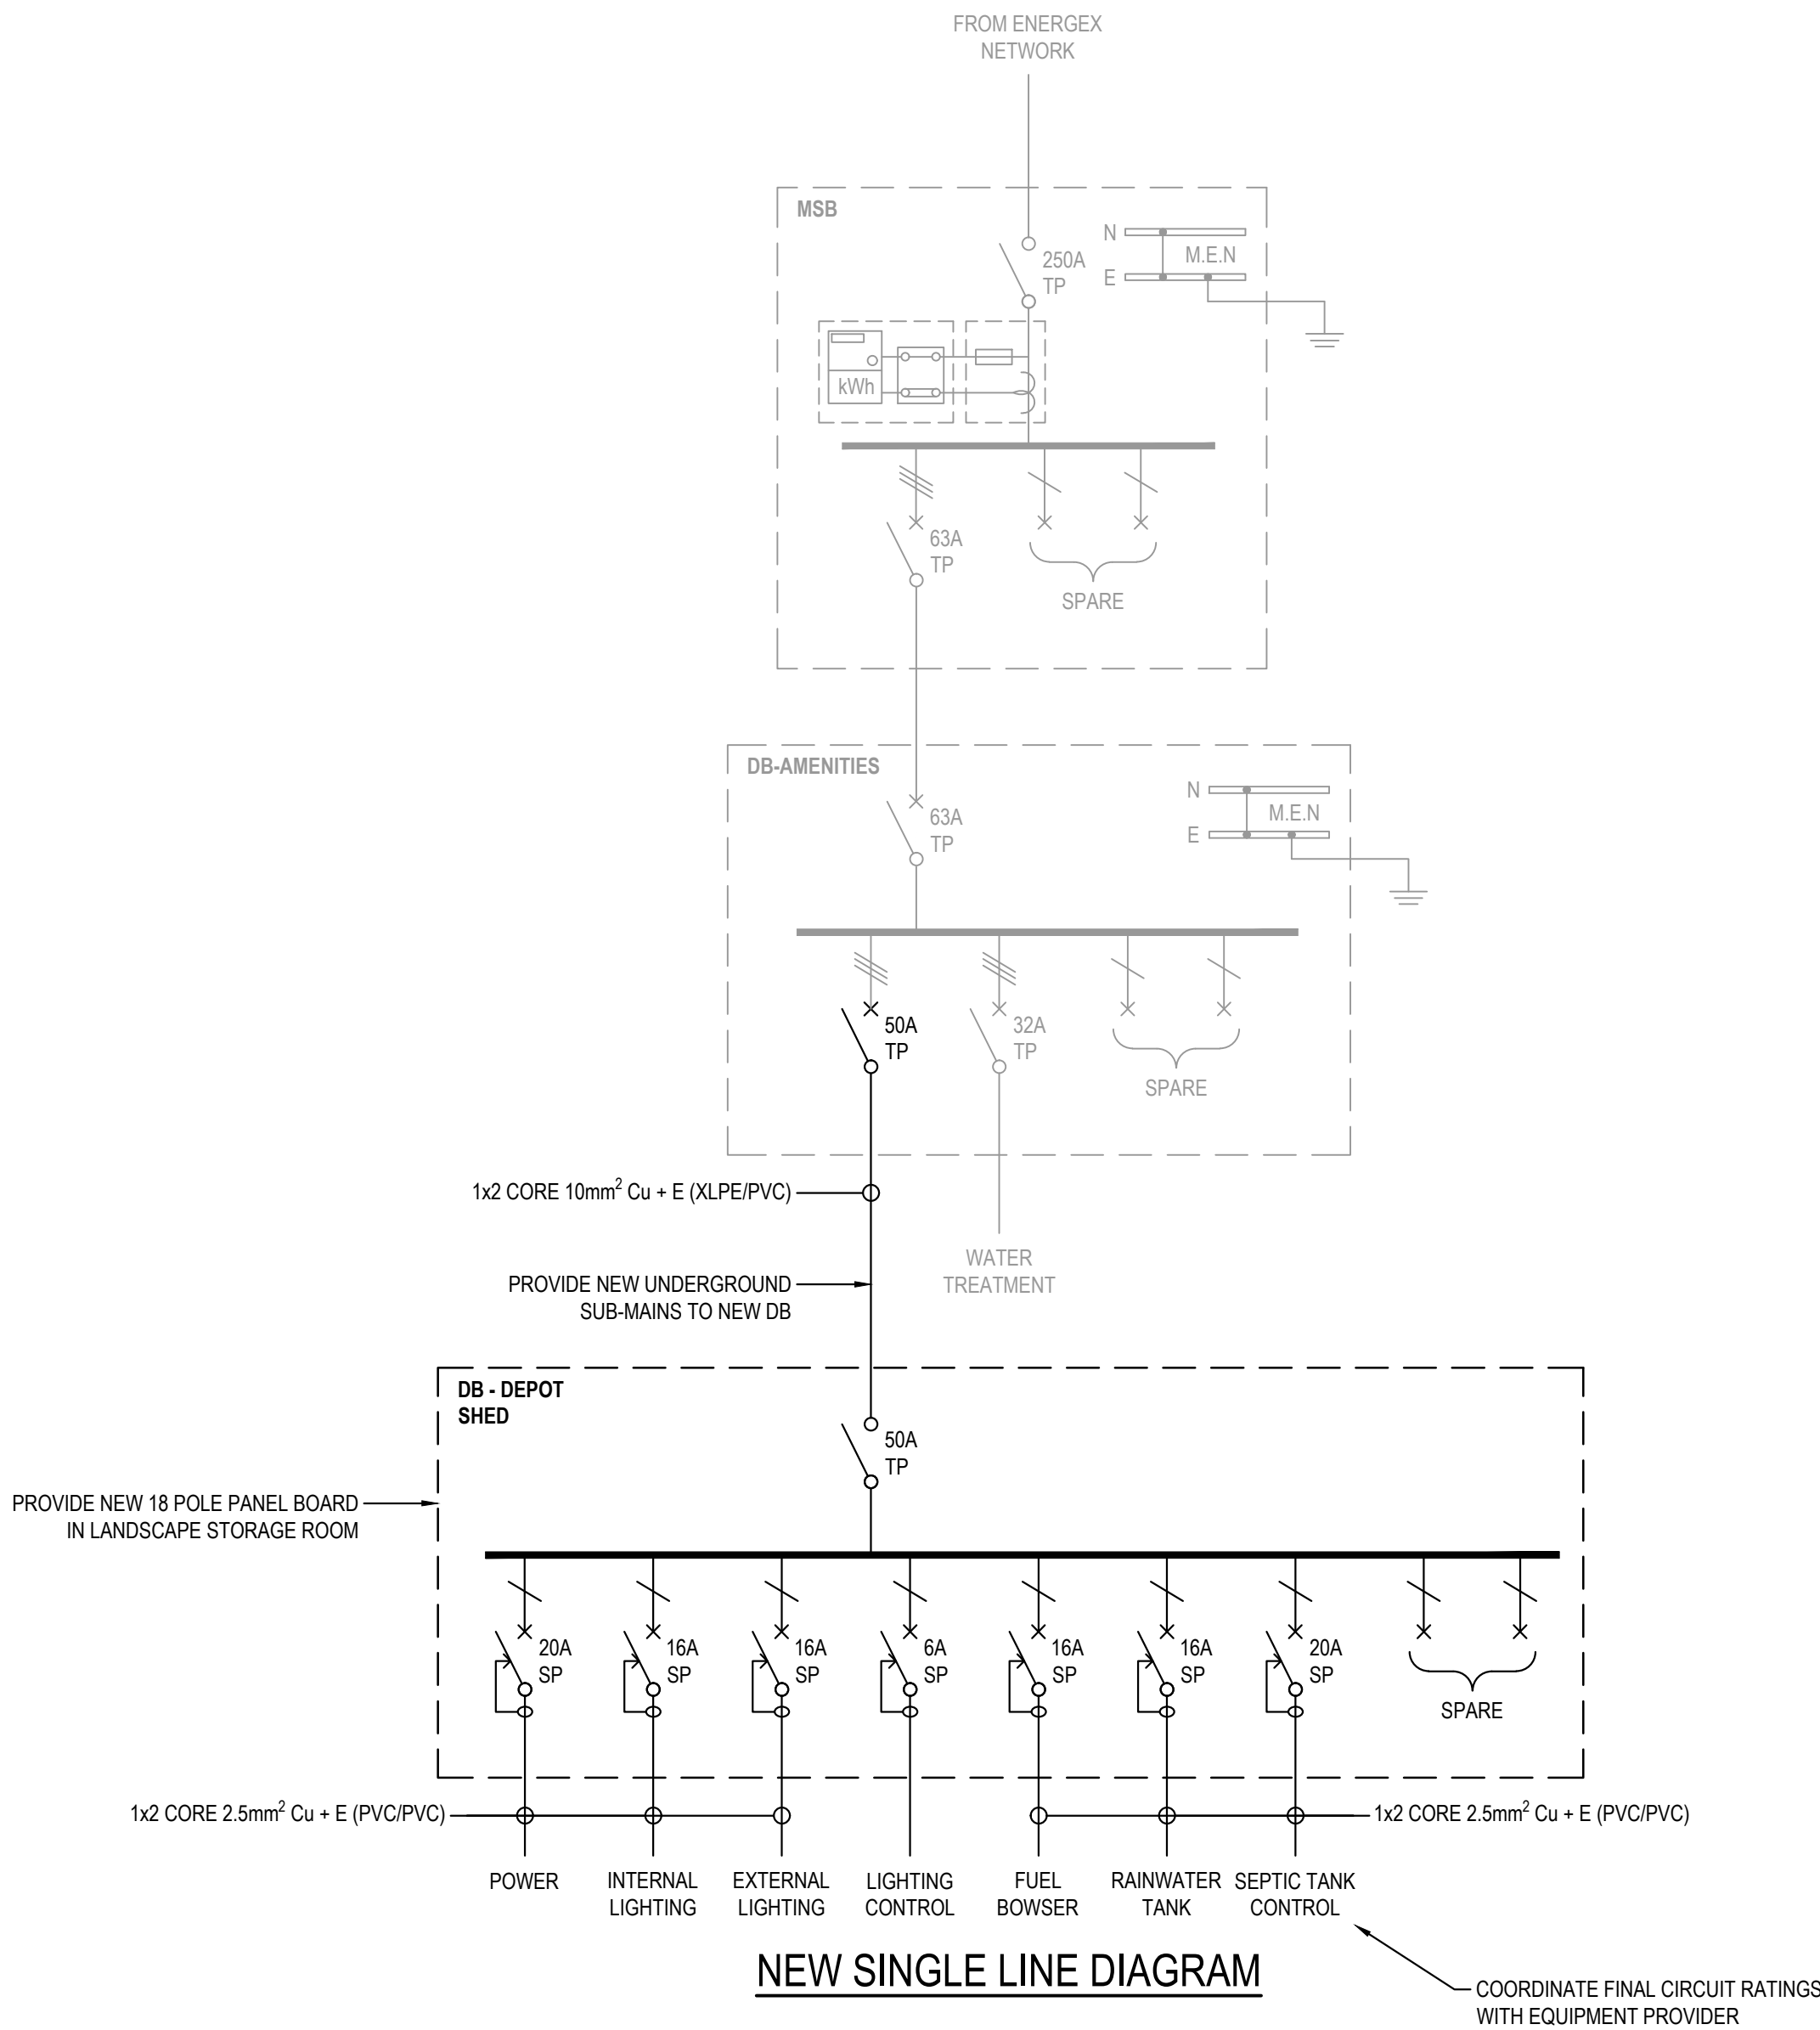

NEW SINGLE LINE DIAGRAM

COORDINATE FINAL CIRCUIT RATINGS WITH EQUIPMENT PROVIDER

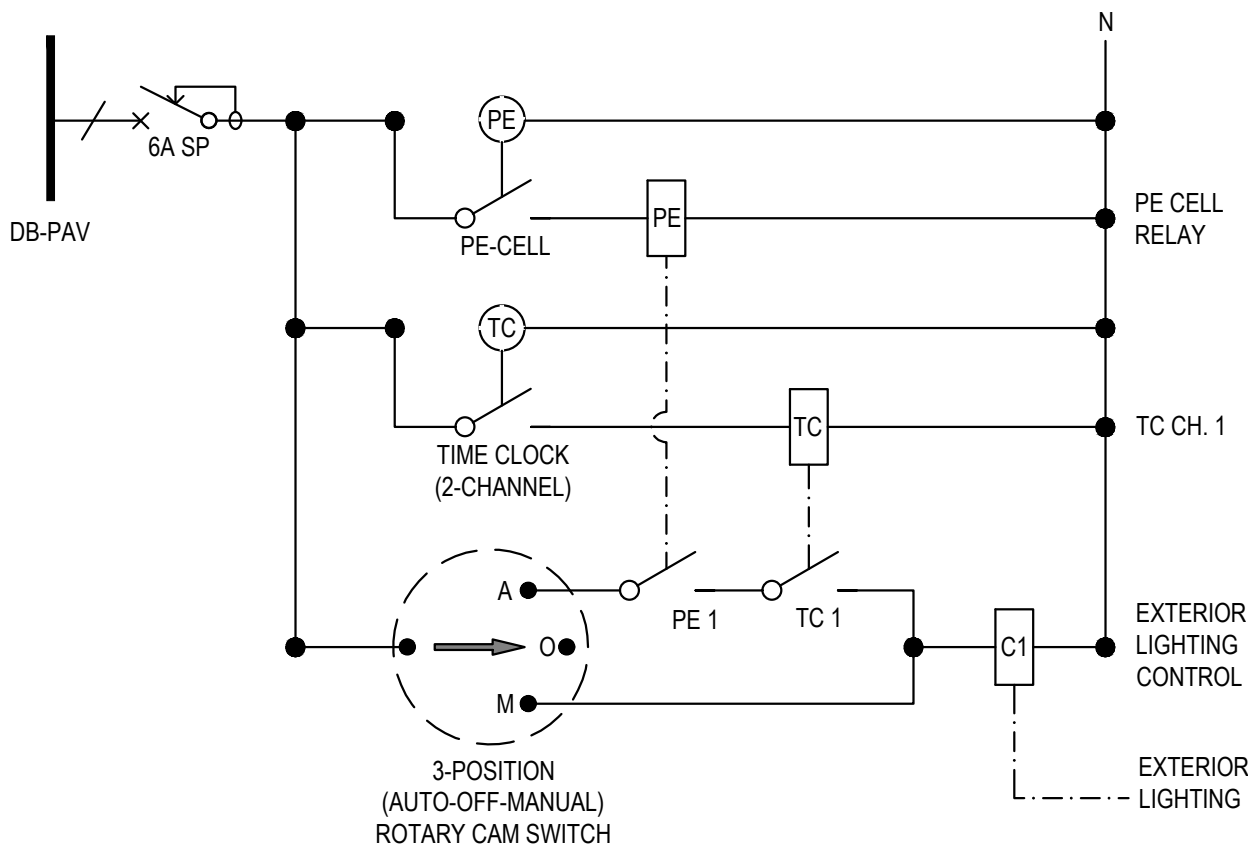

EXTERIOR LIGHTING CONTROL SCHEMATIC

PROVIDE LABELLING TO ROTARY SWITCH: "EXTERIOR LIGHTING". CONFIGURE TIME-CLOCK & PE SETTINGS DURING COMMISSIONING.

A1

2	12.01.22	TENDER ISSUE	C.L	C.L	
1	01.12.21	PRELIMINARY ISSUE	C.L	C.L	
Rv	DATE	REVISIONS	REC.	APPR.	

SURVEYED	
DRAWN	B.GRANT
CHECKED	C.LITTLETON
REVIEWED	C.LITTLETON
COORDINATOR	C.LITTLETON

WEBB AUSTRALIA

CONSULTING ELECTRICAL ENGINEERS - MECHANICAL CONSULTANTS
LIGHTING CONSULTANTS - TECHNOLOGY CONSULTANTS - COMMUNICATIONS CONSULTANTS
COPYRIGHT © 2015 WEBB AUSTRALIA GROUP (AUST PTY LTD) AND ITS SUBSIDIARIES. ALL RIGHTS RESERVED. THIS DRAWING MAY NOT BE REPRODUCED OR TRANSMITTED IN ANY FORM OR BY ANY MEANS, IN PART OR IN WHOLE WITHOUT THE WRITTEN PERMISSION OF WEBB AUSTRALIA GROUP (AUST PTY LTD). WEBB DRAWINGS AND SCHEMATICS SHALL BE READ IN CONJUNCTION WITH ALL CONTRACT DOCUMENTATION. SHOULD ANY AMBIGUITY, ERROR, OMISSION, DISCREPANCY, INCONSISTENCY OR OTHER FAULT APPEAR TO EXIST IN THE DOCUMENT, IMMEDIATELY NOTIFY THE CONTRACT ADMINISTRATOR IN WRITING.

WEBB AUSTRALIA GROUP - ACN 010 733 561
CAPITAL ONE COMPLEX, SUITE 13A
9 CAPITAL PLACE BIRRTINYA QLD 4571
TELEPHONE: (07) 5438 9800
FACSIMILE: (07) 3870 4100
EMAIL: sunshinecoast@webbaustralia.com.au
Q403A



Sunshine Coast
COUNCIL

SIPPY DOWNS DEPOT SHED REFURBISHMENT		Project Number:
ELECTRICAL SERVICES		Q403A
DETAILS & SCHEMATICS		Sheet No. - Revision No.
		E003 2