


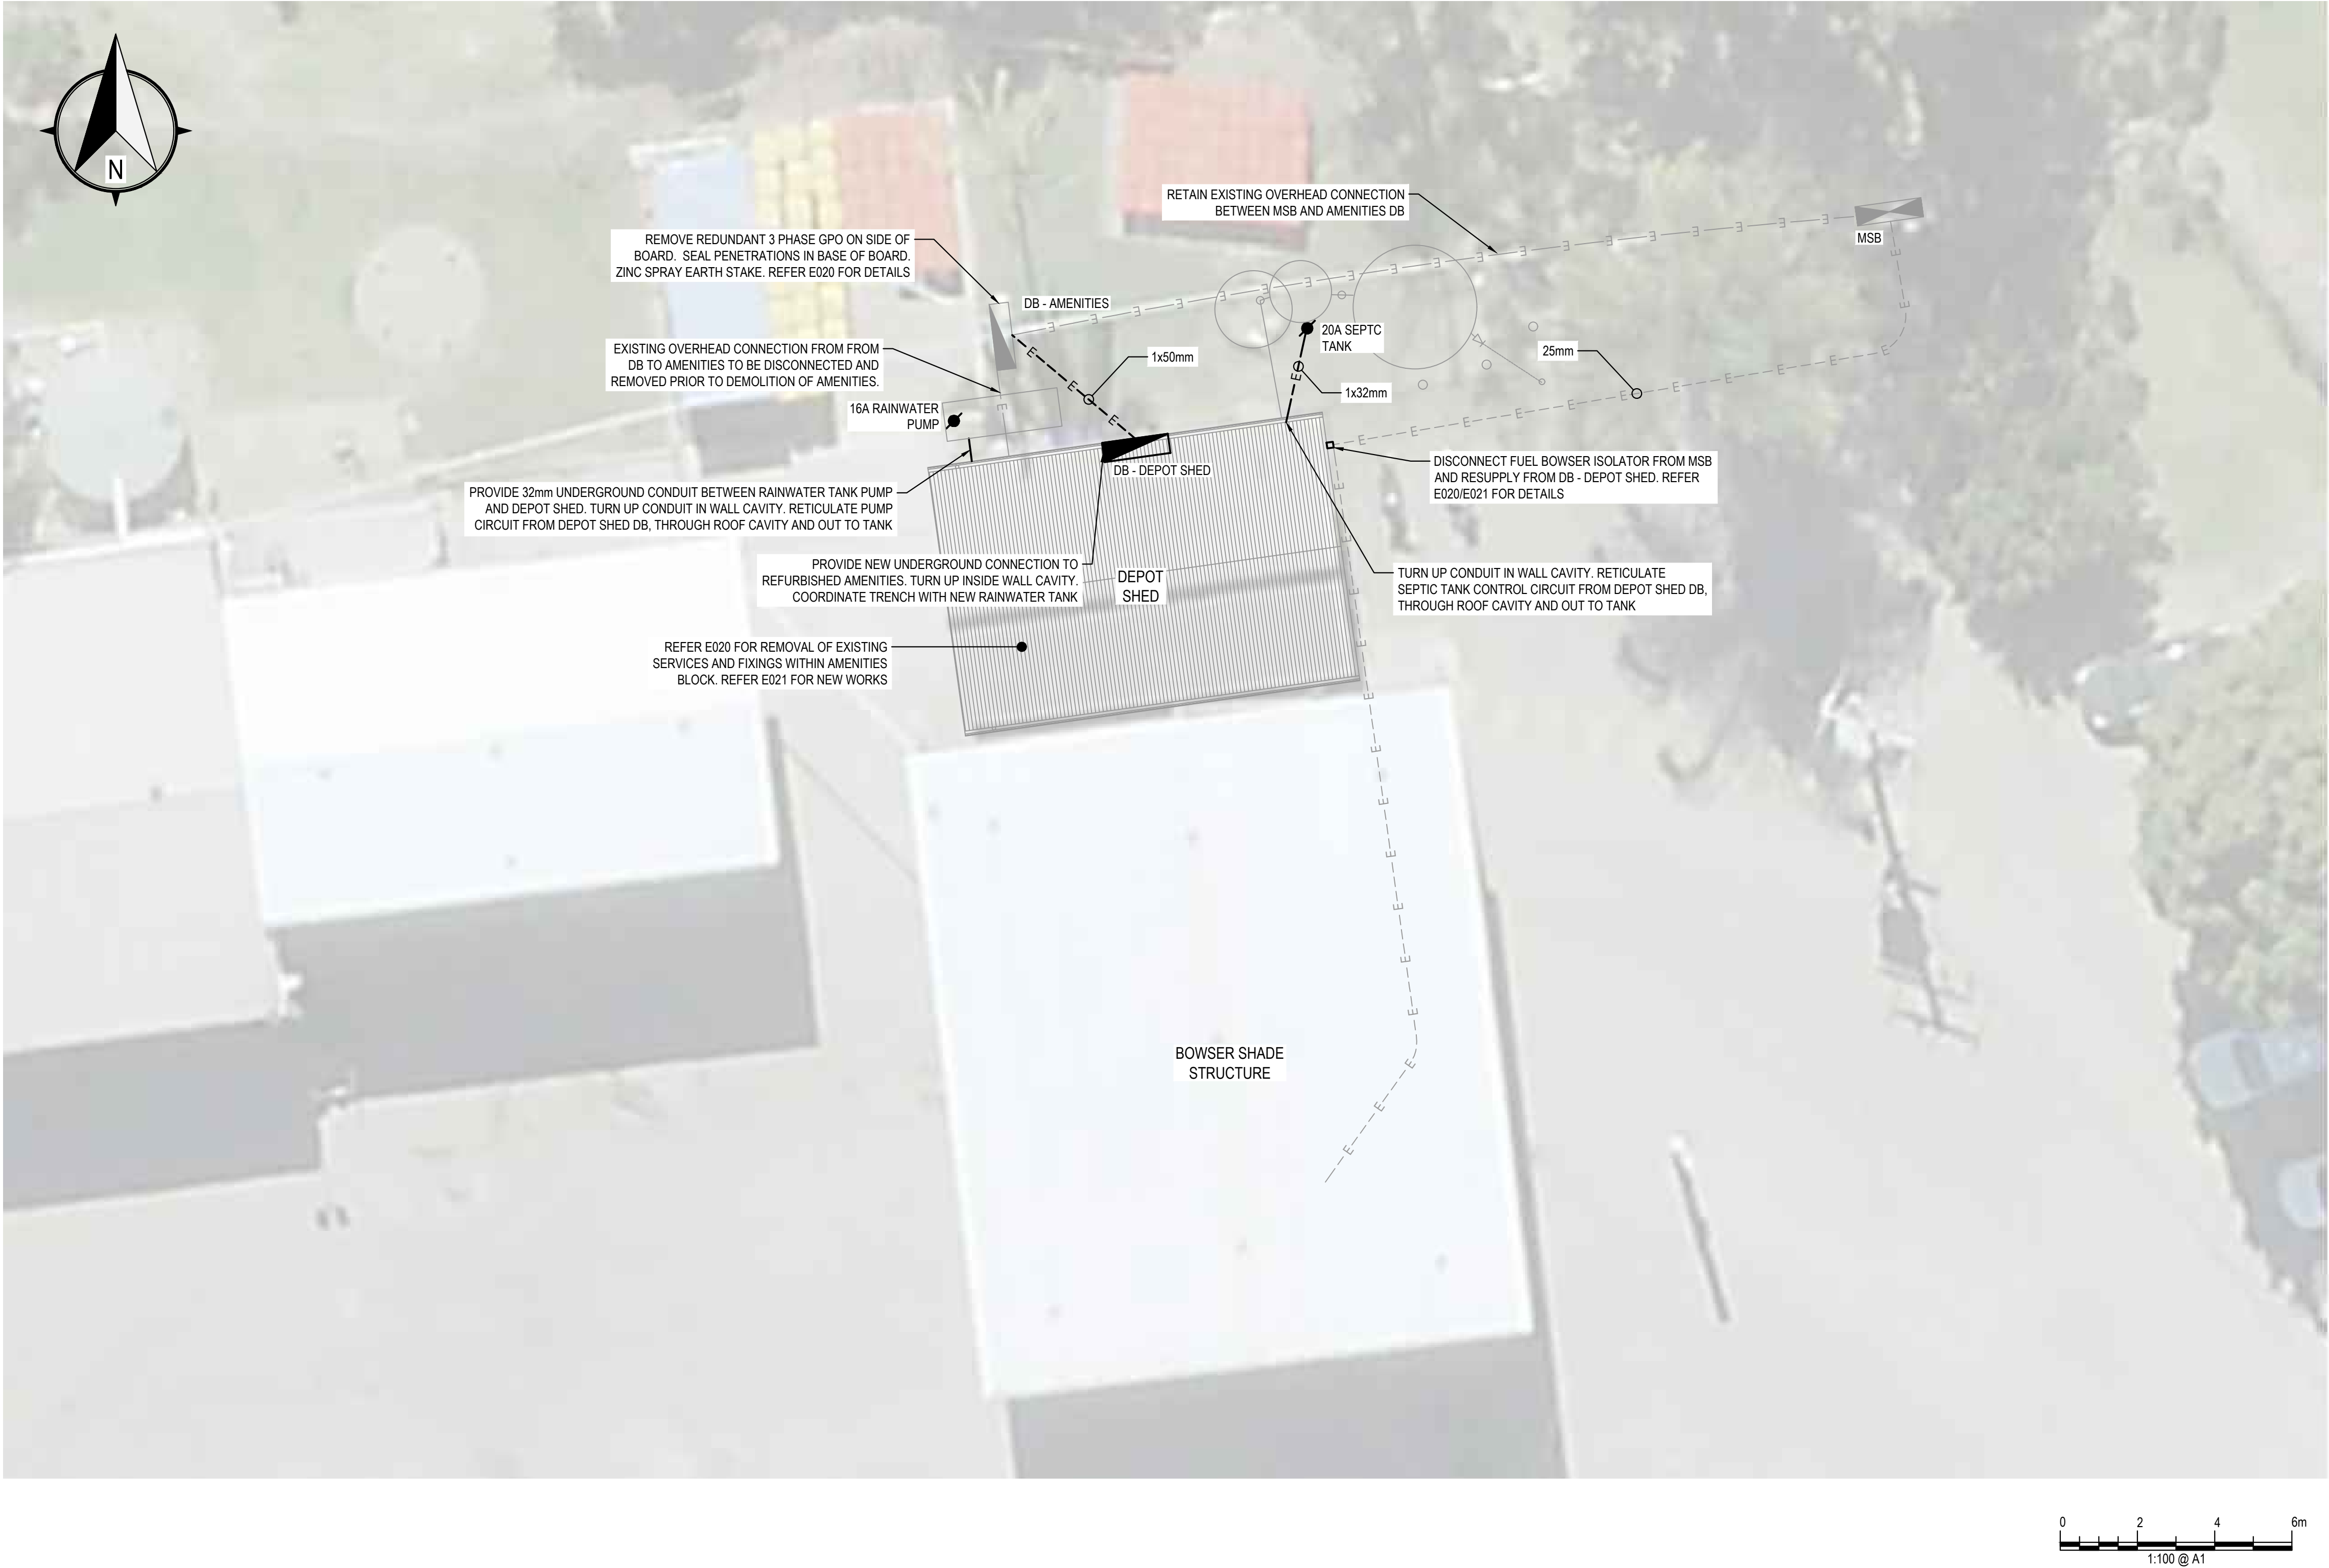

A1

2	12.01.22	TENDER ISSUE		C.L	C.L
1	01.12.21	PRELIMINARY ISSUE		C.L	C.L
Rv	DATE	REVISIONS		REC.	APPR.

SURVEYED	
DRAWN	B.GRANT
CHECKED	C.LITTLETON
REVIEWED	C.LITTLETON
COORDINATOR	C.LITTLETON

WEBB AUSTRALIA

CONSULTING ELECTRICAL ENGINEERS - MECHANICAL CONSULTANTS

WEBB AUSTRALIA GROUP - ACN 010 733 561
CAPITAL ONE COMPLEX, SUITE 13A
9 CAPITAL PLACE BIRTINGA QLD 4571
TELEPHONE: (07) 5438 9800
FACSIMILE: (07) 3870 4100
EMAIL: sunshinecoast@webbaustralia.com.au
Q403A

WEBB AUSTRALIA GROUP - ACN 010 733 561
CAPITAL ONE COMPLEX, SUITE 13A
9 CAPITAL PLACE BIRTINGA QLD 4571
TELEPHONE: (07) 5438 9800
FACSIMILE: (07) 3870 4100
EMAIL: sunshinecoast@webbaustralia.com.au
Q403A

CONSULTING ELECTRICAL ENGINEERS - MECHANICAL CONSULTANTS
LIGHTING CONSULTANTS - TECHNOLOGY CONSULTANTS - COMMUNICATIONS CONSULTANTS
COPYRIGHT © 2015 WEBB AUSTRALIA GROUP (AUST PTY LTD) AND ITS SUBSIDIARIES. ALL RIGHTS RESERVED. THIS
DRAWING MAY NOT BE REPRODUCED OR TRANSMITTED IN ANY FORM OR BY ANY MEANS IN PART OR IN
WHOLE WITHOUT THE WRITTEN PERMISSION OF WEBB AUSTRALIA GROUP (AUST PTY LTD). WEBB DRAWINGS
AND SPECIFICATIONS SHALL BE READ IN CONJUNCTION WITH ALL CONTRACT DOCUMENTS AND SHALL
ANY AMBIGUITY, ERROR, OMISSION, DISCREPANCY, INCONSISTENCY OR OTHER FAULT APPEAR TO EXIST IN
THE DOCUMENTS, AMBIGUITY SHALL BE THE CONTRACT ADMINISTRATOR'S RESPONSIBILITY.

Sunshine Coast

COUNCIL

SIPPY DOWNS DEPOT SHED REFURBISHMENT
ELECTRICAL SERVICES
SITE PLAN

Project Number:
Q403A

Sheet No. - Revision No.
E010 2