




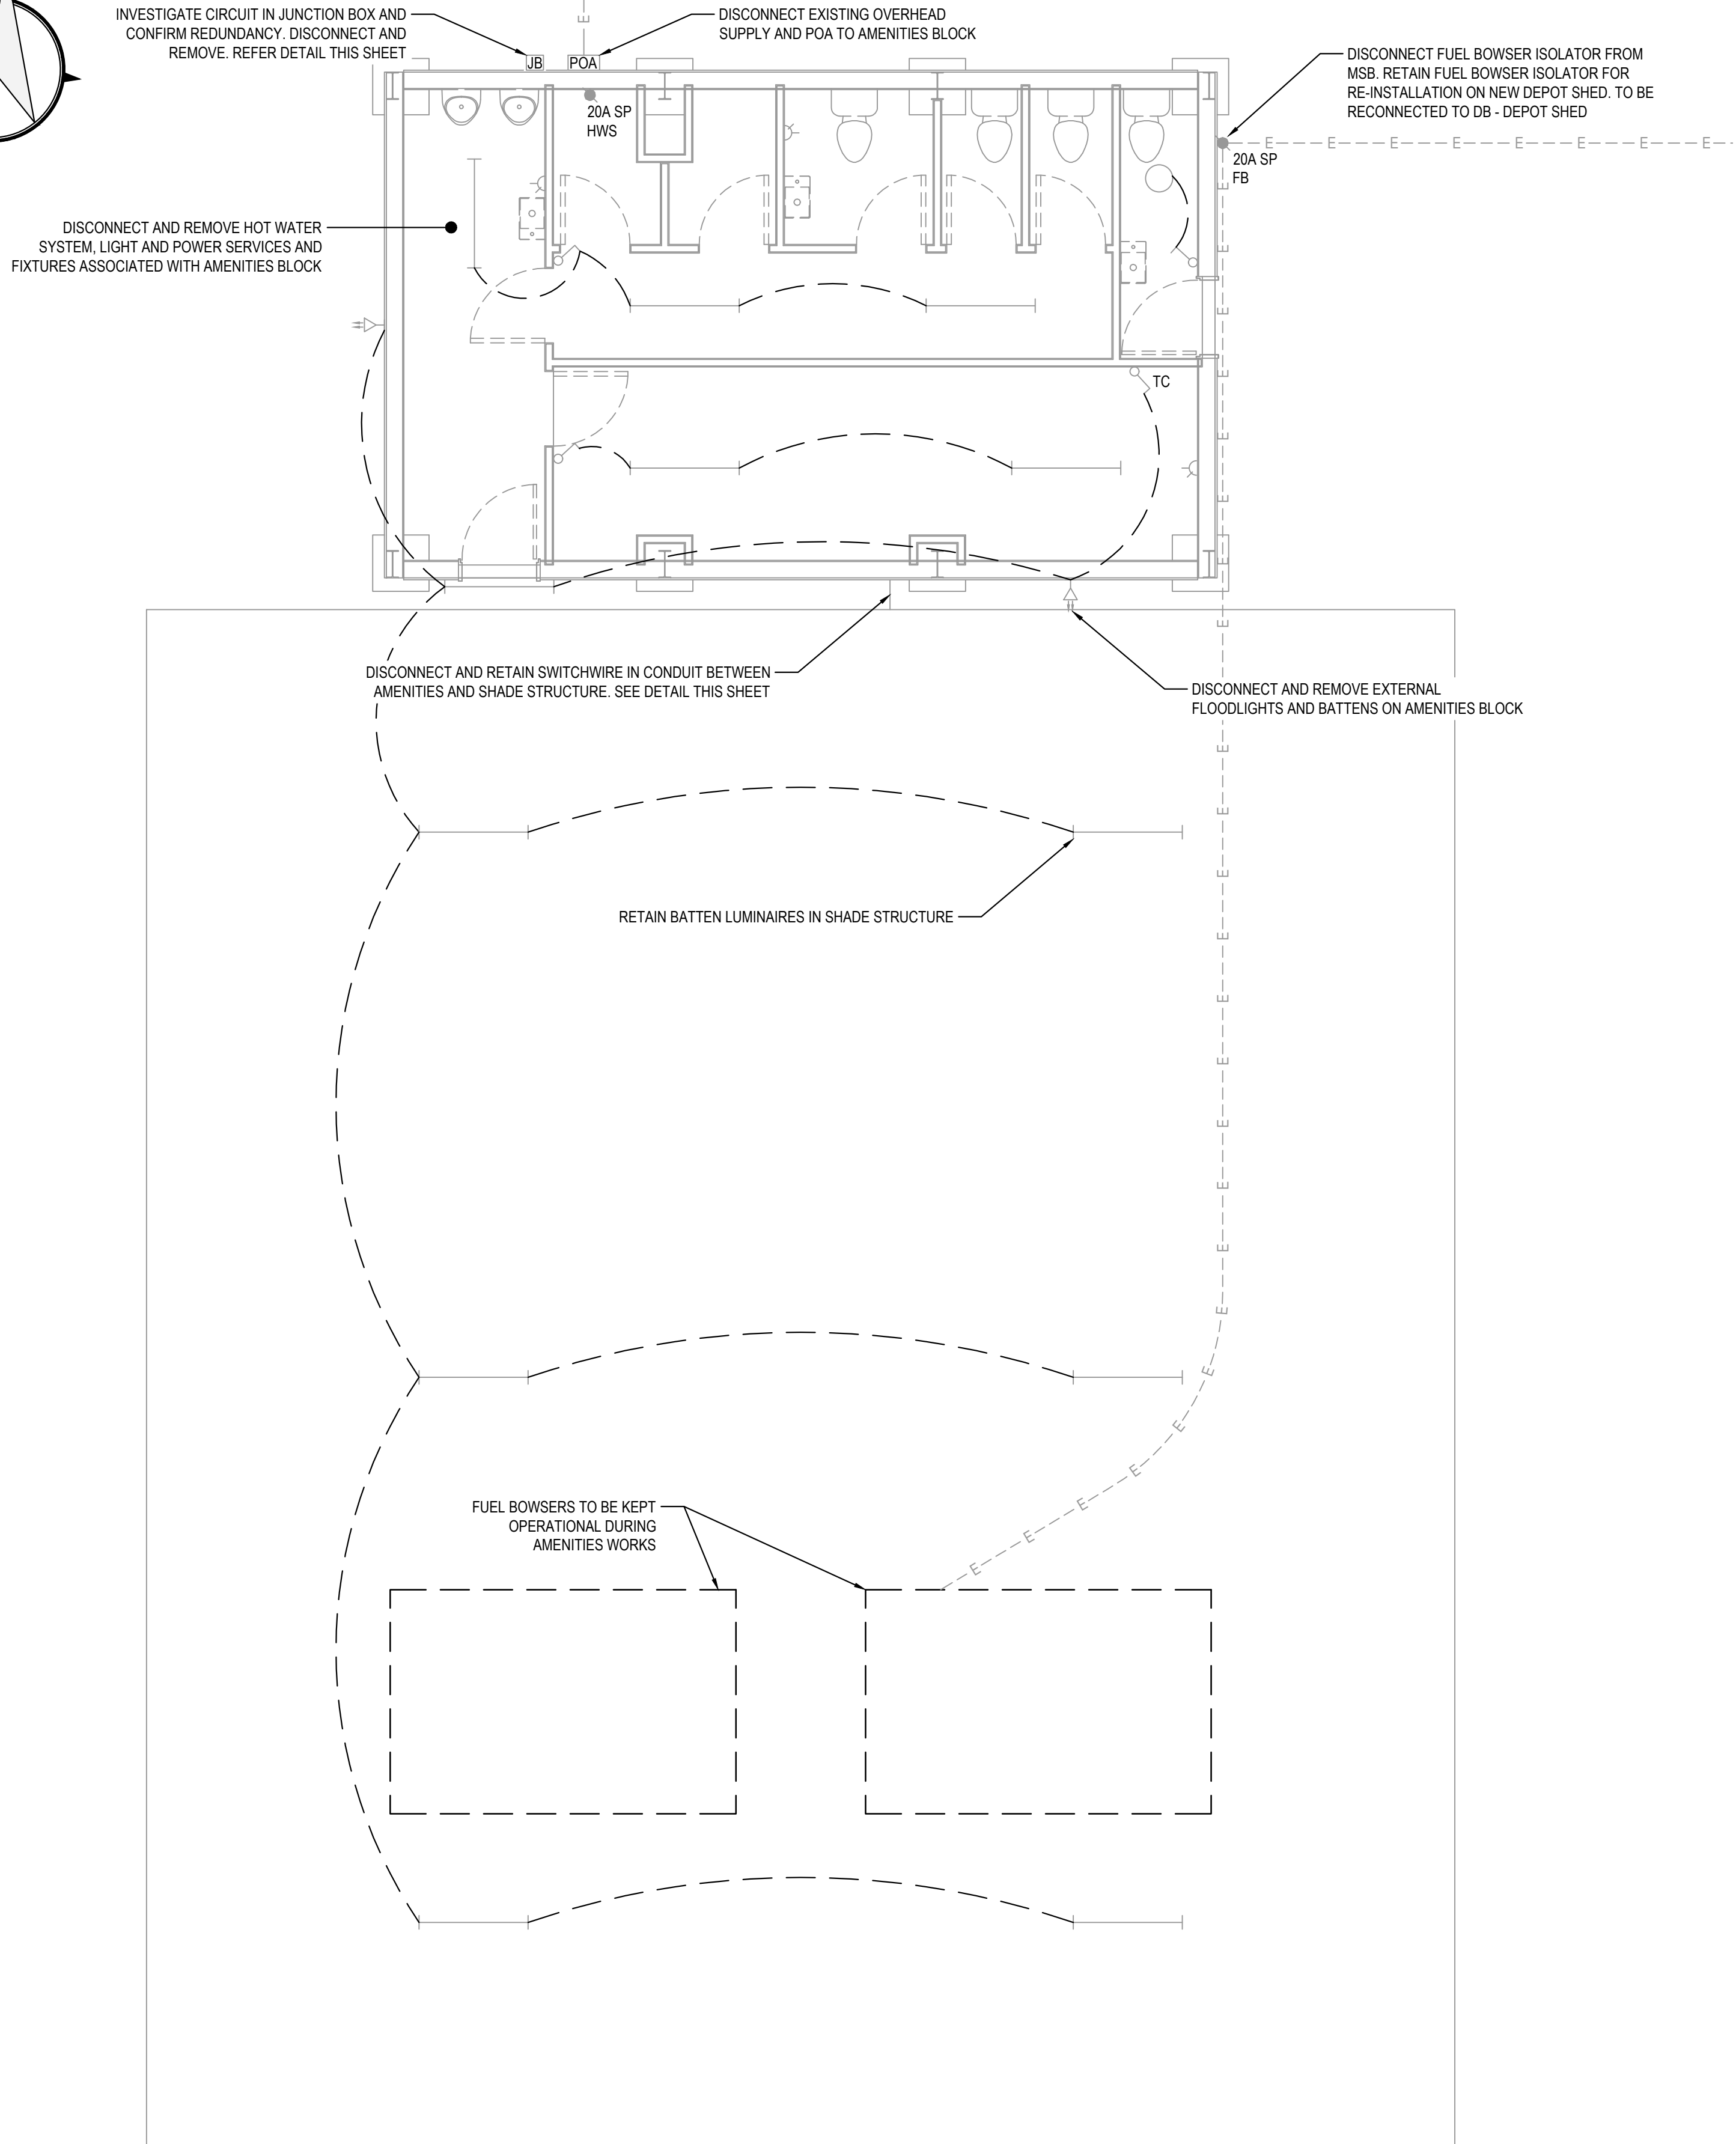

DEMOLITION PLAN
1:50

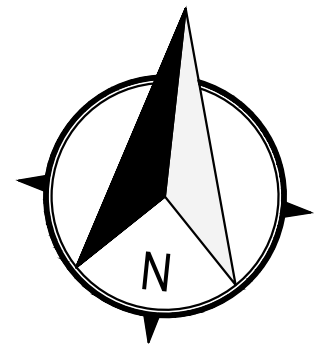

SHADE STRUCTURE SWITCHWIRE DETAIL
1:50

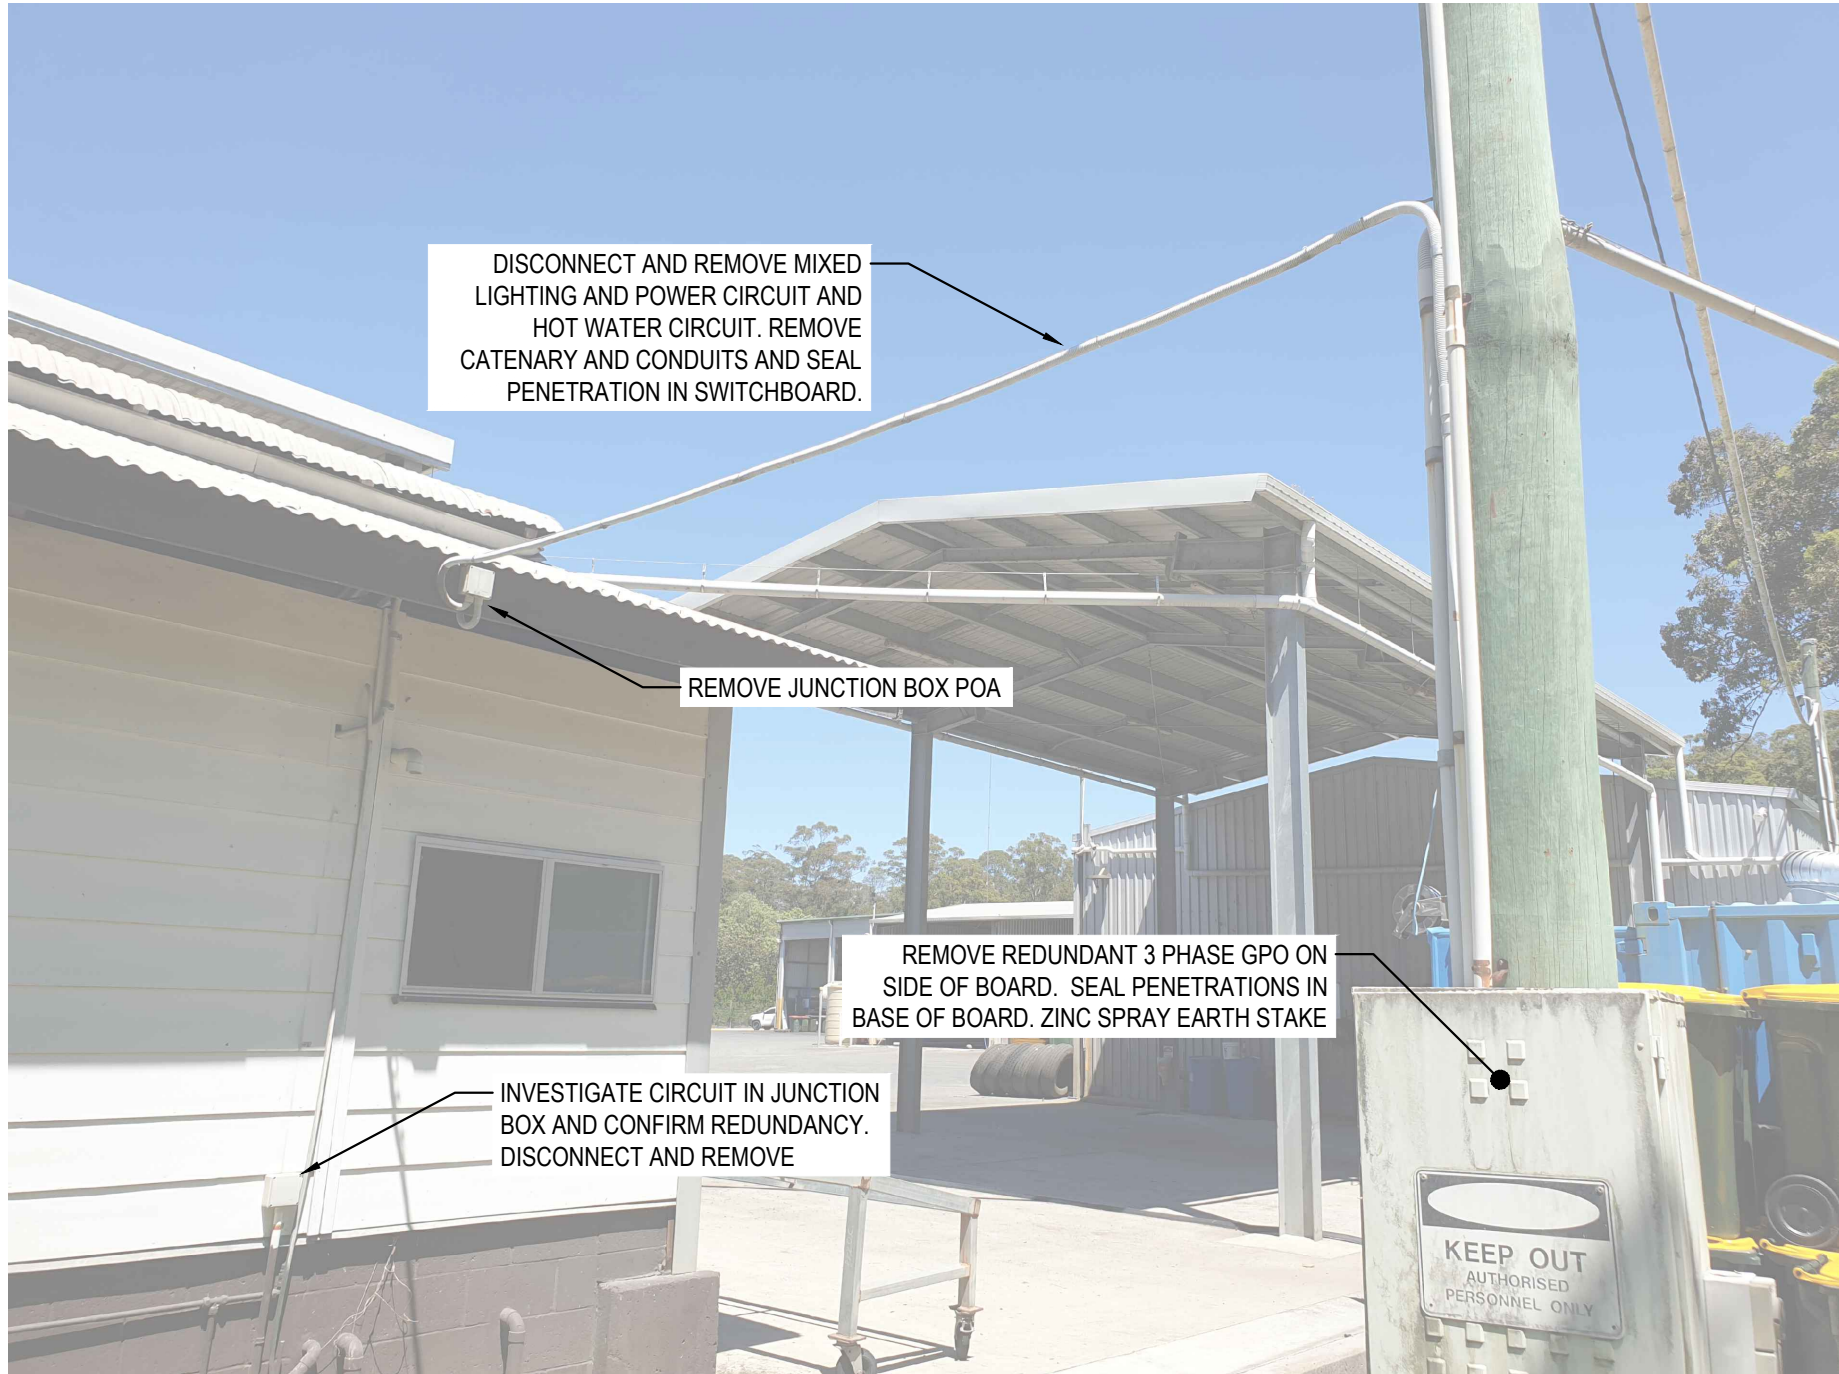

OVERHEAD ATTACHEMENT DETAIL
1:50

A1

2	12.01.22	TENDER ISSUE	C.L.	C.L.	
1	01.12.21	PRELIMINARY ISSUE	C.L.	C.L.	
Rv	DATE	REVISIONS	REC.	APPR.	

SURVEYED	
DRAWN	B.GRANT
CHECKED	C.LITTLETON
REVIEWED	C.LITTLETON
COORDINATOR	C.LITTLETON

WEBB AUSTRALIA

CONSULTING ELECTRICAL ENGINEERS - MECHANICAL CONSULTANTS
LIGHTING CONSULTANTS - TECHNOLOGY CONSULTANTS - COMMUNICATIONS CONSULTANTS
COPYRIGHT © 2021 WEBB AUSTRALIA GROUP (AUST PTY LTD AND ITS SUBSIDIARIES). ALL RIGHTS RESERVED. THIS DOCUMENT MAY NOT BE REPRODUCED OR TRANSMITTED IN ANY FORM OR BY ANY MEANS, IN PART OR IN WHOLE WITHOUT THE WRITTEN PERMISSION OF WEBB AUSTRALIA GROUP (AUST PTY LTD). WEBB AUSTRALIA GROUP (AUST PTY LTD) SHALL BE RESPONSIBLE FOR THE ACCURACY AND COMPLETENESS OF THE INFORMATION CONTAINED HEREIN. ANY AMBIGUITY, ERROR, OMISSION, DISCREPANCY, INCONSISTENCY OR OTHER FAULT APPEAR TO EXIST IN THE DOCUMENT, WHICHEVER IT OCCURS, SHALL BE THE RESPONSIBILITY OF THE CLIENT. ANY FAULT APPEAR TO EXIST IN THE DOCUMENT, WHICHEVER IT OCCURS, SHALL BE THE RESPONSIBILITY OF THE CLIENT.

WEBB AUSTRALIA GROUP - ACN 010 733 561
CAPITAL ONE COMPLEX, SUITE 13A
9 CAPITAL PLACE BIRTING QLD 4571
TELEPHONE: (07) 5438 9800
FACSIMILE: (07) 3870 4100
EMAIL: sunshinecoast@webbaustralia.com.au

Q403A



Sunshine Coast
COUNCIL

SIPPY DOWNS DEPOT SHED REFURBISHMENT
ELECTRICAL SERVICES
DEMOLITION PLAN

Project Number:
Q403A

Sheet No. - Revision No.
E020 2