



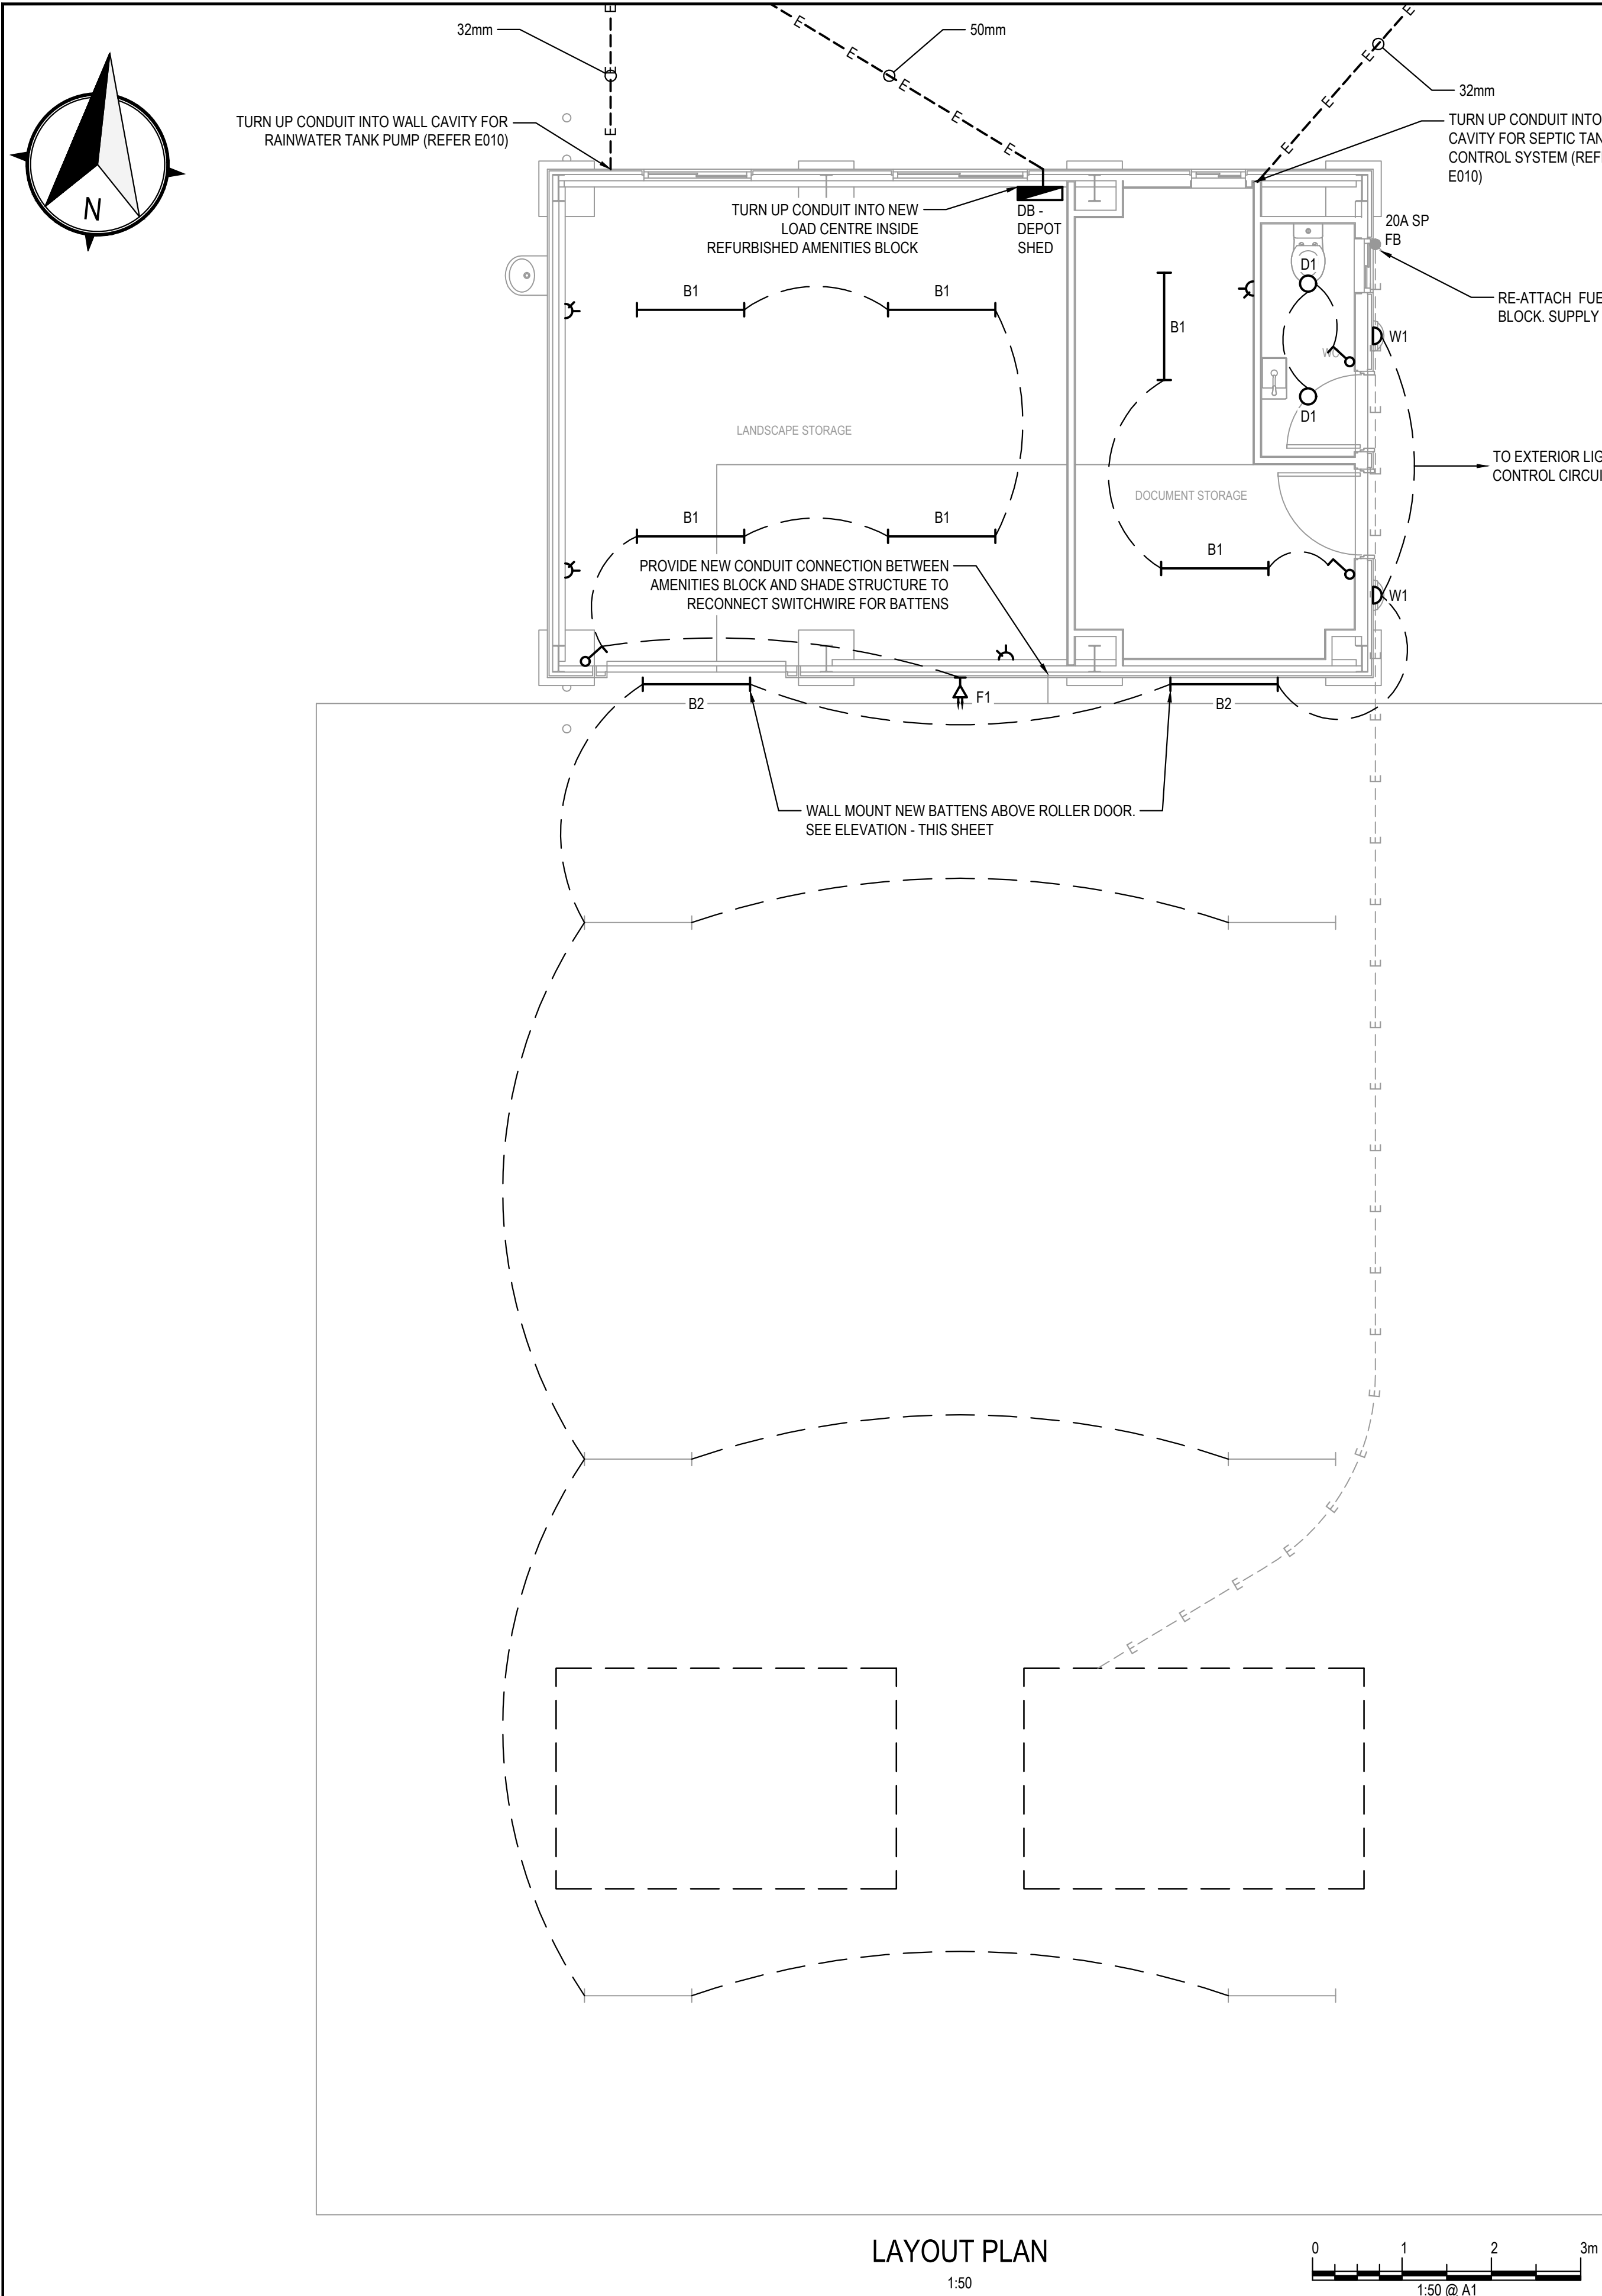

LAYOUT PLAN
1:50

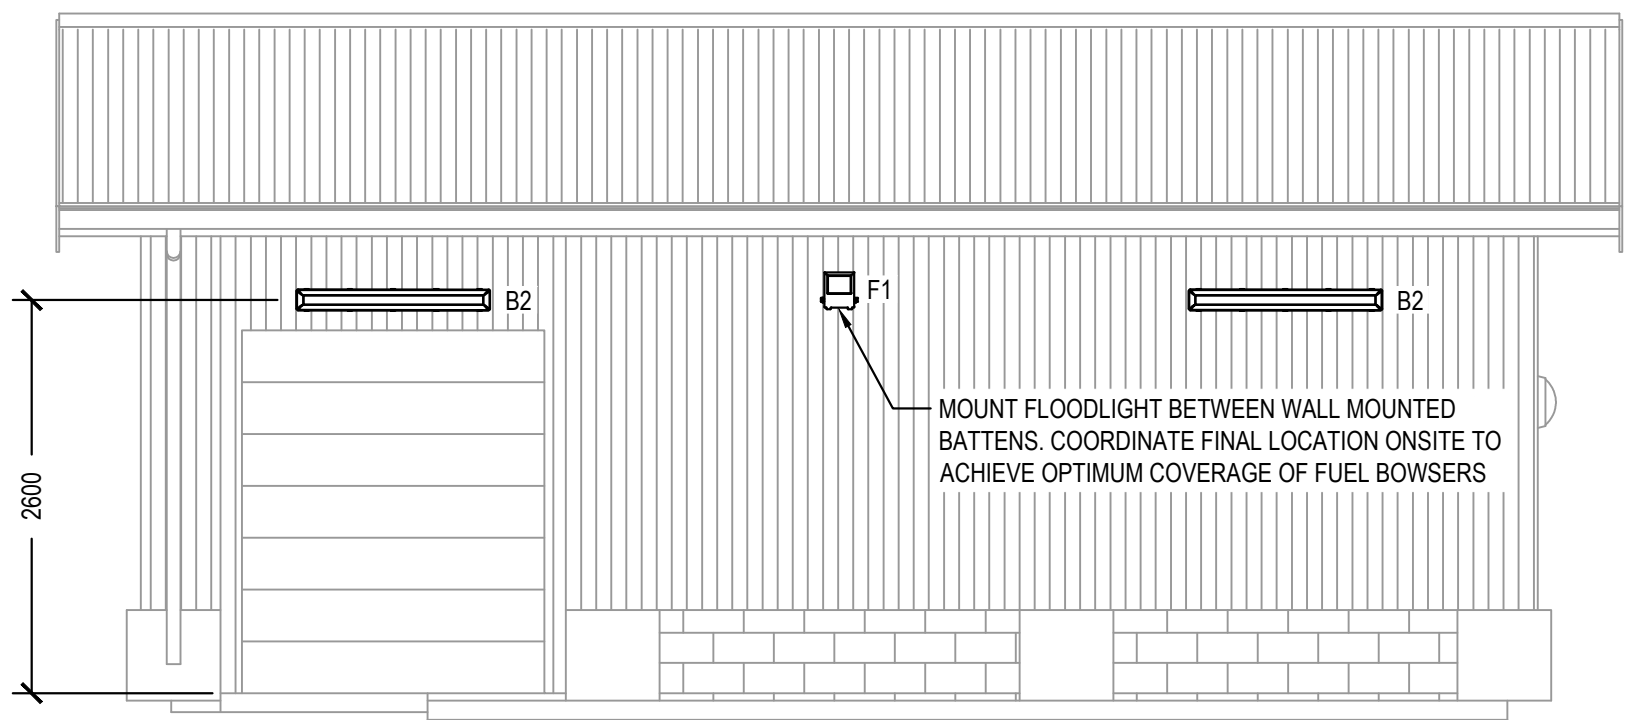

ELEVATION PLAN
1:50

A1							SURVEYED	
							DRAWN	B.GRANT
							CHECKED	C.LITTLETON
							REVIEWED	C.LITTLETON
							COORDINATOR	C.LITTLETON
2	12.01.22	TENDER ISSUE		C.L	C.L			
1	01.12.21	PRELIMINARY ISSUE		C.L	C.L			
Rv	DATE	REVISIONS		REC.	APPR.			

WEBB AUSTRALIA GROUP - ACN 010 733 561
CAPITAL ONE COMPLEX, SUITE 13A
9 CAPITAL PLACE BIRTINYA QLD 4571
TELEPHONE: (07) 5438 9800
FACSIMILE: (07) 3870 4100
EMAIL: sunshinecoast@webbaustralia.com.au
Q403A

CONSULTING ELECTRICAL ENGINEERS - MECHANICAL CONSULTANTS
LIGHTING CONSULTANTS - TECHNOLOGY CONSULTANTS - COMMUNICATIONS CONSULTANTS
COPYRIGHT © 2021 WEBB AUSTRALIA GROUP (ASU PTY LTD AND ITS SUBSIDIARIES). ALL RIGHTS RESERVED. THIS DRAWING MAY NOT BE REPRODUCED OR TRANSMITTED IN ANY FORM OR BY ANY MEANS, IN PART OR IN WHOLE WITHOUT THE WRITTEN PERMISSION OF WEBB AUSTRALIA GROUP (ASU PTY LTD). WEBB DRAWINGS AND DOCUMENTS MUST BE READ IN CONJUNCTION WITH ALL CONTRACT DOCUMENTS AND SHOULD ANY AMBIGUITY, ERROR, OMISSION, DISCREPANCY, INCONSISTENCY OR OTHER FAULT APPEAR TO EXIST IN THE DOCUMENTS, IMMEDIATELY NOTIFY THE CONTRACT ADMINISTRATOR IN WRITING.

SIPPY DOWNS DEPOT SHED REFURBISHMENT
ELECTRICAL SERVICES
LAYOUT PLAN

Project Number:
Q403A

Sheet No. - Revision No.
E021 2

FILE:G:\Q403A - SIPPY DOWNS DEPOT\01 WEBB\01 ELECTRICAL\E021.dwg DATE:12/Jun/2022 BY:bgran