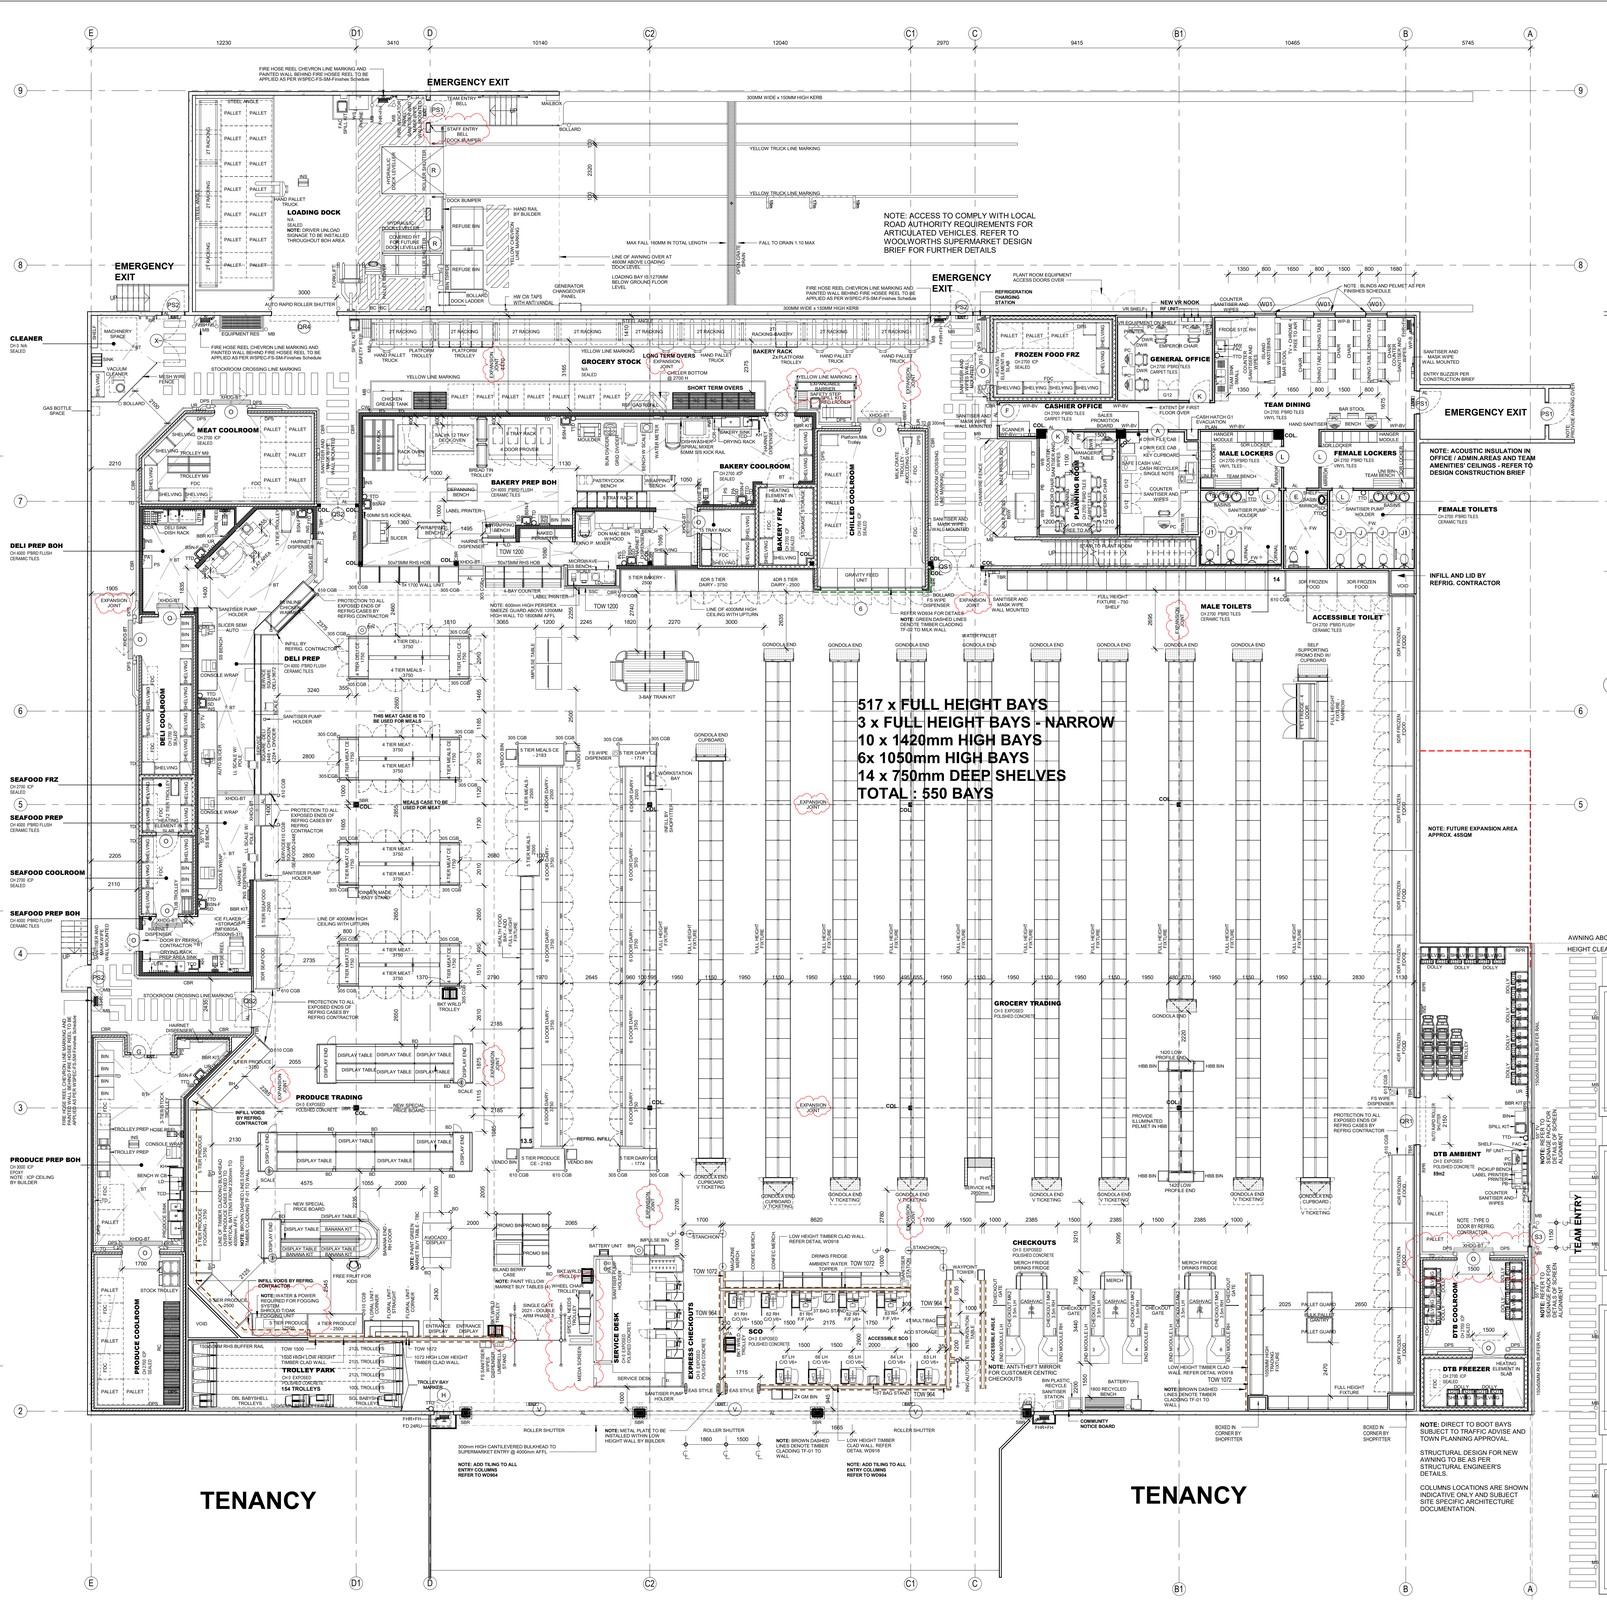

1 Control Plan - Ground Floor
1 : 100

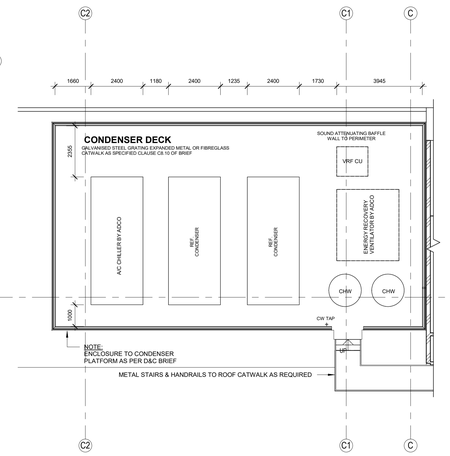

3 Control Plan - Condenser Deck
1 : 100

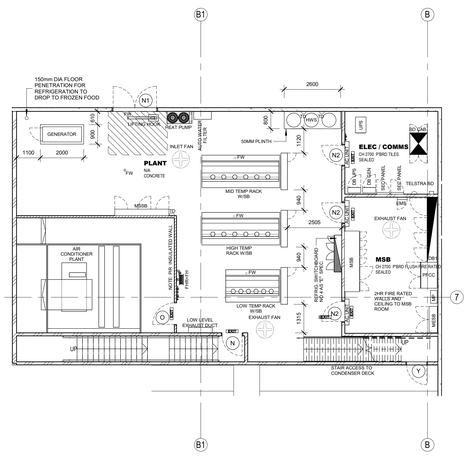

2 Control Plan - First Floor
1 : 100

eComm VOLUME SUMMARY	
DIRECT TO BOOT	DELIVERY
TARGET	$78,846 n/a
DEPARTMENT/ROOM	# OF TOTES
DTB AMBIENT	89
DTB CHILLED	47
DTB FREEZER	15
DELIVERY AMBIENT	n/a
DELIVERY CHILLED	n/a
DELIVERY FREEZER	n/a

NEW SMART BUNDLE 1.0 ITEMS:
- MONIKA
- BREAD ROLLERS
- ANTISWEEP SHELVING
- FIXED AVAILABILTY CAMERAS
- VR
- ESL
- SMART ALARM

ABBREVIATIONS

ABR	ALUMINIUM BUFFER RAIL
AFFL	ABOVE FINISHED FLOOR LEVEL
AH	ACCESS HATCH
AL	ALUMINIUM STRIP
BC	BATTERY CHARGER
BH	BAG HOLDER
BSN	BASIN
BR	BROOM RACK
BRR	BRUSH RACK
BT	BUCKET TRAP
BWU	BOILING WATER UNIT
CBR	COOLROOM BUFFER RAIL
CCB	CLEANING CHEMICAL BASKET
CCR	CLEANING CHEMICAL RACK
CER	CERAMIC
CGB	CORNER GUARD BOLLARD
CH	CEILING HEIGHT
CW	COLD WATER
CWM	CHAINWIRE MESH
CV	CASH VACUUM
DB	DISTRIBUTION BOARD
DPS	DEFLECTION PROTECTION SYSTEM
DR	DOUBLE RAIL
DWR	DRAWER UNDER BENCH
EAS	ELECTRONIC ALARM SWITCH
EMS	ENERGY MANAGEMENT SYSTEM CONTROL PANEL
FAC	FIRST AID CABINET
FB	FIRE BLANKET
FDC	FORCED DRAFT COOLER
FFL	FINISHED FLOOR LEVEL
FH	FIRE HYDRANT
FHR	FIRE HOSE REEL
FW	FLOOR WASTE
GR	GUARD RAIL
HH	HOSE REEL HOLDER (EXISTING)
HND	HARNET DISPENSER
HR	HANDRAIL
HW	HOT WATER
HWS	HOT WATER SYSTEM
ICP	INSULATED COOLROOM PANEL
INS	INSECTOCUTOR
KH	KNIFE HOLDER
LD	LABEL DISPENSER
LP	LABEL PRINTER
MB	MILD STEEL BOLLARD
MSB	MAIN SWITCH BOARD
MW	MICROWAVE
MR	MOP RACK
PA	PUBLIC ADDRESS SYSTEM
PDL	PENDANT LIGHT
PHS	PHONE SHELF
RC	ROLL CAGE
RDL	RECESSED DOWN LIGHT
RPR	RECYCLED PLASTIC BUMP RAIL
SD	SOAP DISPENSER
SSA	STAINLESS STEEL ANGLE
SSC	STAINLESS STEEL CHANNEL
TCD	TORK CLOTH DISPENSER
TTD	TORK TOWEL DISPENSER
TD	TUNDISH
TOW	TOP OF WALL
UR	UNIFORM RACK
UTR	UTENSIL RACK
WB	WHITEBOARD
WP-B	WALL PROTECTION - BUFFER RAIL
WP-BV	WALL PROTECTION - BUFFER RAIL WITH VINYL PANEL
WP-CB	WALL PROTECTION - CHAIR BUFFER RAIL
WP-TB	WALL PROTECTION - TIMBER BUFFER RAIL
WP-TT	WALL PROTECTION - TROLLEY TIMBER BUFFER RAIL WITH RHS
WS	WORKSTATION
XHDG-BT	EXTRA HEAVY DUTY GRATE DRAIN WITH BUCKET TRAP

SCOPE ABBREVIATIONS	
SCP-B	SCOPE BY BUILDER
SCP-C	SCOPE BY CLEANING CONTRACTORS
SCP-E	SCOPE BY ELECTRICAL CONTRACTORS
SCP-IT	SCOPE BY IT
SCP-L	SCOPE BY LOYALTY OPERATIONS
SCP-M	SCOPE BY MECHANICAL CONTRACTORS
SCP-REF	SCOPE BY REFRIGERATION CONTR.
SCP-V	SCOPE BY EQUIPMENT VENDORS
SCP-WW_C	SCOPE BY WOW CONTRACTORS

TRADING BAY BREAKDOWN

Description	Total Bays
Checkouts	
MINI MERCH CONFECT	5
Chilled	
GRAVITY FEED UNIT	6
Grocery	
1050MM HIGH TRADING FIXTURE	6
1420MM TRADING FIXTURE	10
FULL HEIGHT FIXTURE	517
FULL HEIGHT FIXTURE - 750 SHELF	14
FULL HEIGHT FIXTURE - NARROW	3
Produce	
3-TIER STOCK TROLLEY	1
FREE FRUIT FOR KIDS	1

AREA - RATIO

Type	Area	Ratio
Trading	2130.24 m²	64%
Non-Trade	1182.96 m²	36%
Total	3313.19 m²	

AREA - NON TRADE

Department	Area	Ratio
Admin-Misc	113.69 m²	10%
Chilled	32.50 m²	3%
Deli	82.30 m²	7%
Frozen Food	21.86 m²	2%
Grocery	309.15 m²	26%
ISB	149.45 m²	13%
Meat	32.73 m²	3%
Misc	143.10 m²	12%
Office	69.83 m²	6%
Online	108.93 m²	9%
Produce	77.21 m²	7%
Seafood	42.22 m²	4%
Grand total	1182.96 m²	

AREA - TRADING

Department	Area	Ratio
Checkouts	217.27 m²	10%
Chilled	138.07 m²	6%
Deli	31.28 m²	1%
Entry-Exit	66.87 m²	3%
Fresh Convenience	193.42 m²	9%
Frozen Food	99.92 m²	5%
Grocery	1021.03 m²	48%
ISB	73.42 m²	3%
Produce	241.75 m²	11%
Seafood	15.44 m²	1%
Service Desk	31.78 m²	1%
Grand total	2130.24 m²	

AREA - EXCLUDED

Department	Area	Ratio
Plant	213.81 m²	100%
Grand total	213.81 m²	

LINE TYPES LEGEND

- BROWN DASHED LINE DENOTES EXTENT OF TF-01 TIMBER WALL CLADDING.
- GREEN DASHED LINE DENOTES EXTENT OF TF-02 TIMBER WALL CLADDING.

REFRIGERATION BAY COUNT

Description	Model	Count	Bays	Doors	Shelves
BAKERY					
5 TIER BAKERY - 2500	LISBONA 2 CLF 95/205 GL	1	2	0	0
			2	0	
DAIRY					
4 DOOR DAIRY - 2500	KM20S1DC4-4W	2	0	8	0
4DR 5 TIER DAIRY - 2500	LISBONA 2 CLF 95/205 GL	1	2	0	0
5 TIER DAIRY CE - 1774	LISBONA 2 CLF 95/205 GL	2	6	0	0
6 DOOR DAIRY - 3750	KM20S1DC4-4W	8	0	48	0
6DR 5 TIER DAIRY - 3750	LISBONA 2 CLF 95/205 GL	1	3	0	0
			11	56	
DELI					
4 TIER DELI - 3750	SME152-nDE-2W	1	3	0	0
4 TIER DELI CE - 1750	SME152-nDE-2W	2	2	0	0
SERVICE SQUARE -DELI 2448 + CHICKEN 1224 + DIVIDER	DD13-nDE1-1W	1	0	0	
SERVICE SQUARE -DELI-3672	DD13-nDE1-1W	1	0	0	
			5	0	
Deli - Self Serve					
6ft INLINE CHICKEN WARMER		1	2	0	
			2	0	
FROZEN					
3DR FROZEN FOOD	KG20S1FZE-4W	2	0	6	0
4DR FROZEN FOOD	KG20S1FZE-4W	2	0	8	0
5DR FROZEN FOOD	KG20S1FZE-4W	7	0	35	0
			0	49	
MEALS					
4 TIER MEALS - 3750	SME152-nDE-2W	1	3	0	0
4 TIER MEALS CE - 1750	SME152-nDE-2W	1	1	0	0
5 TIER MEALS - 2500	LISBONA 2 CLF 95/205 GL	2	4	0	5
5 TIER MEALS CE - 2183	LISBONA 2 CLF 95/205 GL	1	3	0	0
			11	0	
MEAT					
4 TIER MEAT - 3750	SME152-nDE-2W	6	18	0	12
4 TIER MEAT CE - 1750	SME152-nDE-2W	5	5	0	6
PET FRIDGE - 4 DOOR	Multifresh Plus Modular	1	2	4	12
			25	4	
PRODUCE					
4 TIER PRODUCE - 2500	SME152-nPR-2W	1	2	0	0
5 TIER PRODUCE -2500	LISBONA 2 CLF 95/205 GL	2	4	0	0
5 TIER PRODUCE - 3750	LISBONA 2 CLF 95/205 GL	2	6	0	0
5 TIER PRODUCE CE - 2183	LISBONA 2 CLF 95/205 GL	1	3	0	0
5 TIER PRODUCE FOGGING - 3750	LISBONA 2 CLF 95/205 GL	1	3	0	0
ISLAND BERRY CASE	85	1	0	0	
			18	0	
SEAFOOD					
3DR SEAFOOD	KG20S1FFE-4W	1	0	3	0
5 TIER SEAFOOD - 2500	LISBONA 2 CLF 95/205 GL	1	2	0	0
SERVICE SQUARE -SEAFOOD-2448	DC13-*F1-1W	1	0	0	
			2	3	
Trading Floor					
PBU INFILL	960.270	1	0	0	
REFRIG. INFILL	960.270	2	0	0	
			0	0	

No.	DRAWING AMENDMENTS (REVISIONS)	DATE	BY
J	DWR#3501 AND #3557 - REVISE DRIVE THRU LAYOUT, 4 BAYS ADDED. UPDATE PLAN TO ALLOW FOR VALUE OVERLAY SCOPE, UPDATE SIGNAGE AND NOTES. REMOVE TIMBER CLADDING ON EXIT CHECKOUT WALL AND TROLLEY PARK WALL. REMOVE FEATURE WALL FROM DELI AND SEAFOOD PREP AREAS. REMOVE 9 BOLLARDS IN THE LOADING DOCK AND ADJUST LINE MARKING TO ALIGN WITH DOCK BUMPER. UPDATE PET FOOD CASE AND ADJUST FIXTURES TO SUIT. ADD COVID BUNDLE THROUGHOUT.	11/10/2021	CG-WW CA-TRG
K	NEW PHASE 3 WELCOME GATE AND SERVICE DESK. REMOVED 2X BAYS AND RELOCATED GONDOLA END TO INCREASE CLEARANCE. CHANGED LAYOUT TO SUIT. ADDED 2X CASHLESS SCOS. UPDATED SCO LAYOUT AS SHOWN. CHANGED SCO AND DTB ROOM NAMES AS PER LATEST STANDARDS. NEW CONFEC, MERCH AND 1X AMBIENT TOPPER FRIDGE TO SCO WALL. ADDED SCAN & GO, MOVED CHECKOUTS TO SUIT. REDUCED TO 6X BELTED CHECKOUTS AS SHOWN. REMOVED 1X BAY TO SUIT NEW LAYOUT. RELOCATED TEAM ENTRY TO DTB AMBIENT. ADDED NEW DTB FREEZER. UPDATED DTB LAYOUT AS SHOWN. REVISED DTB DRIVE-THRU LAYOUT TO MATCH LATEST STANDARDS. REPLACED TOTES TO NEW TYPE. ADDED SMART BUNDLE NOTE. NEW VR SHELF TO GENERAL OFFICE. NEW BARRIER GATES TO SAFETY ZONE. ADDED DRIVER NOTE TO LOADING DOCK. REPLACED BIN LIFTER AS SHOWN. NEW IMPULSE TABLE. REMOVED HOT FOOD CASE AND INCREASED SERVICE DELI TO 36/72. REPLACED SCALES TO DELI/CHICKEN/SEAFOOD PREP AS PER LATEST STANDARDS. RELOCATE SCANNER AT TEAM ROOM.	17/12/2021	IP - TRG
L	UPDATED 180MM SETDOWN EXTENTS, SHOW EXPANSION JOINTS AS PER LATEST CONCRETE SETOUT PLAN RECEIVED. UPDATE BARRIER. PROVIDE DOOR BELL FOR DELIVERY, UPDATE FOGGING UNIT, EXTEND LOW HEIGHT WALL BY 200MM NEXT TO ENTRY GATE AND MOVE MEDIA SCREEN UP.	18/01/2022	KY - TRG

DRAFTED BY:
CDS-TRG

NOTES

Plot: 20/01/2022 4:05:53 PM
Template Version: 2019.1.01_15.30
Shared Parameters Version: WW_Bld_20131214.txt
File: C:\Users\1152279\Downloads\22-01-18-202001187dc01242-001\22-01-18\3442 - Gordonvale West - Control Plan.rvt

trg MELBOURNE
MELBOURNE OFFICE
The Retail Group Pty Ltd ABN 69 050 134 686 © - COPYRIGHT 2012
Lvl 3, Suite 37, 799 Springvale Rd
Mulgrave
Victoria
3170 Australia
P +61 3 9542 9300
F +61 3 9542 9310
E trg@trg-aus.com
W www.trg-aus.com

woolworths
The fresh food people

ALL DIMENSIONS, SIZES, ETC. ARE IN MILLIMETERS. **DO NOT SCALE DIRECTLY FROM DRAWINGS.** ALWAYS USE FIGURED DIMENSIONS.
THIS DRAWING TO BE READ IN CONJUNCTION WITH ELECTRICAL, MECHANICAL, HYDRAULIC, DETAIL STANDARD DRAWINGS AND CONSTRUCTION SUMMARY.
THIS DRAWING IS FOR DESIGN GUIDANCE ONLY. FINAL DETAILS MUST MEET SITE CONDITIONS, RELEVANT AUTHORITIES AND APPLICABLE BUILDING STANDARDS.

PROJECT ADDRESS :
Cnr Bruce Hwy and Draper Road, Gordonvale (Carins), QLD 4865 Australia

BLUEPRINT ISSUE :
BRP 2018.1 REV B

DRAWN BY : CDS-TRG
APPROVED BY : C. GUIAO
ISSUED TO : WW

DRAWING :
Control Plan

STORE 2642

DOC STAGE:WA200 | FITOUT

PROJECT :
WOOLWORTHS Gordonvale West

SCALE : 1 : 100 @ A0
ISSUE DATE : 18/01/2022
REGION / STATE : QLD
PROJECT No : 2642
DRAWING No : **WA200**
AMEND. No : **L**