


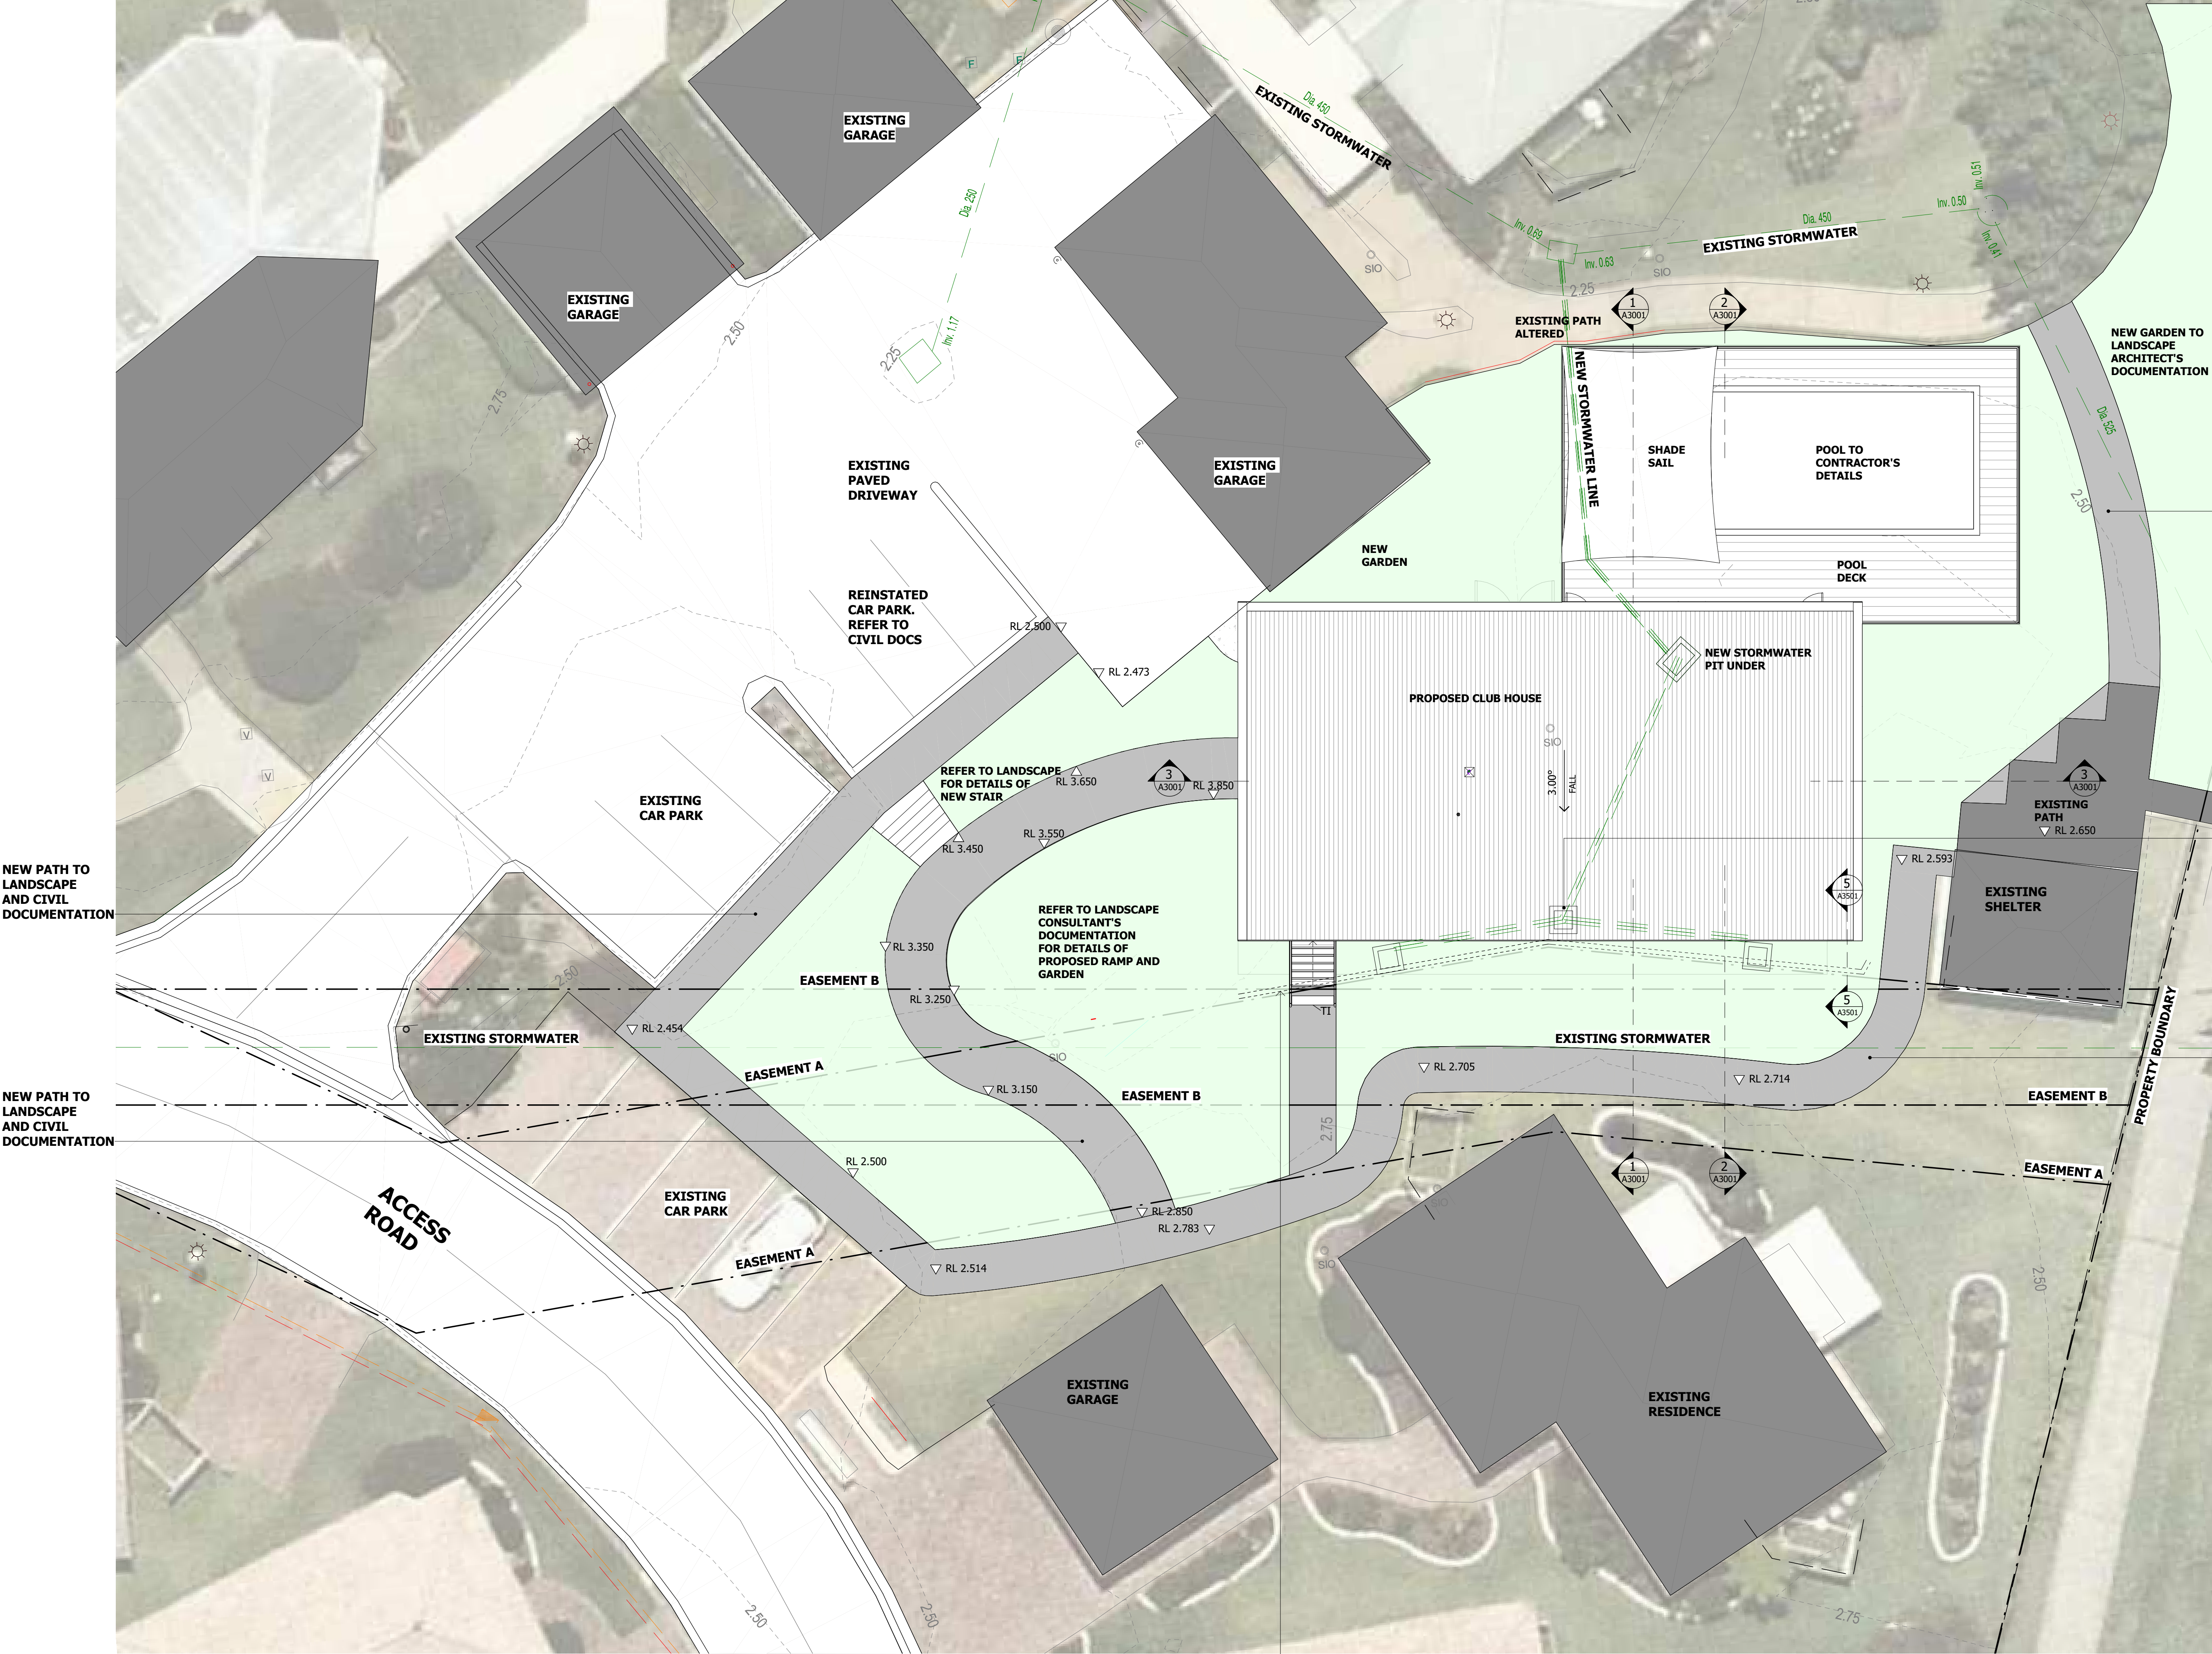

NEW PATH TO
LANDSCAPE
AND CIVIL
DOCUMENTATION

NEW PATH TO
LANDSCAPE
AND CIVIL
DOCUMENTATION

RETAINING WALL
LEVELS TO CONFIRM
WITH THE CIVIL
ENGINEER

Notes

The information contained in this document is copyright and may not be used or reproduced for any other project or purpose.
Verify all dimensions and levels on site and report any discrepancies to dwp for direction prior to the commencement of work.
Drawings are to be read in conjunction with all other contract documents.

Use figured dimensions only. Do not scale from drawings.
dwp cannot guarantee the accuracy of content and format for copies of drawings issued electronically. The completion of the Issue Details Checked and Authorised section is confirmation of the status of the drawing. The drawing shall not be used for construction unless endorsed 'For Construction' and authorised for issue.

© dwp Australia Pty Ltd
Registered Business Name dwp Australia ABN 37 169 328 018
Nominated Architect Angus Rose NSW ARB 8341 &
Nominated Architect Cameron Martin NSW ARB 9194
© Copyright 2011 dwp.
ALL RIGHTS RESERVED.
Reproduction prohibited unless authorised in writing by dwp.


NOTE: ALL STORMWATER PITS TO BE COORDINATED WITH CIVIL AND LANDSCAPE BEFORE CONSTRUCTION

NEW PATH TO LANDSCAPE DOCUMENTATION

LINE LEGEND

ELECTRICAL SERVICE	---	---	---
FENCE	---	---	---
STORMWATER SERVICE	---	---	---
TELECOM SERVICE	---	---	---
WATER SERVICE	---	---	---
DEMOLITION	---	---	---
EXISTING EASEMENT	---	---	---
STORMWATER PIT	---	---	---

DRAINAGE PIT LOCATIONS O BE CONFIRMED WITH CIVIL ENGINEER

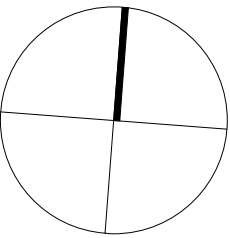

FOR TENDER

NOT TO BE USED DURING CONSTRUCTION

NEW PATH TO LANDSCAPE DOCUMENTATION

C	TENDER ISSUE	23.12.2021	FK	DB
B	JOINERY UPDATE	10.12.2021	FK	DB
A	UPDATED DRAWINGS FOR COORDINATION	06.12.2021	FK	DB

Issue	Description	Date	Chk	Auth
Architect/ Designer	dwp			
	www.dwp.com			
Client	Bolton Clarke			

Project
Galleon Gardens Club House

Location
126-134 Galleon Way
Currumbin Waters, QLD

Project Number
21-0511

Drawing
SITE PLAN - PROPOSED

Scale (A1)	Date Printed
1 : 100	23/12/2021 11:03:04 AM
Drawing Number	Issue

A1101

C

dwp

File Name: B:\21-0511_Galleon Gardens Club House\21-0511-A&S-GCH-R19.rvt