


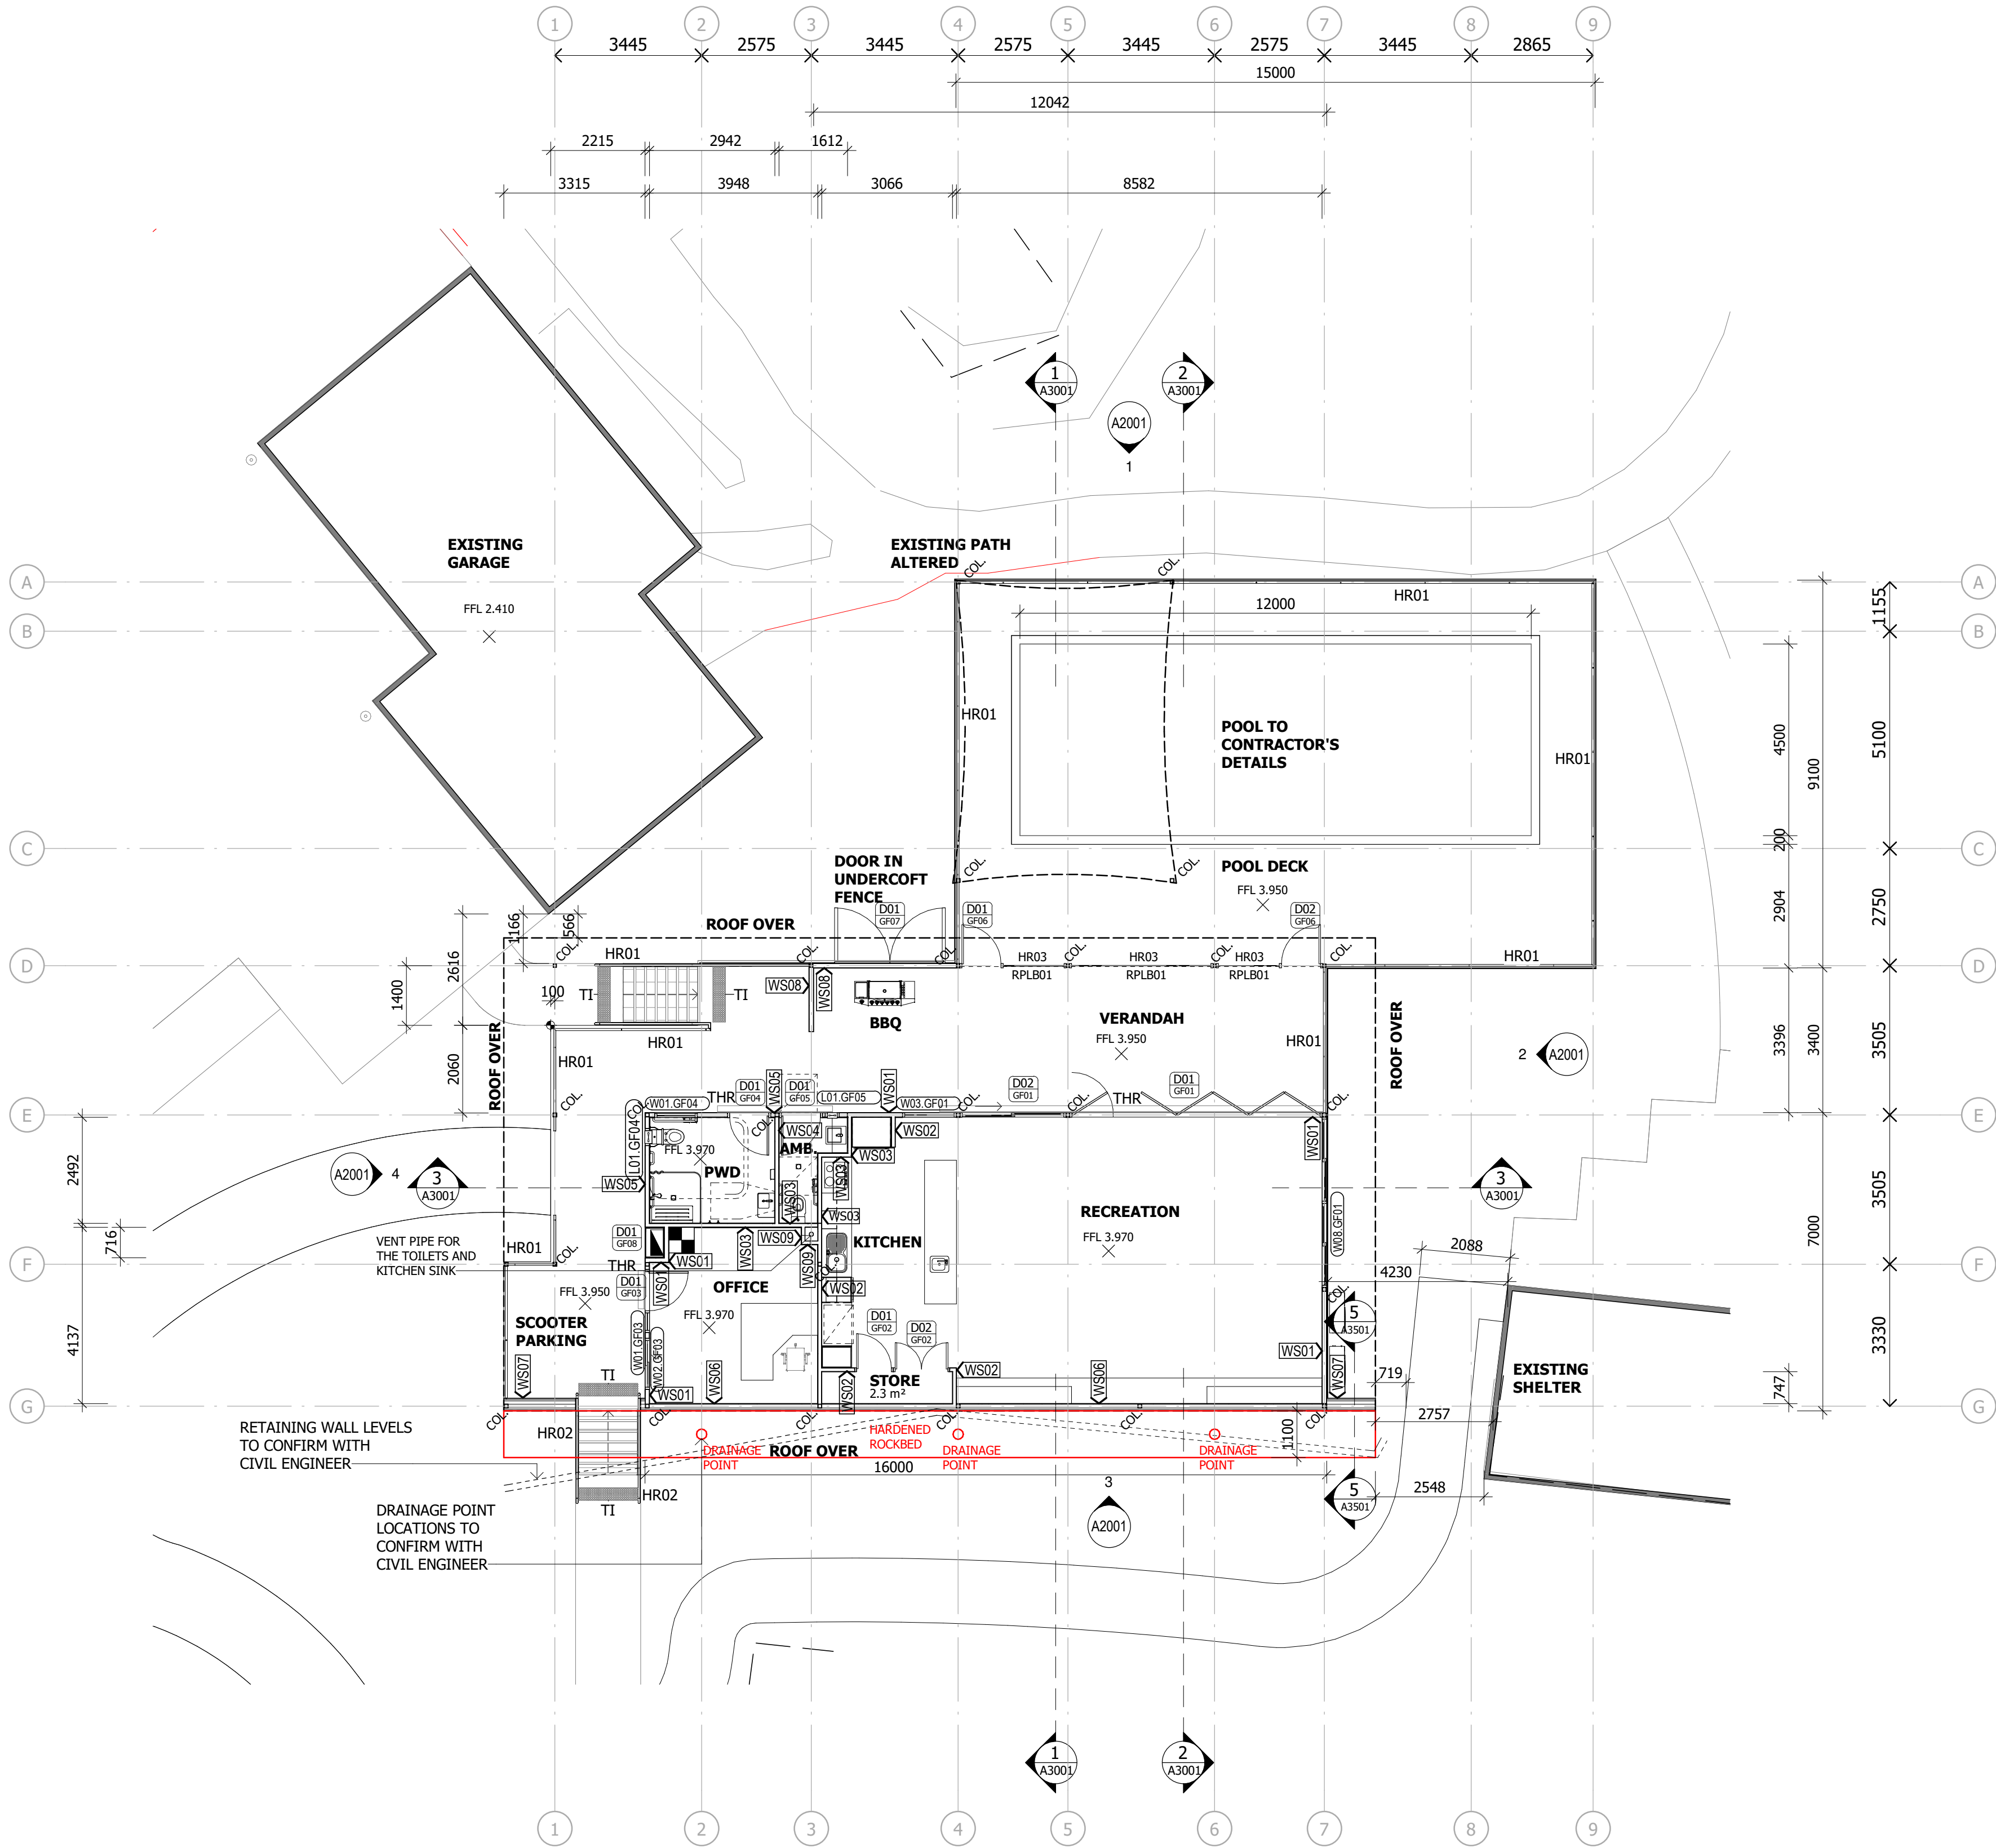

1 GA PLAN - GROUND FLOOR
A2001 1 : 100

WALL SCHEDULE

(WS) STEEL CORE LAYER WALLS

WS01

EXTERNAL SIDE

	7.5mm FC WEATHERBOARD CLADDING (FC01)
92mm METAL STUD, INSULATION (INS02)	
9mm PLASTERBOARD	

THERMAL INSULATION: INS02
ACOUSTIC INSULATION: NIL
FIRE RESISTANCE LEVEL: -/-
OTHER: NA

WS02

EXTERNAL SIDE

	9mm PLASTERBOARD
76mm METAL STUD, INS04	
9mm PLASTERBOARD	

THERMAL INSULATION: NIL
ACOUSTIC INSULATION: INS04
FIRE RESISTANCE LEVEL: -/-
OTHER: NA

WS03

EXTERNAL SIDE

	9mm PLASTER BOARD
76mm METAL STUD, INS04	
9mm MOISTURE RESISTANT PLASTERBOARD	

THERMAL INSULATION: NIL
ACOUSTIC INSULATION: INS04
FIRE RESISTANCE LEVEL: -/-
OTHER: NA

WS04

EXTERNAL SIDE

	9mm MOISTURE RESISTANT PLASTERBOARD
76mm METAL STUD, INS04	
9mm MOISTURE RESISTANT PLASTERBOARD	

THERMAL INSULATION: NIL
ACOUSTIC INSULATION: INS04
FIRE RESISTANCE LEVEL: -/-
OTHER: NA

WS05

EXTERNAL SIDE

	7.5mm FC WEATHERBOARD CLADDING (FC01)
92mm METAL STUD, INSULATION (INS02)	
9mm MOISTURE RESISTANT PLASTERBOARD	

THERMAL INSULATION: INS02
ACOUSTIC INSULATION: NIL
FIRE RESISTANCE LEVEL: -/-
OTHER: NA

WS06

EXTERNAL SIDE

	29mm METAL WALL CLADDING
35mm FURRING CHANNEL	
92mm METAL STUD, INSULATION (INS02)	
9mm PLASTER BOARD	

THERMAL INSULATION: INS02
ACOUSTIC INSULATION: NIL
FIRE RESISTANCE LEVEL: -/-
OTHER: NA

WS07

EXTERNAL SIDE

	29mm METAL WALL CLADDING
35mm FURRING CHANNEL	
92mm METAL STUD	
76mm METAL STUD	
35mm FURRING CHANNEL	
29mm METAL WALL CLADDING	

THERMAL INSULATION: NIL
ACOUSTIC INSULATION: NIL
FIRE RESISTANCE LEVEL: -/-
OTHER: NA

WS08

EXTERNAL SIDE

	7.5mm FC WEATHERBOARD CLADDING
92mm METAL STUD	
9mm FC CLADDING (FC02)	

THERMAL INSULATION: NIL
ACOUSTIC INSULATION: NIL
FIRE RESISTANCE LEVEL: -/-
OTHER: NA

WS09

EXTERNAL SIDE

	92mm METAL STUD
9mm PLASTERBOARD	

THERMAL INSULATION: NIL
ACOUSTIC INSULATION: NIL
FIRE RESISTANCE LEVEL: -/-
OTHER: NA

Notes

The information contained in this document is copyright and may not be used or reproduced for any other project or purpose.

Verify all dimensions and levels on site and report any discrepancies to dwp for direction prior to the commencement of work.


Drawings are to be read in conjunction with all other contract documents.

Use figured dimensions only. Do not scale from drawings. dwp cannot guarantee the accuracy of content and format for copies of drawings issued electronically. The completion of the Issue Details Checked and Authorised section is confirmation of the status of the drawing. The drawing shall not be used for construction unless endorsed 'For Construction' and authorised for issue.

© dwp Australia Pty Ltd
Registered Business Name dwp Australia ABN 37 169 328 018
Nominated Architect Angus Rose NSW ARB 8341 &
Nominated Architect Cameron Martin NSW ARB 9194
© Copyright 2011 dwp.
ALL RIGHTS RESERVED.
Reproduction prohibited unless authorised in writing by dwp.

GENERAL NOTES

1. REFER TO STRUCTURAL ENGINEER'S DOCUMENTATION.
2. REFER TO GA PLAN FOR LOCATIONS OF WALL TYPES.
3. REFER TO FINISHES PLANS FOR APPLIED FINISHES.
4. STUD CENTRES ARE TO SUIT WALL HEIGHT REQUIREMENTS UNLESS NOTED OTHERWISE.
5. ALL FLOOR WASTE SETOUT MUST BE CONFIRMED ON SITE.
6. CONTRACTOR TO CO-ORDINATE JOINTS, LIGHTING AND ALL CEILING PENETRATIONS.
7. FURNITURE IS SHOWN ON THE DRAWING FOR DEMONSTRATION PURPOSE.
8. DRAINAGE POINTS ARE INDICATIVE, FINAL COORDINATED WITH CIVIL

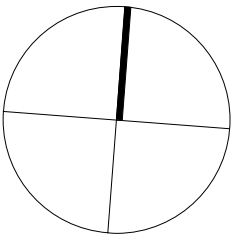

FOR TENDER

NOT TO BE USED DURING CONSTRUCTION

D	TENDER ISSUE	23.12.2021	FK	DB
C	COORDINATION UPDATE	21.12.2021	FK	DB
B	JOINERY UPDATE	10.12.2021	FK	DB
A	UPDATED DRAWINGS FOR COORDINATION	06.12.2021	FK	DB

Issue	Description	Date	Chk	Auth
-------	-------------	------	-----	------

Architect/ Designer

dwp

www.dwp.com

Client

Bolton Clarke

Project

Galleon Gardens Club House

Location

126-134 Galleon Way
Currumbin Waters, QLD

Project Number

21-0511

Drawing

GA PLAN - GROUND
FLOOR

Scale (A1)

As indicated

Drawing Number

A1201

Date Printed

23/12/2021 11:03:07 AM

Issue

Issue

Issue

Issue

Issue

Issue

Issue

Issue

Issue

Issue

Issue

Issue

Issue

dwp

File Name: B:\2021\21-0511_Galleon Gardens Club House\21-0511-148-GCH-R13.rvt