


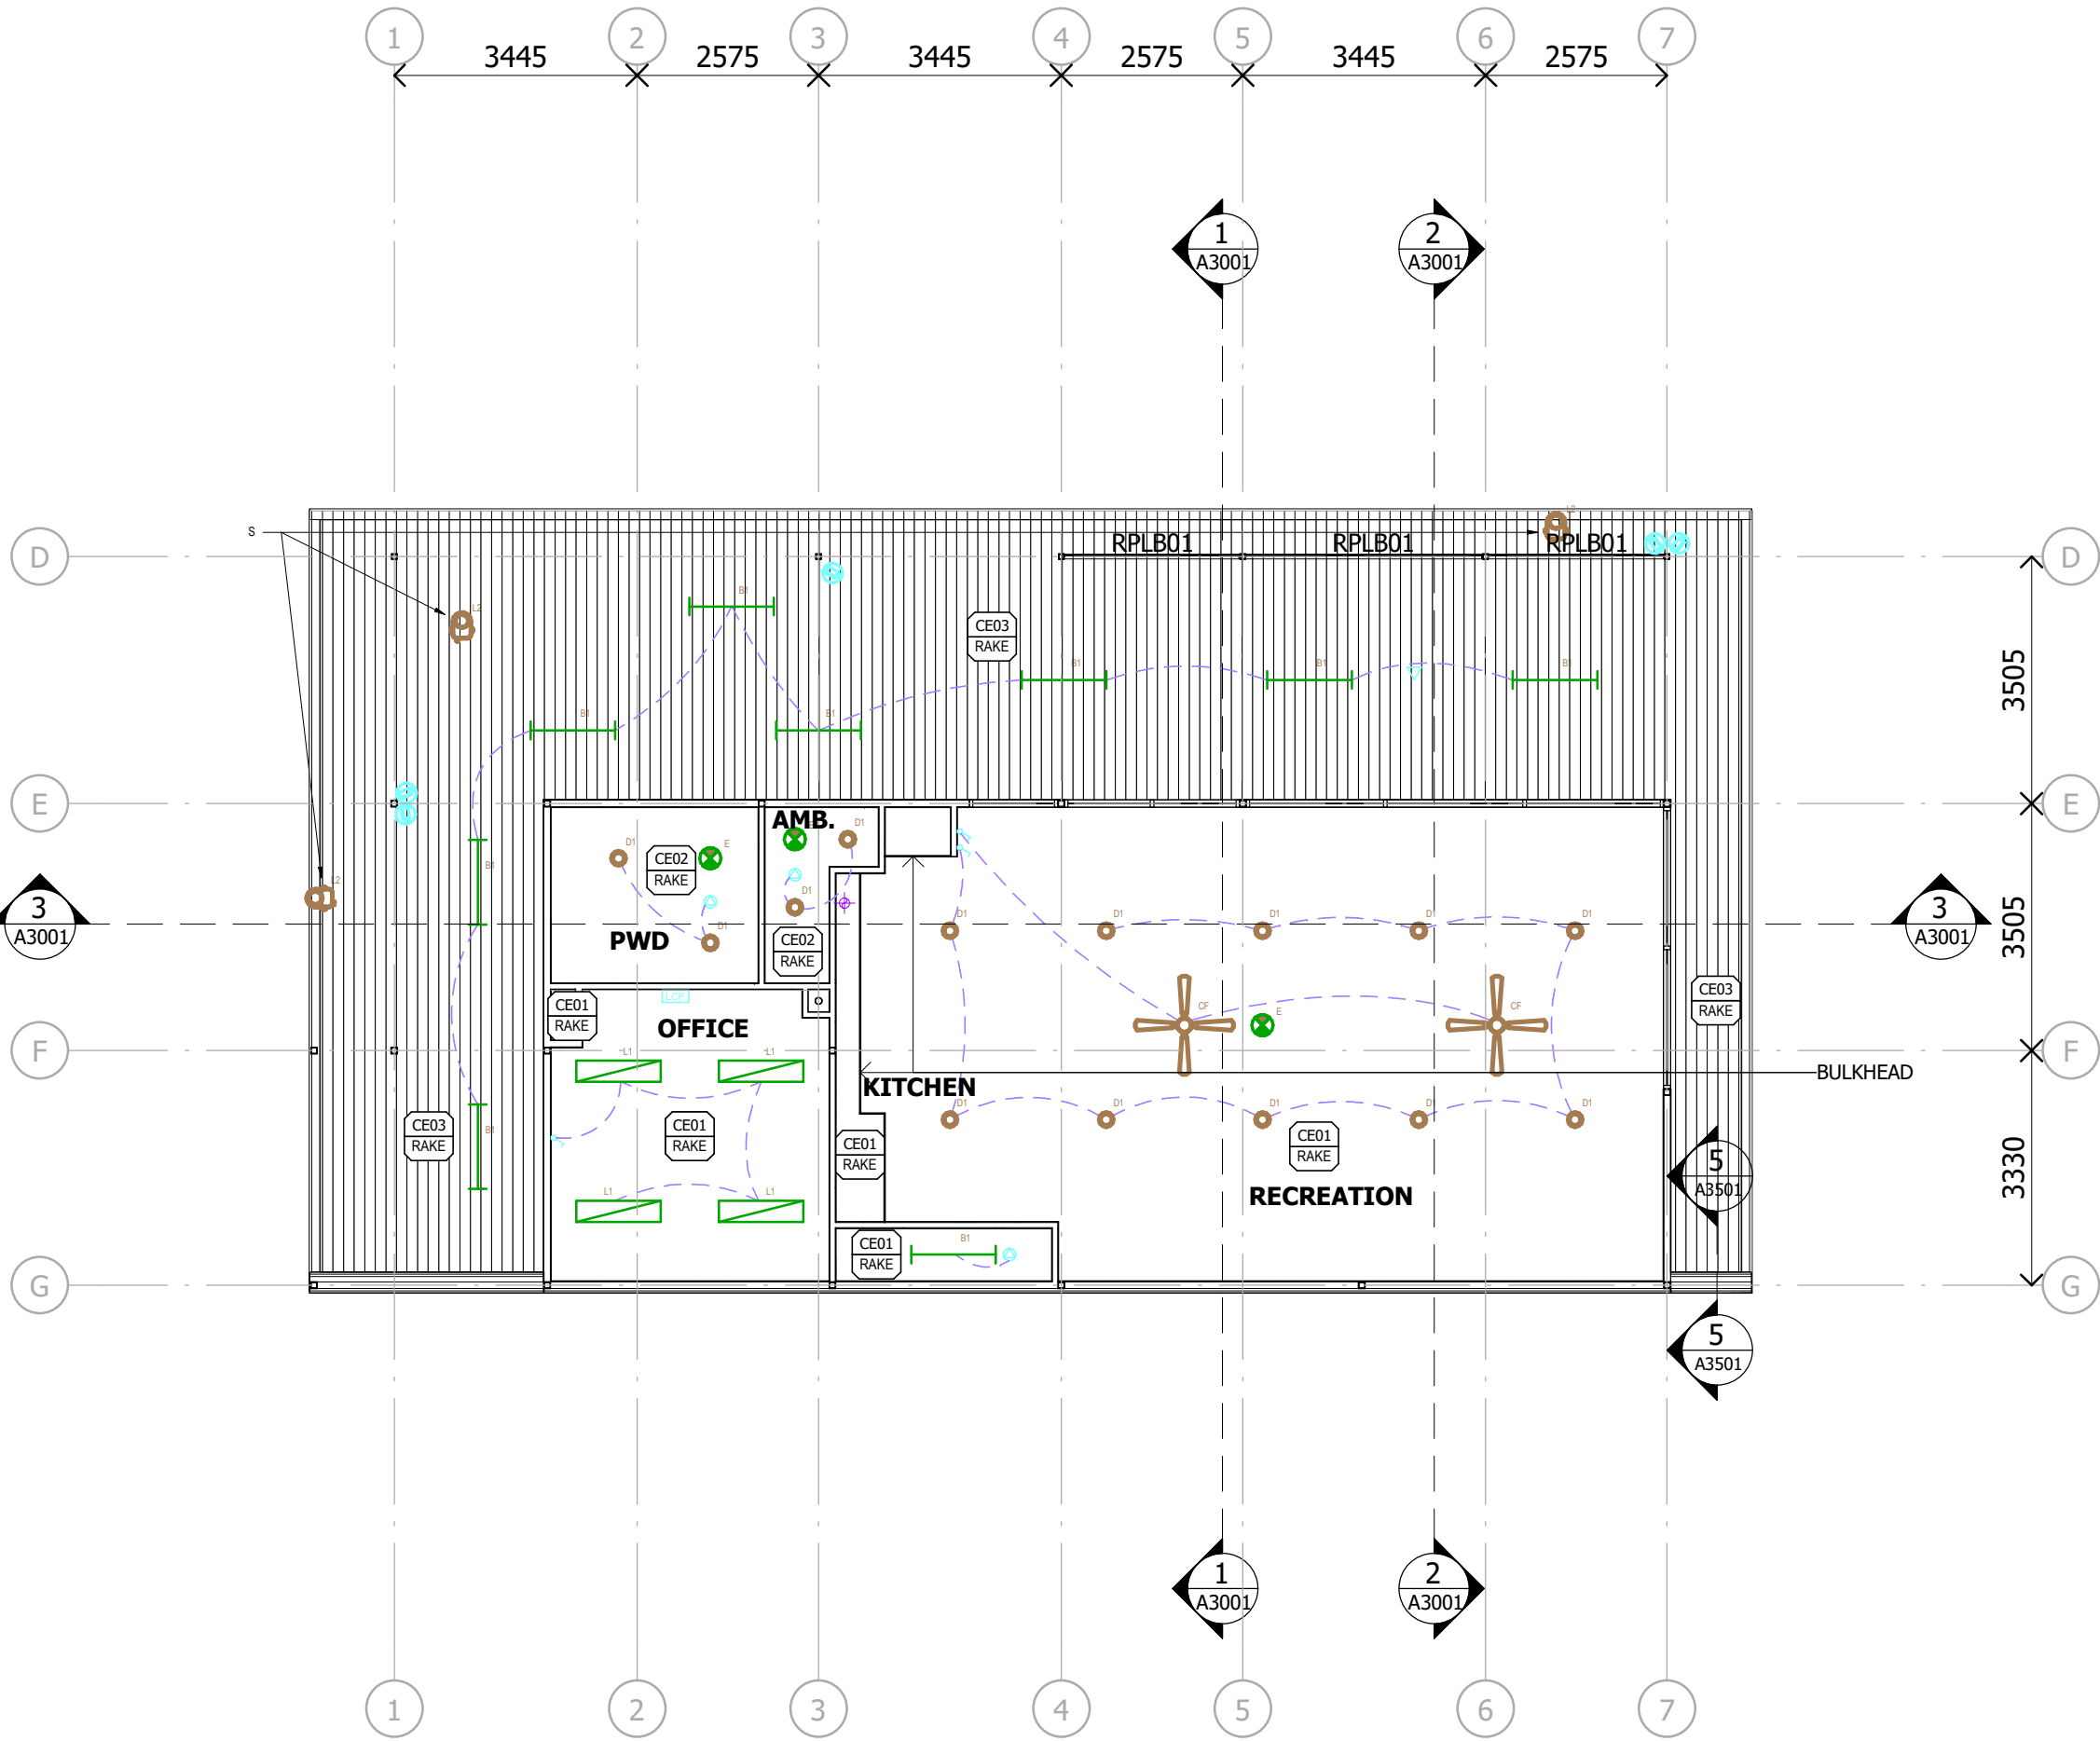

1
A2001
GROUND FLOOR - REFLECTED CEILING PLAN
1 : 100

CEILING SCHEDULE		
CODE	DESCRIPTION	FINISH
CE01	13mm FLUSH PLASTER BOARD	PT02
CE02	13mm FLUSH MOISTURE RESISTANT PLASTERBOARD	PT02
CE03	29mm METAL ROOF SHEETING	MRS01

Notes

The information contained in this document is copyright and may not be used or reproduced for any other project or purpose.

Verify all dimensions and levels on site and report any discrepancies to dwp for direction prior to the commencement of work.


Drawings are to be read in conjunction with all other contract documents.

Use figured dimensions only. Do not scale from drawings. dwp cannot guarantee the accuracy of content and format for copies of drawings issued electronically. The completion of the Issue Details Checked and Authorised section is confirmation of the status of the drawing. The drawing shall not be used for construction unless endorsed 'For Construction' and authorised for issue.

© dwp Australia Pty Ltd
Registered Business Name dwp Australia ABN 37 169 328 018
Nominated Architect Angus Rose NSW ARB 8341 &
Nominated Architect Cameron Martin NSW ARB 9194
© Copyright 2011 dwp.
ALL RIGHTS RESERVED.
Reproduction prohibited unless authorised in writing by dwp.

NOTE

THE CEILING PLAN TO BE READ IN
CONJUNCTION WITH ELECTRICAL
ENGINEER'S DOCUMENTATION

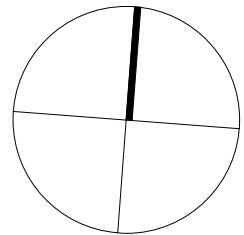

FOR TENDER
NOT TO BE USED DURING CONSTRUCTION

B	TENDER ISSUE	22.12.2021	FK	DB
A	JOINERY UPDATE	10.12.2021	FK	DB
Issue	Description	Date	Chk	Auth

Architect/ Designer
dwp
www.dwp.com

Client
Bolton Clarke

Project
Galleon Gardens Club House

Location
126-134 Galleon Way
Currumbin Waters, QLD

Project Number
21-0511

Drawing
REFLECTED CEILING
PLAN

Scale (A1)	Date Printed
1 : 100	22/12/2021 5:57:42 PM
Drawing Number	Issue

A1801

B

