

Notes

The information contained in this document is copyright and may not be used or reproduced for any other project or purpose.

Verify all dimensions and levels on site and report any discrepancies to dwp for direction prior to the commencement of work.

Drawings are to be read in conjunction with all other contract documents.

Use figured dimensions only. Do not scale from drawings. dwp cannot guarantee the accuracy of content and format for copies of drawings issued electronically. The completion of the Issue Details Checked and Authorised section is confirmation of the status of the drawing. The drawing shall not be used for construction unless endorsed 'For Construction' and authorised for issue.

© dwp Australia Pty Ltd  
Registered Business Name dwp Australia ABN 37 169 328 018  
Nominated Architect Angus Rose NSW ARB 8341 &  
Nominated Architect Cameron Martin NSW ARB 9194  
© Copyright 2011 dwp.  
ALL RIGHTS RESERVED.  
Reproduction prohibited unless authorised in writing by dwp.

SCHEMATIC DESIGN

NOT TO BE USED DURING CONSTRUCTION

|                     |              |            |     |      |
|---------------------|--------------|------------|-----|------|
| A                   | TENDER ISSUE | 23.12.2021 | FK  | DB   |
| Issue               | Description  | Date       | Chk | Auth |
| Architect/ Designer |              |            |     |      |
| dwp                 |              |            |     |      |
| www.dwp.com         |              |            |     |      |
| Client              |              |            |     |      |
| Bolton Clarke       |              |            |     |      |

Project

Galleon Gardens Club House

Location

126-134 Galleon Way  
Currumbin Waters, QLD

Project Number

21-0511

Drawing

DETAILED SECTIONS

Scale (A1)

1 : 20

Date Printed

23/12/2021 11:08:58 AM

Drawing Number


A3502

Issue


A



File Name: B:\B\3662\21-0511\_Galleon Gardens Club House\21-0511-AS-GSCH-R19.rvt

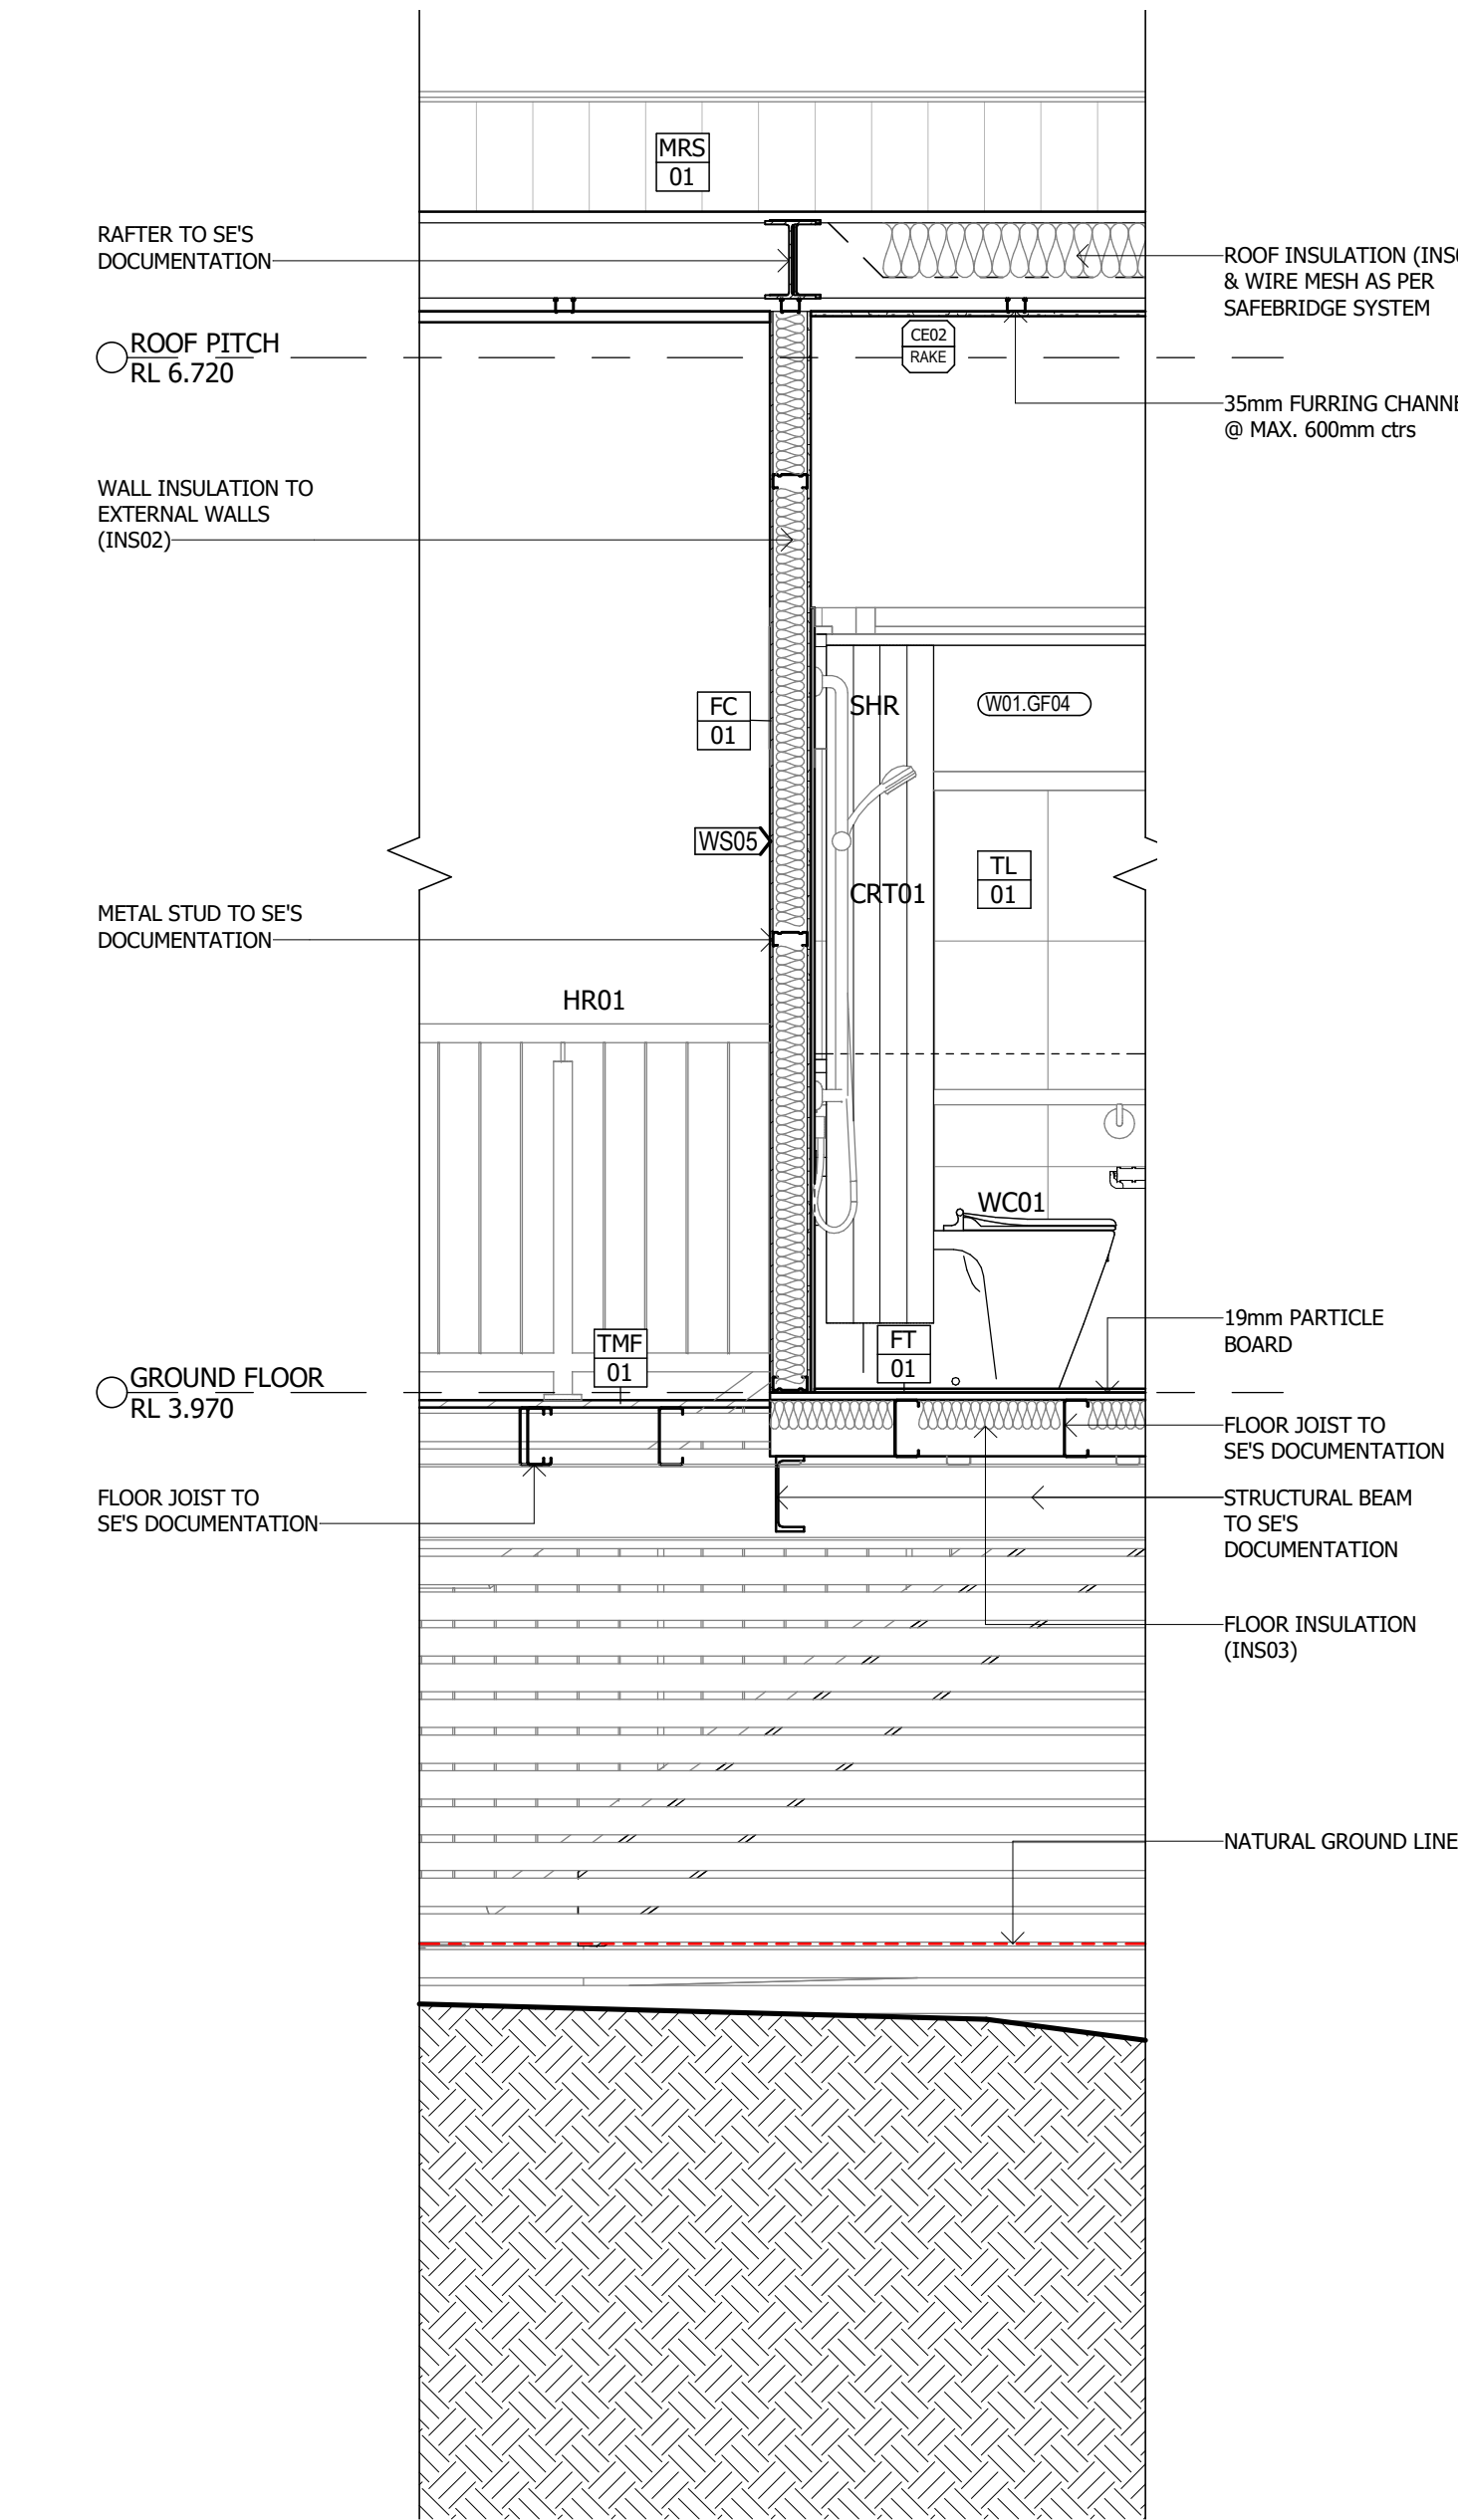

1 DETAIL SECTION 3  
A3001 1 : 20

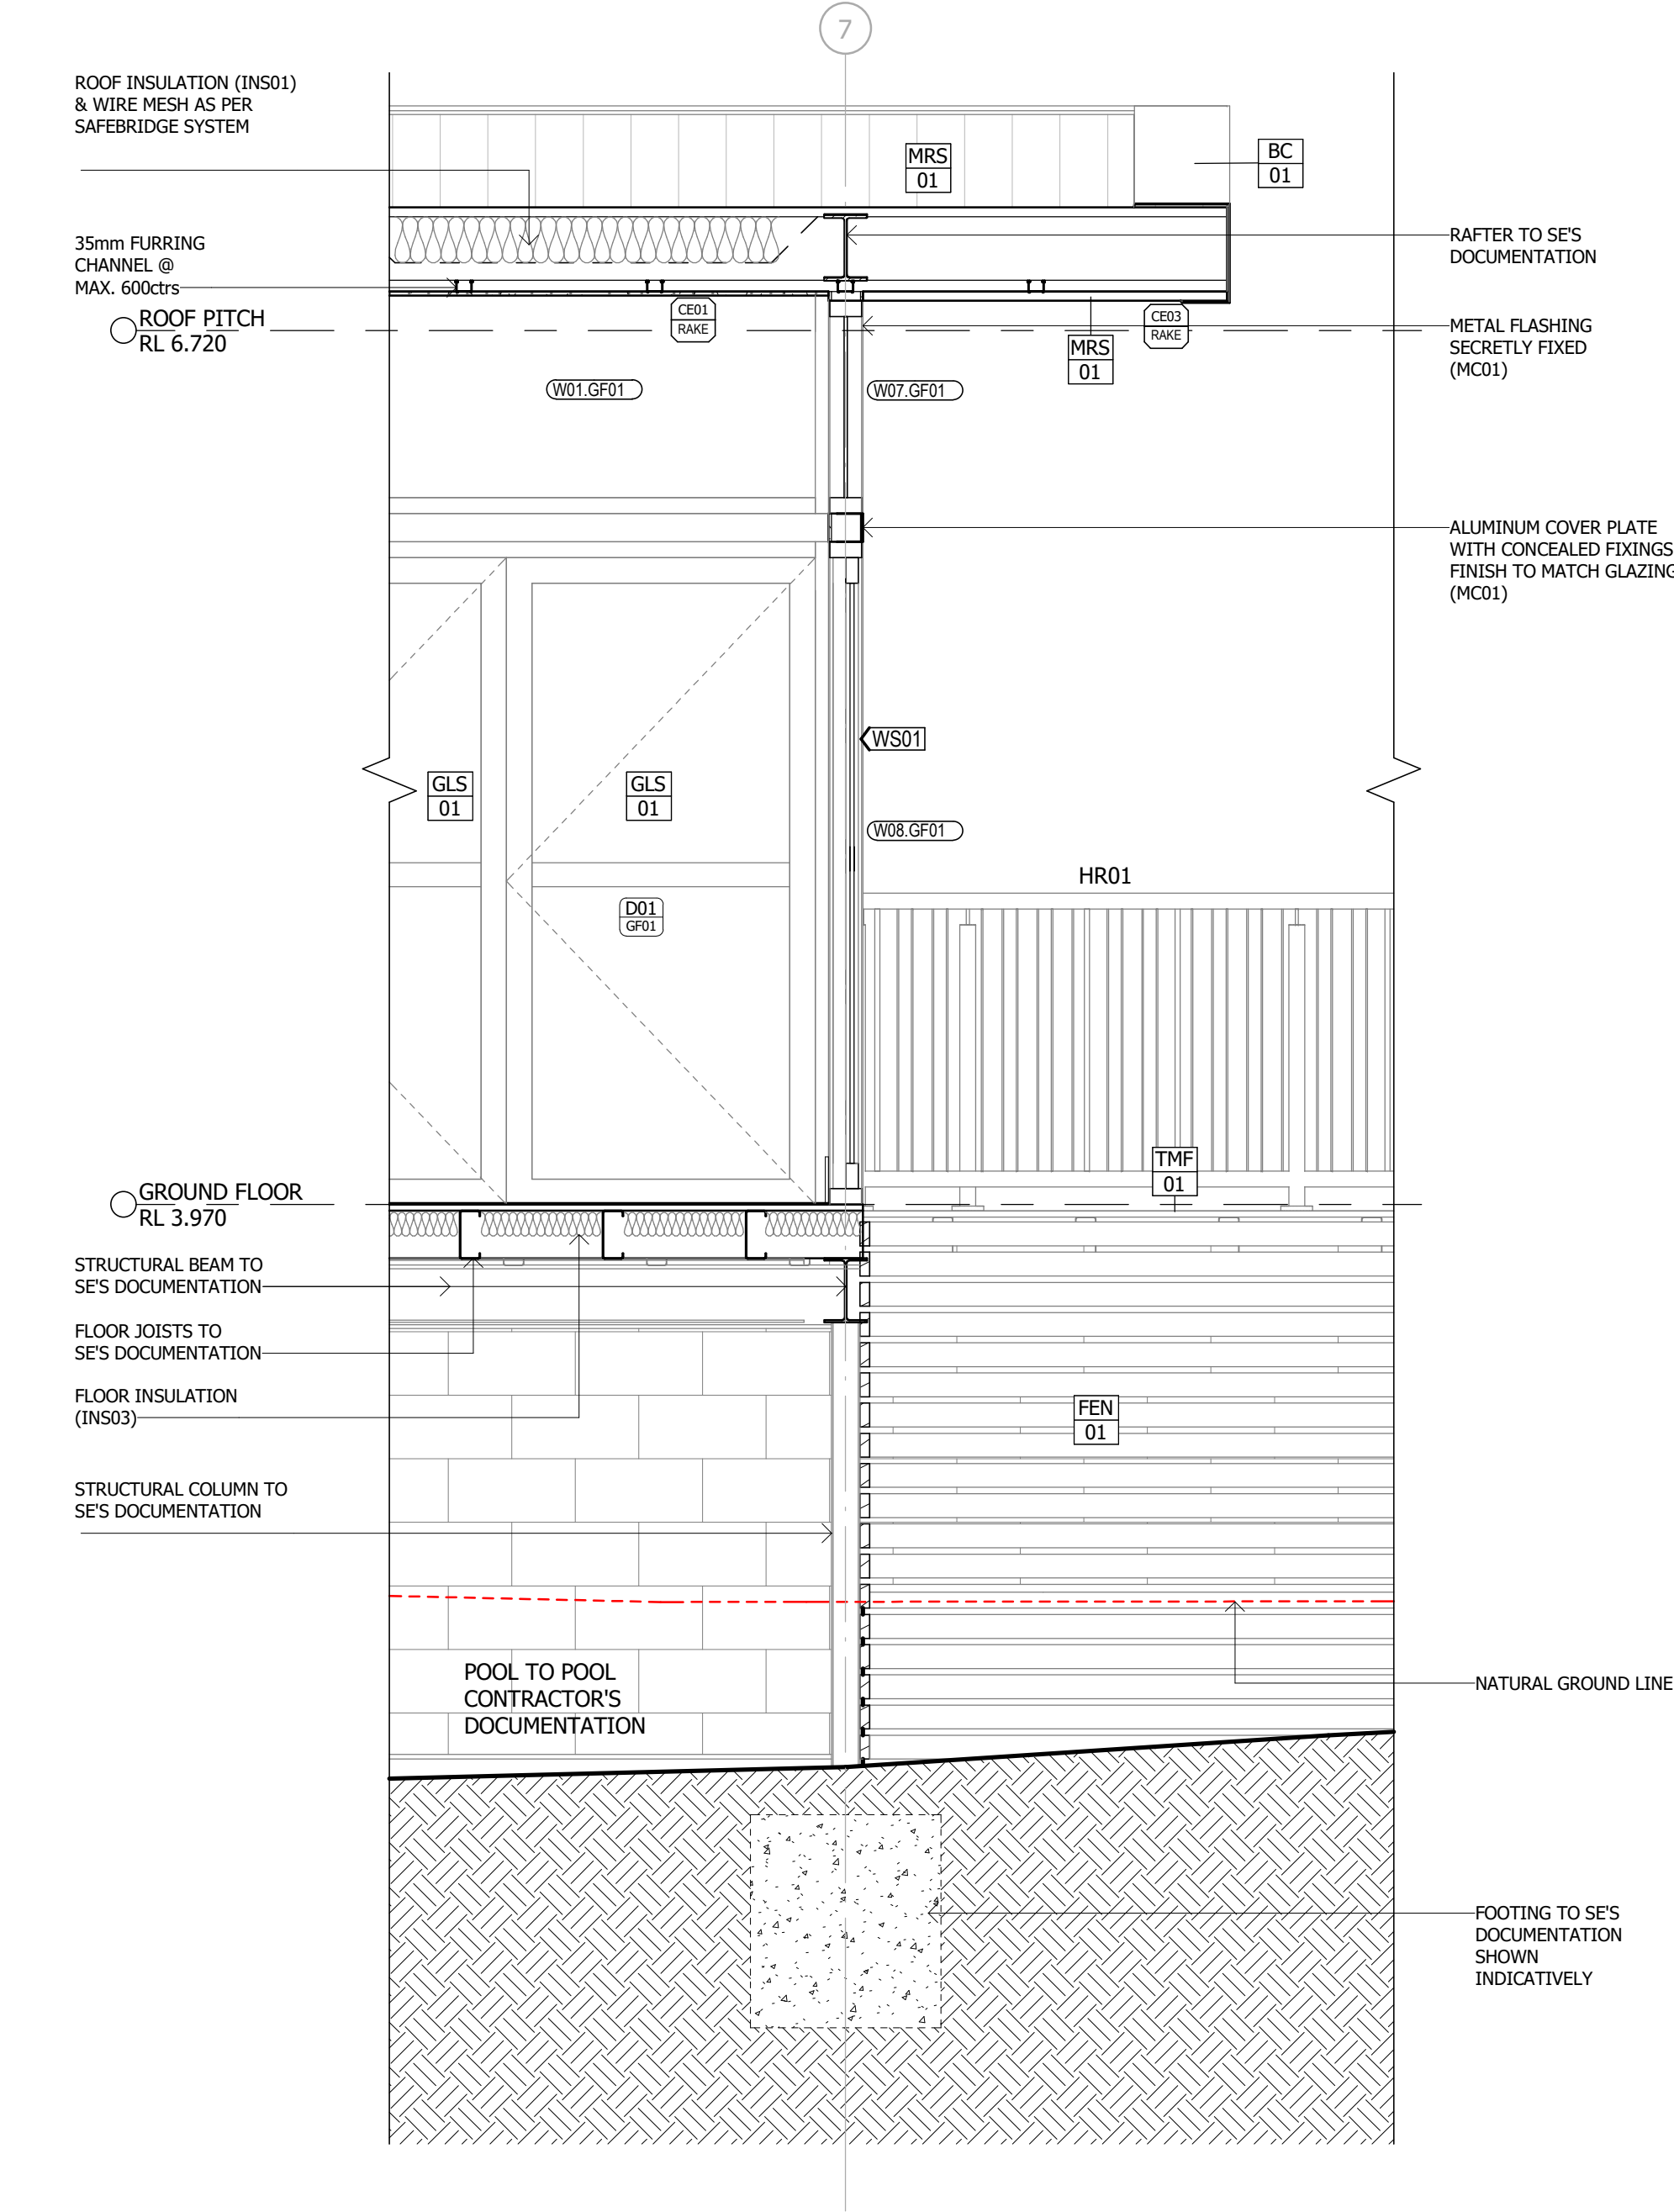

2 DETAIL SECTION 4  
A3001 1 : 20