




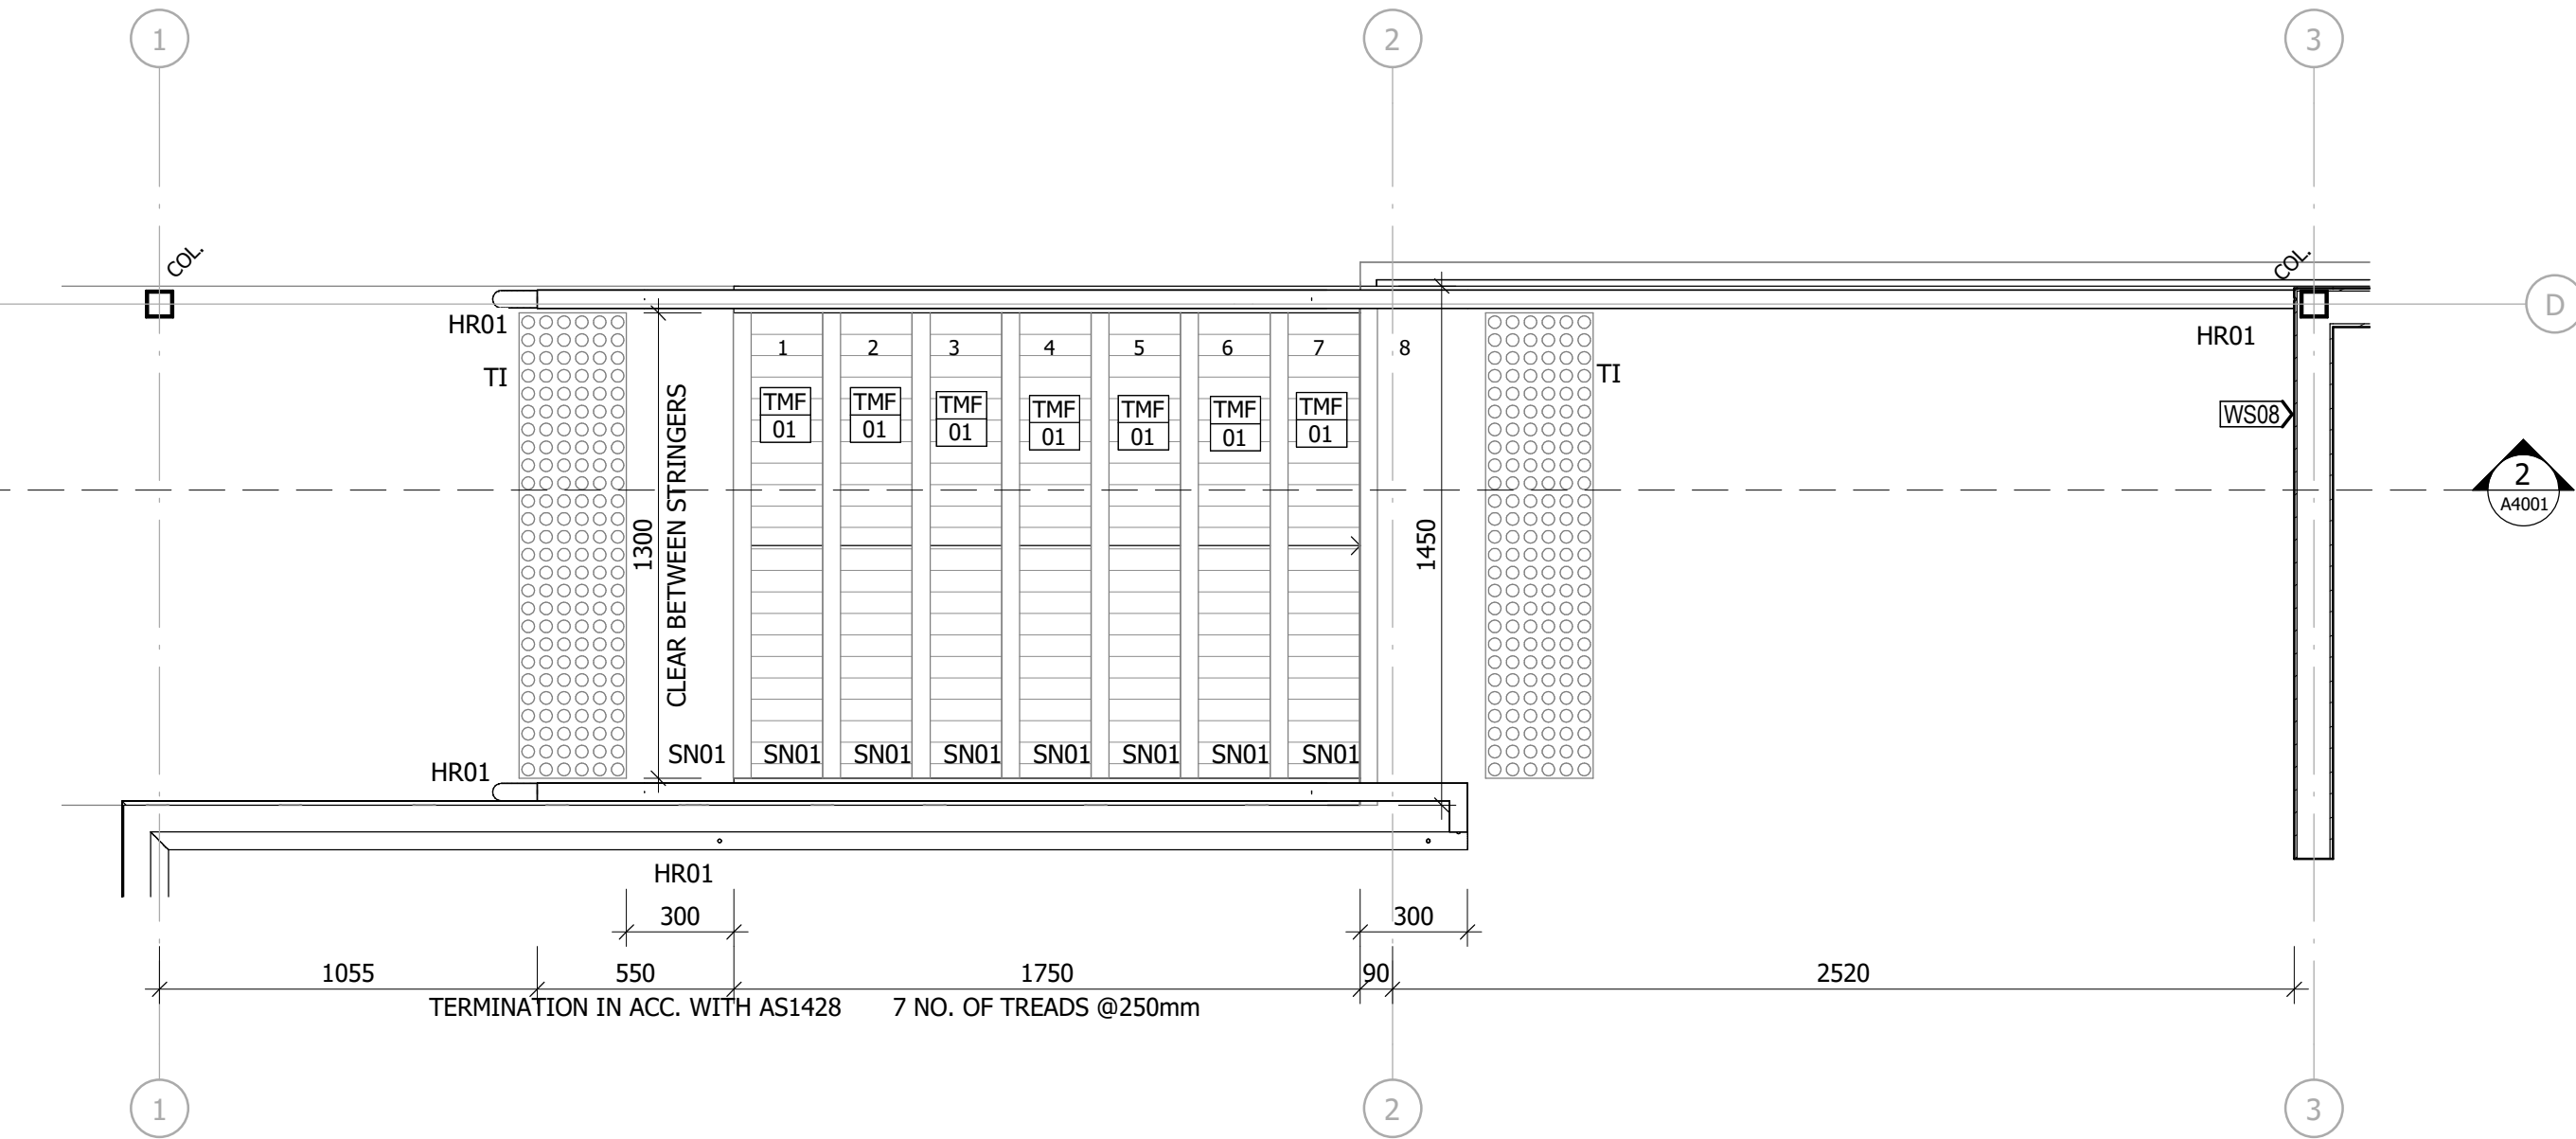


1 STAIR 1 - PLAN
A2001/ 1 : 20

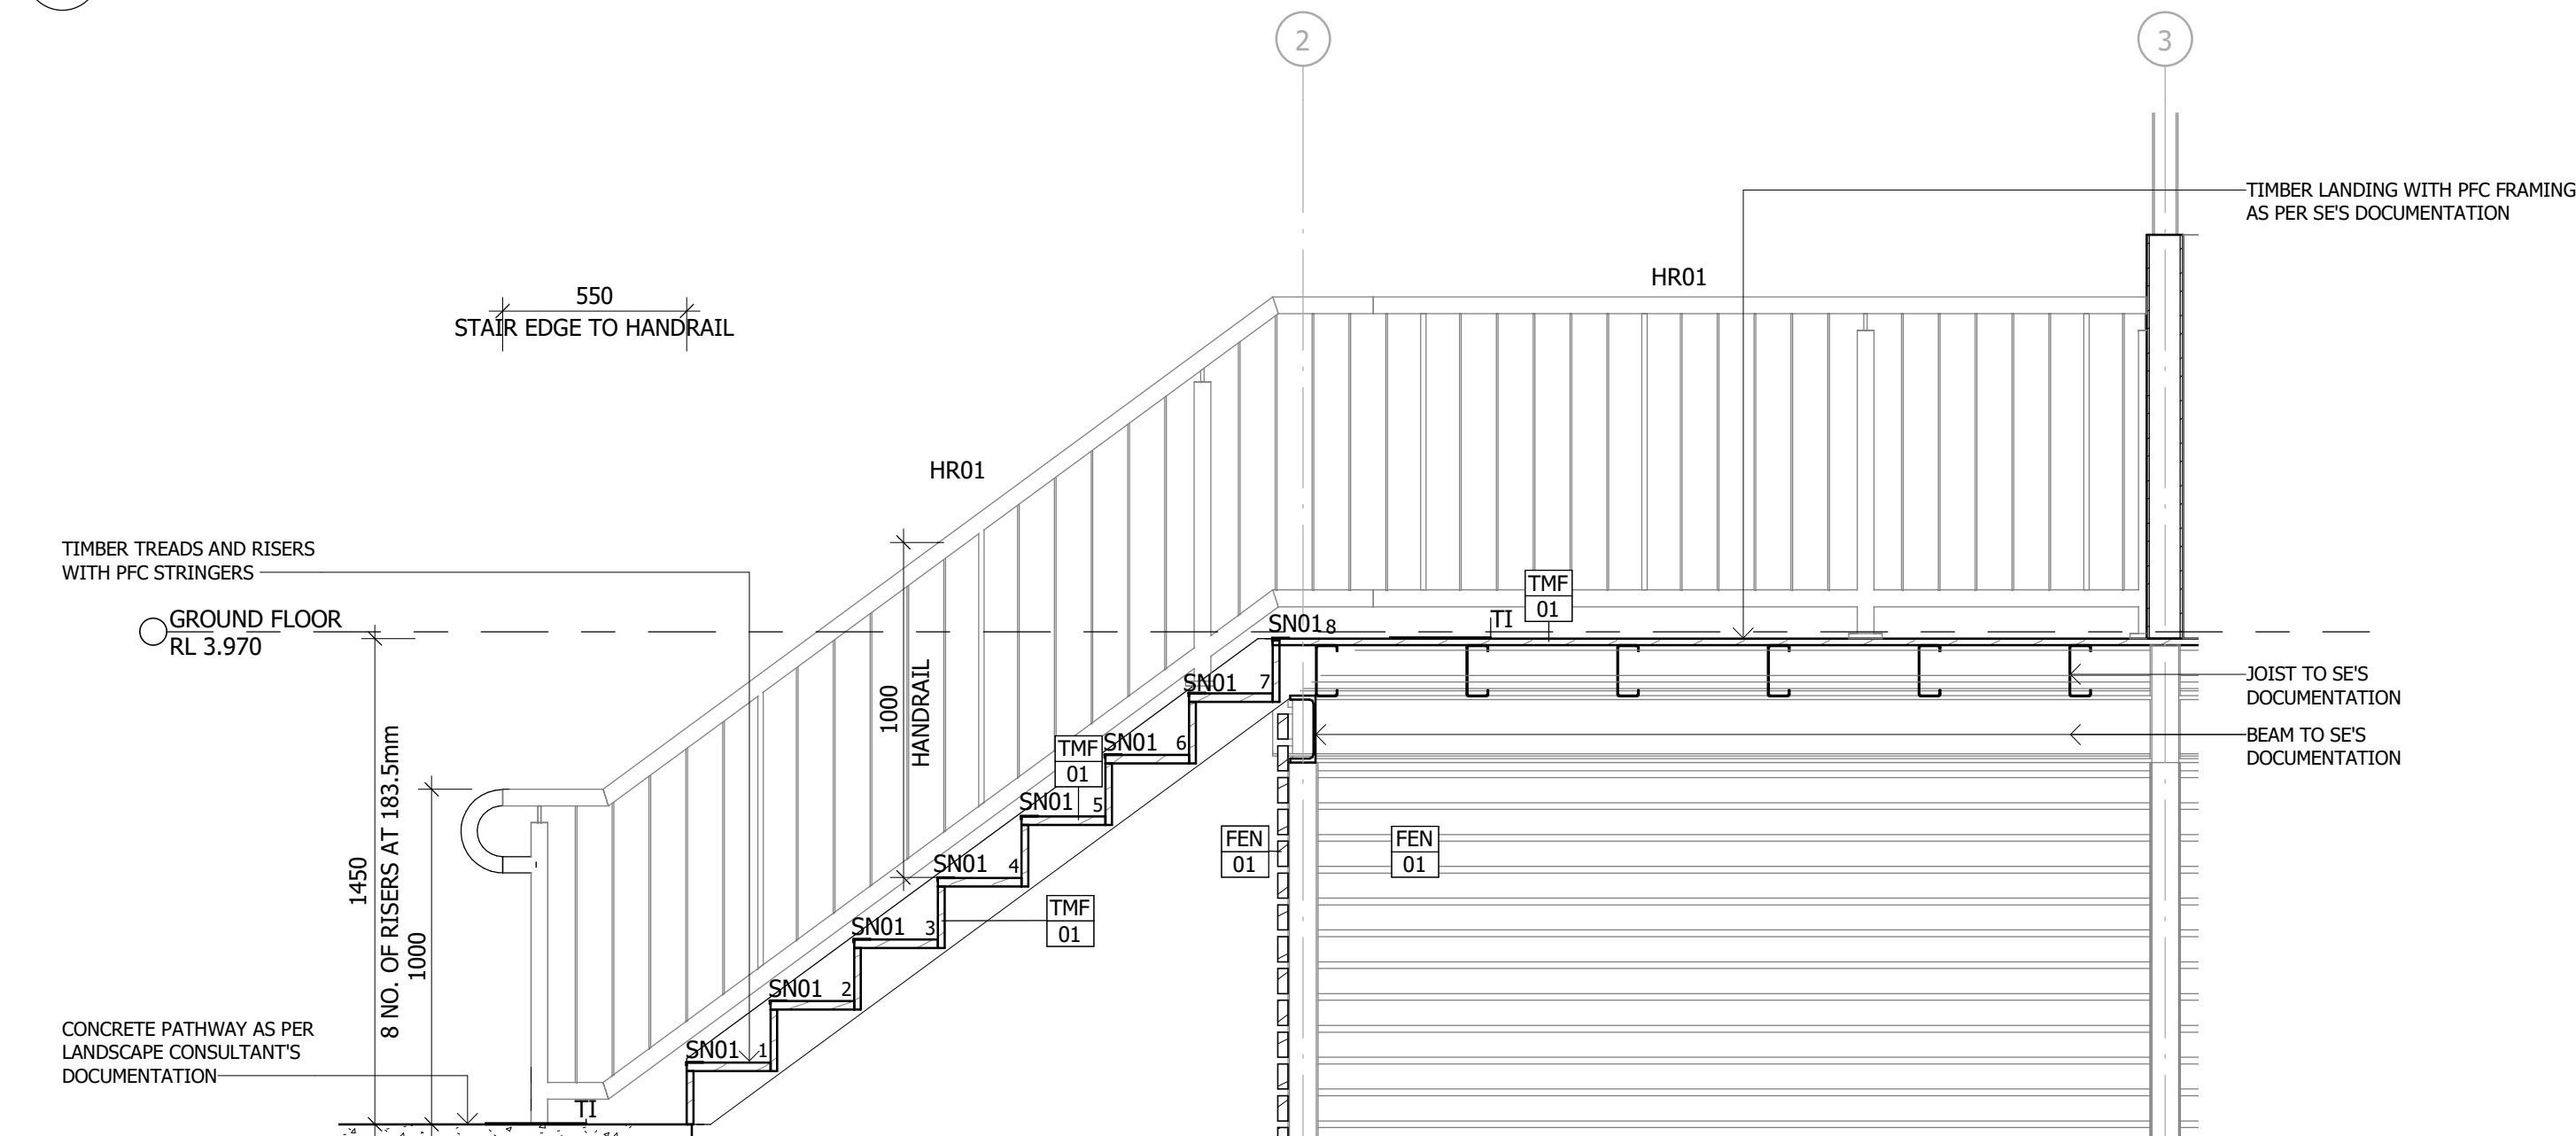


2 STAIR 1 - SECTION
A4001/ 1 : 20

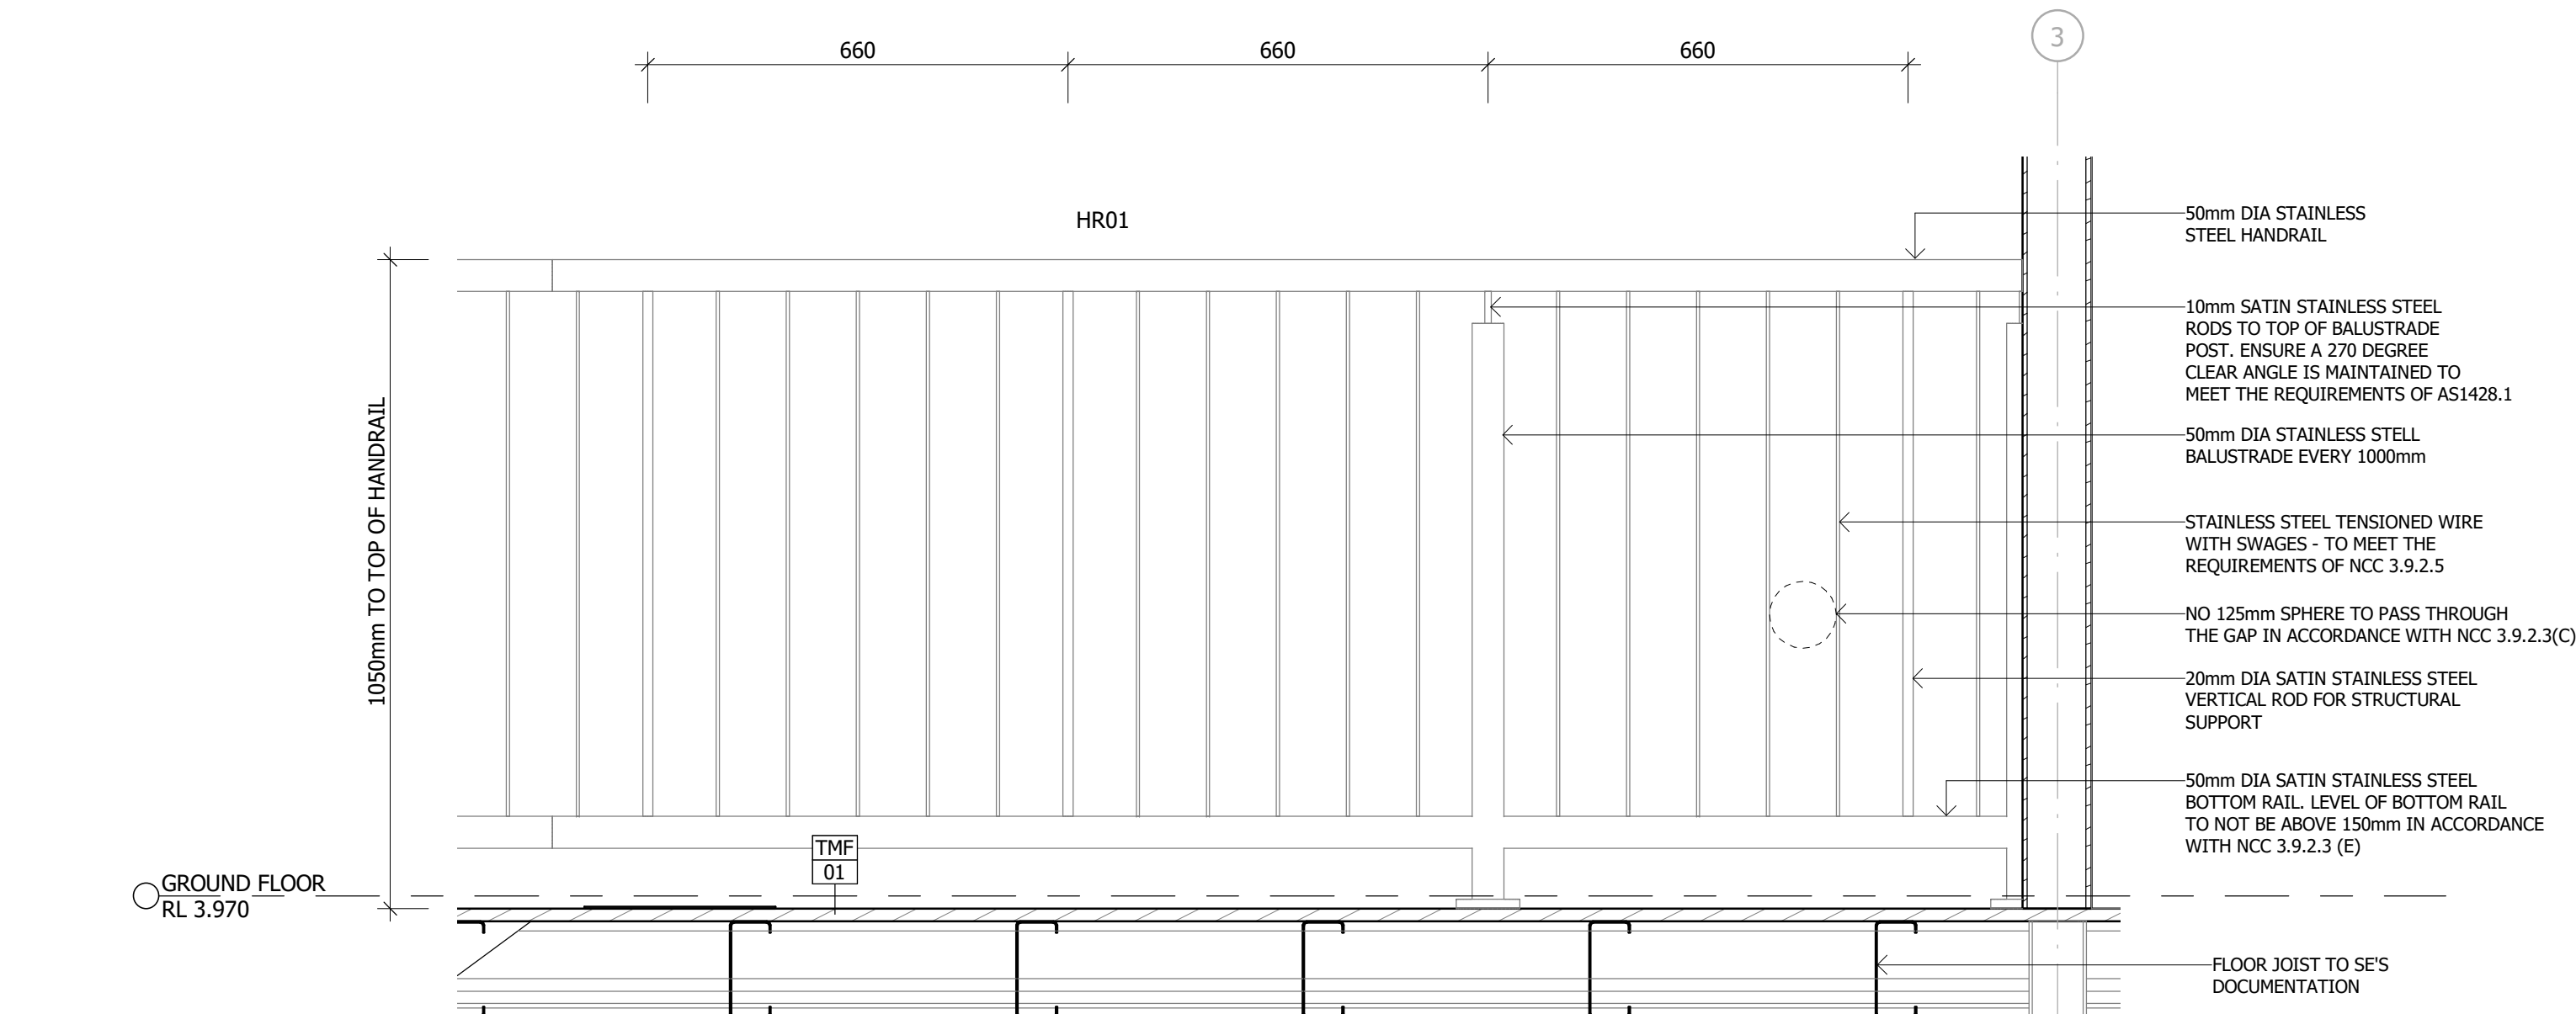


5 BALUSTRADE ELEVATION
1 : 10

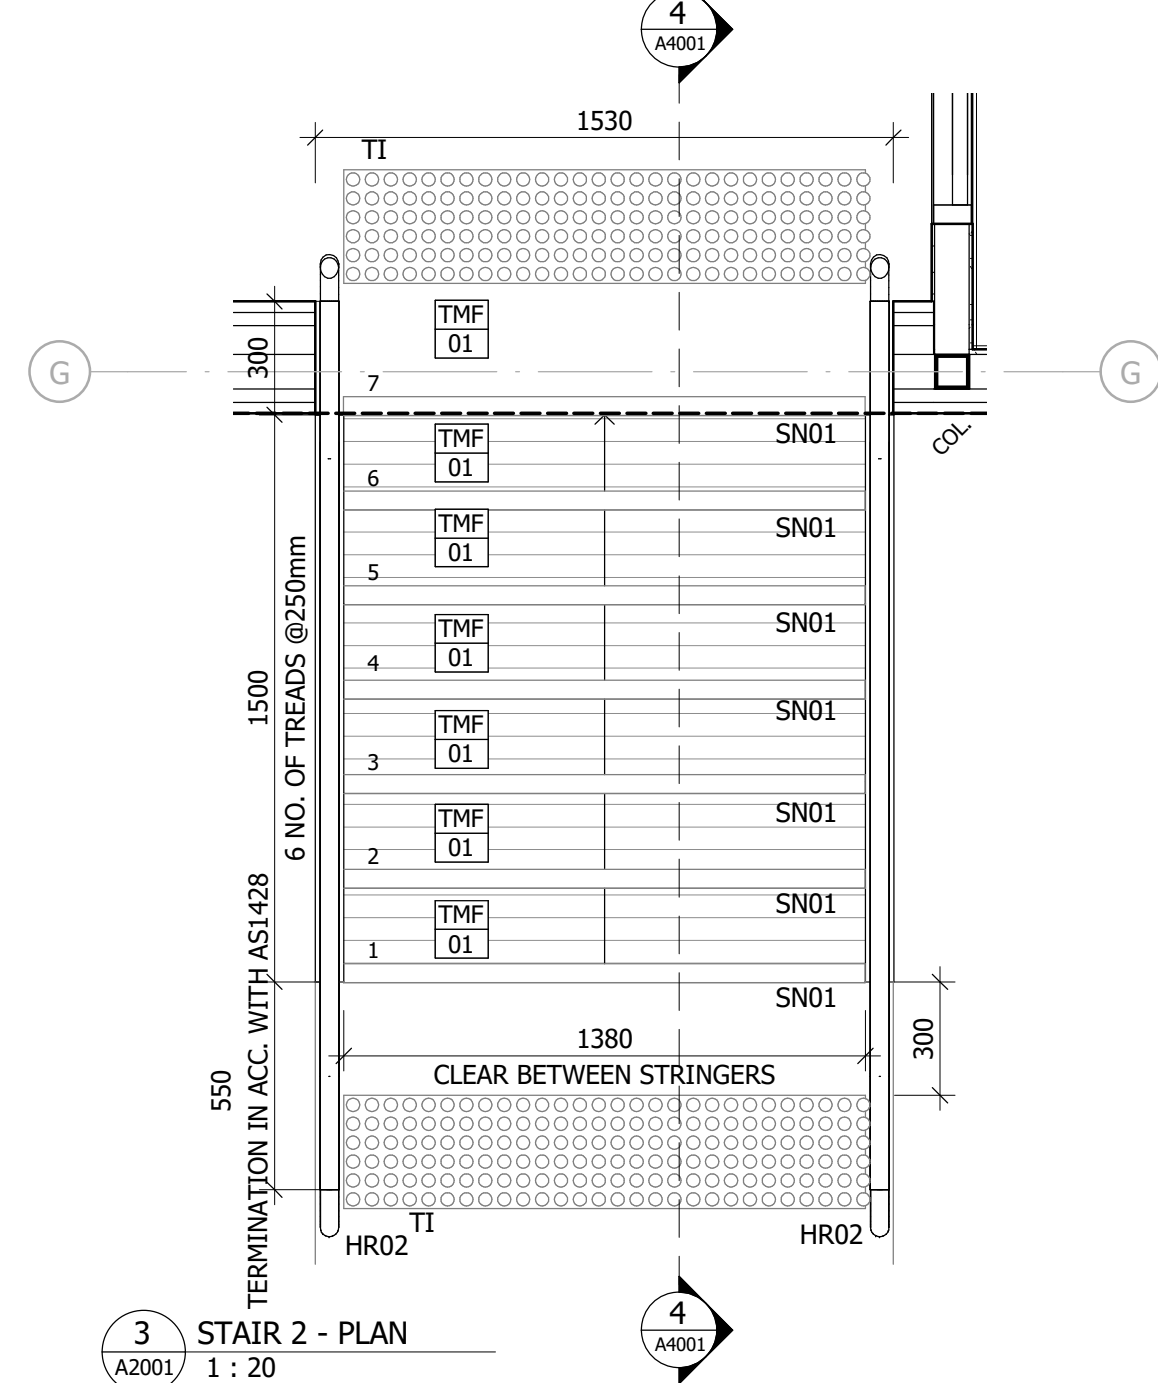

3 STAIR 2 - PLAN
A2001/ 1 : 20

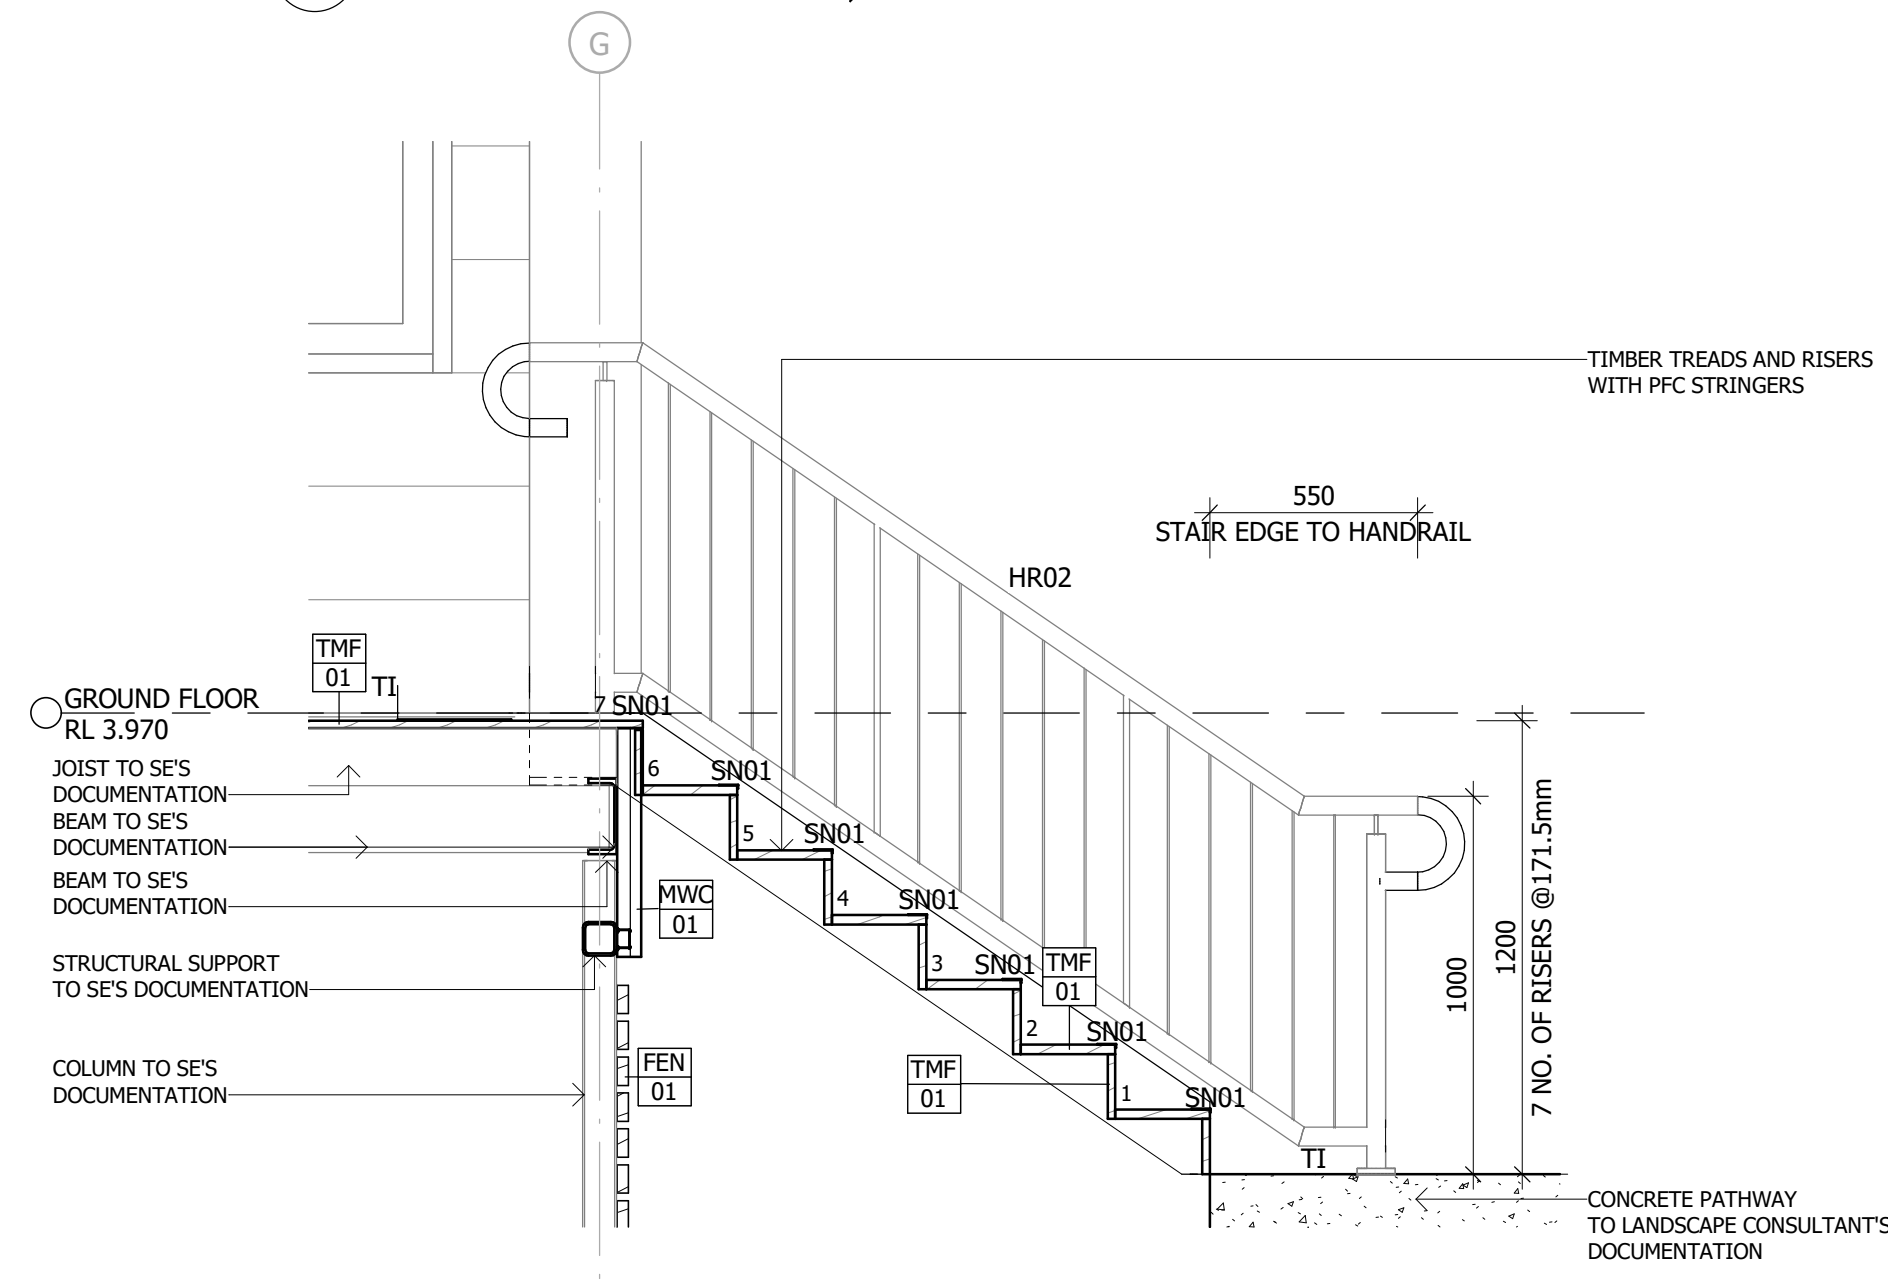

4 STAIR 2 - SECTION
A4001/ 1 : 20

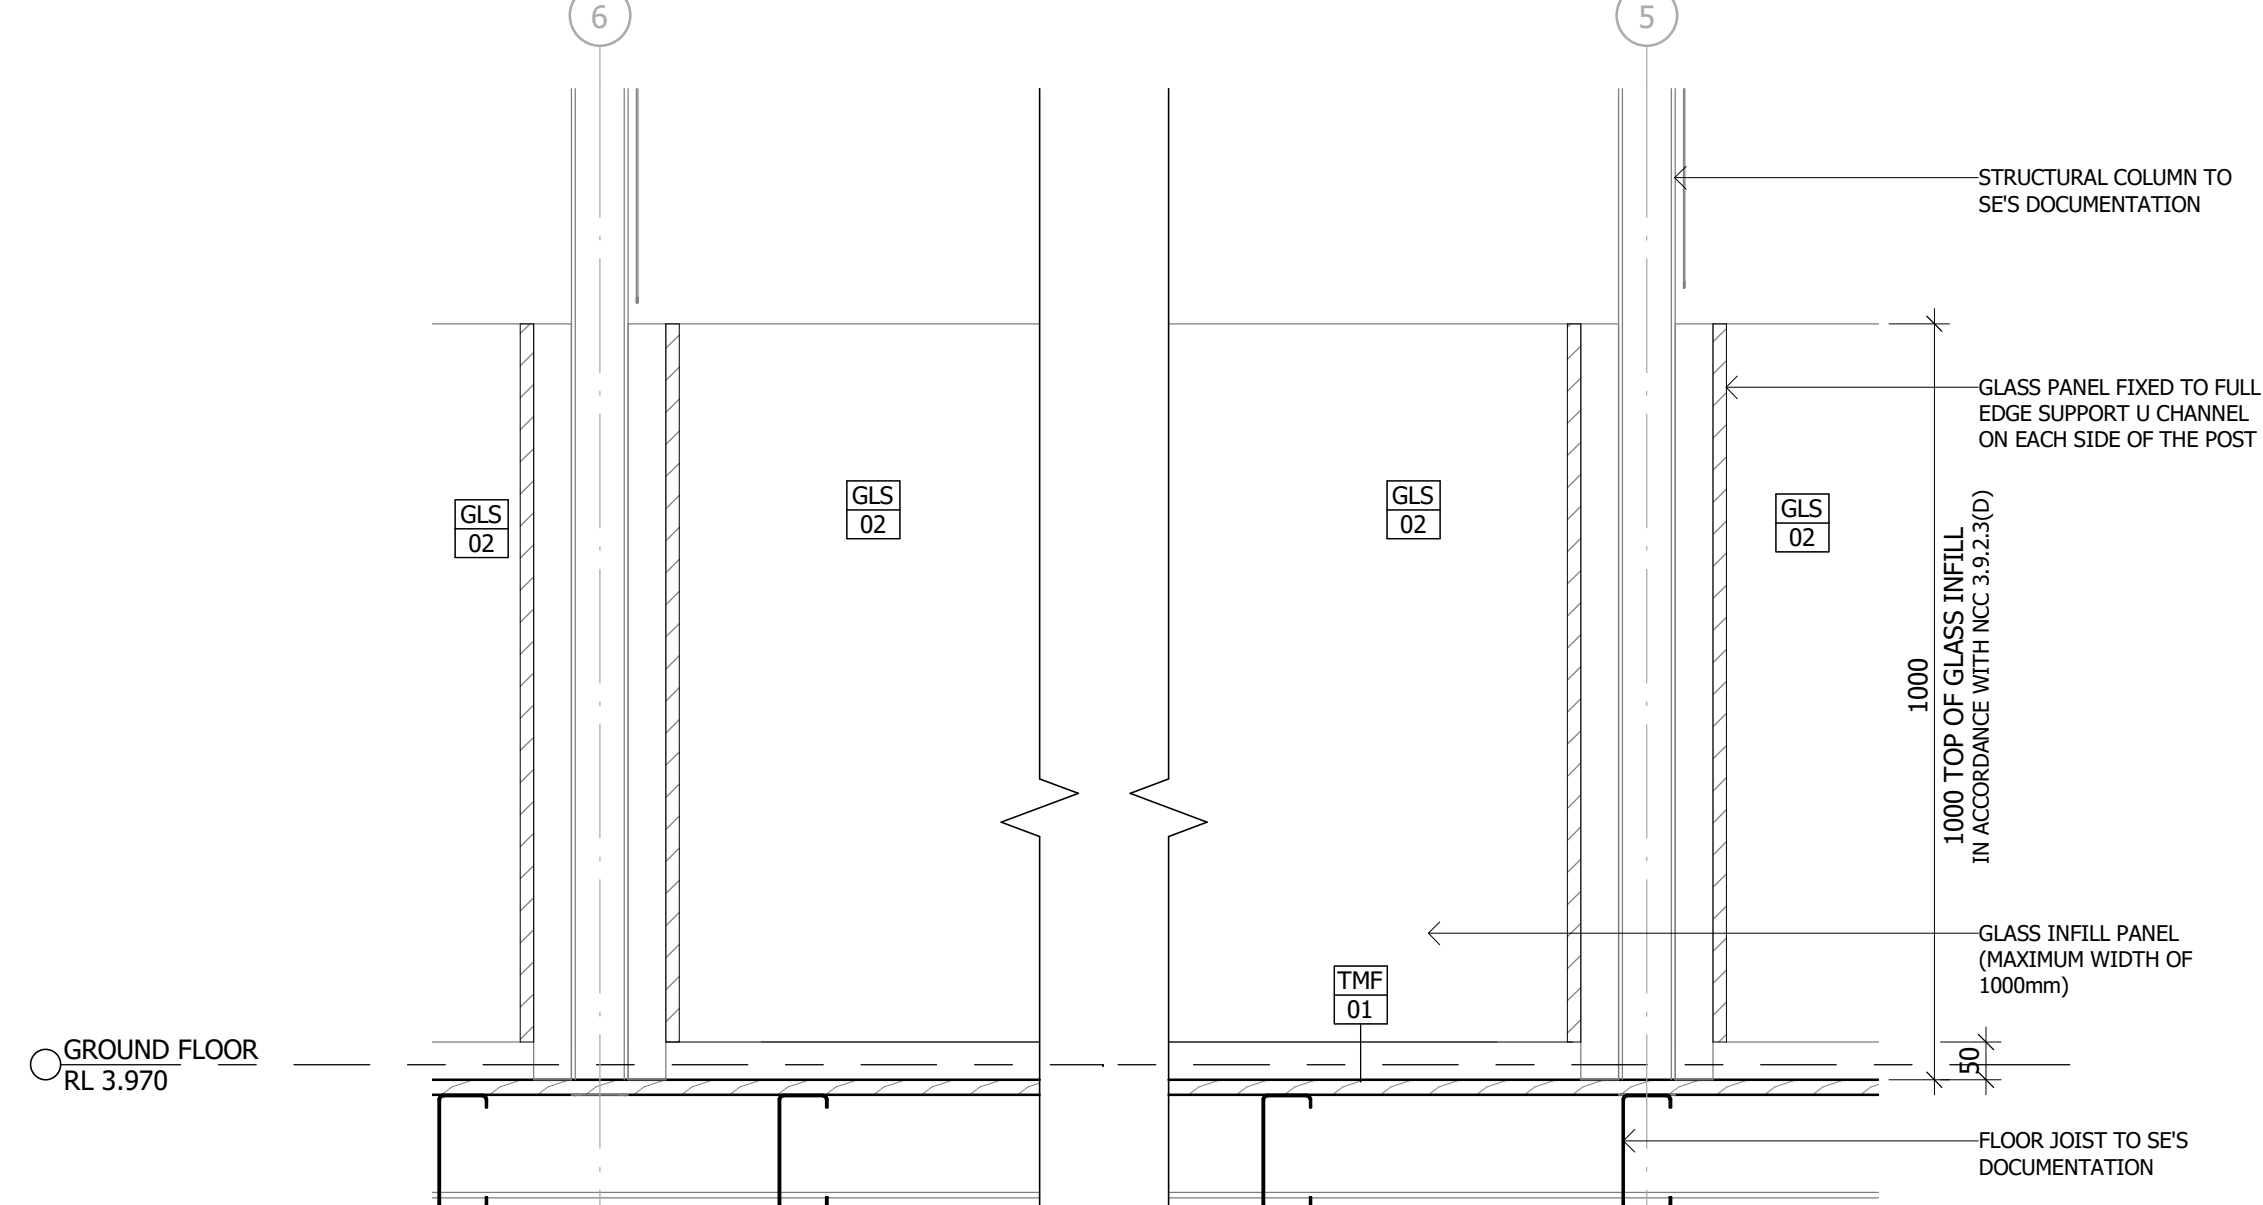

6 HR03 - ELEVATION
1 : 10

Notes

The information contained in this document is copyright and may not be used or reproduced for any other project or purpose.

Verify all dimensions and levels on site and report any discrepancies to dwp for direction prior to the commencement of work.

Drawings are to be read in conjunction with all other contract documents.

Use figured dimensions only. Do not scale from drawings. dwp cannot guarantee the accuracy of content and format for copies of drawings issued electronically. The completion of the Issue Details Checked and Authorised section is confirmation of the status of the drawing. The drawing shall not be used for construction unless endorsed 'For Construction' and authorised for issue.

© dwp Australia Pty Ltd
Registered Business Name dwp Australia ABN 37 169 328 018
Nominated Architect Angus Rose NSW ARB 8341 &
Nominated Architect Cameron Martin NSW ARB 9194
© Copyright 2011 dwp.
ALL RIGHTS RESERVED.
Reproduction prohibited unless authorised in writing by dwp.

FOR TENDER IN
NOT TO BE USED DURING CONSTRUCTION

A	TENDER ISSUE	22.12.2021	FK	DB
Issue	Description	Date	Chk	Auth
Architect/ Designer	dwp			
	www.dwp.com			
Client	Bolton Clarke			

Project
Galleon Gardens Club House

Location
126-134 Galleon Way
Currumbin Waters, QLD

Project Number
21-0511

Drawing
STAIR DETAILS

Scale (A1) Date Printed
As indicated 22/12/2021 6:08:35 PM

Drawing Number Issue
A4001 A



File Name: BHP_360/21-0511_Galleon Gardens Club House/21-0511-A4001.dwg