


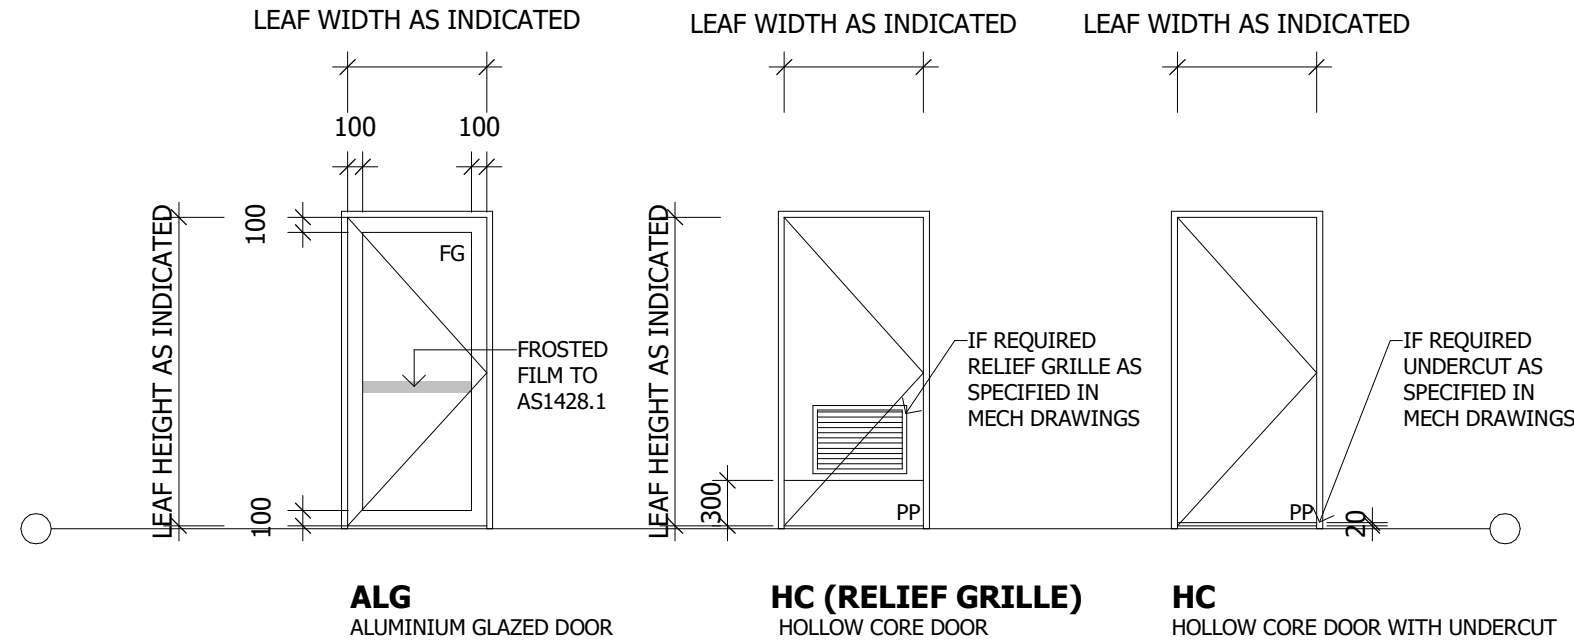

1 DOOR TYPE ELEVATIONS
1 : 50

DOOR SCHEDULE																															
DOOR ID			DOOR OPERATION	FRAME		LEAF						GLASS		HARDWARE							COMMENTS	REVISION									
DOOR No. WITHIN ROOM	ROOM NO	ROOM NAME		TYPE	FINISH	TYPE	FINISH	No. OFF	THICKNESS	LEAF HEIGHT	LEAF A WIDTH	LEAF B WIDTH	TYPE	FILM	DOOR SEALS	SECURITY / ELEC.	KEYING	LOCK / LATCH	HANDLES				HINGES	DOOR CLOSER	DOOR STOP	OTHER HARDWARE					
																			IN	OUT											

GROUND FLOOR																																	
D01	GF01	RECREATION ROOM	BIFOLD	APGS	APGS			6	40	2035	972	0		FLM01	WS	-	GMK	PL	LE	LE	MSP											PROVIDE CONDUITS FOR FUTURE SWIPE CARDS. BOTTOM TRACK TO BE DDA COMPLIANT	
D02	GF01	RECREATION ROOM	SLIDING_STACKED	APGS	APGS			2	40	2035	1233	0		FLM01	WS	-	GMK	PL	LE	LE	MSP											PROVIDE CONDUITS FOR FUTURE SWIPE CARDS. BOTTOM TRACK TO BE DDA COMPLIANT	
D01	GF02	STORE	SWING	AL	CA	HC	PT05	1	40	2040	820	0	-	-	-		GMK	SL	LE	LE	BB		WMDS									DOOR STOP MOVED TO THE KICKBOARD OF KITCHEN	
D02	GF02	STORE	SWING	AL	CA	HC	PT05	2	40	2040	620	620	-	-	-		GMK	SL	LE	LE	BB		WMDS										
D01	GF03	OFFICE	SWING	APGS	APGS			1	40	2035	920			FLM01	WS	-	KD	CL	LE	LE	BB	DA	FMDS									PROVIDE CONDUITS FOR FUTURE SWIPE CARDS. BOTTOM TRACK TO BE DDA COMPLIANT	
D01	GF04	ACCESSIBLE TOILET	SWING	AL	PT04	HC	PT04	1	40	2040	920		-	-	AS/W S	-	-	PR,IB	LE	LE	LO	DA	WMDS	-								RELIEF GRILLE TO MATCH MECH. SPECIFICATIONS	
D01	GF05	AMBULANT TOILET	SWING	AL	PT04	HC	PT04	1	40	2040	920			AS/W S	-	-	PR,IB	LE	LE	LO		WMDS										20mm UNDERCUT OR AS SPECIFIED BY MECH. CONSULTANT	
D01	GF06	VERANDAH RAILING (HR03)	SWING	APGS	APGS	HR03	HR03	1	40	950	920	0	-	-	WS			PL	LE	LE	BB		FMDS										
D02	GF06	VERANDAH RAILING (HR03)	SWING	APGS	APGS	HR03	HR03	1	40	950	920	0	-	-	WS			PL	LE	LE	BB		FMDS										
D01	GF07	UNDERCROFT FENCE	GATE	FEN01	FEN01	FEN01	FEN01	2	75	1425	1300	1300	-	-	WS		GMK	SL	LE	LE	BB												
D01	GF08	DB CUPBOARD	SWING	JRY	PT04	JRY	PT04	1	20	2085	680	-	-	-	WS		GMK																

DOOR LEGEND

REFER TO FINISHES SCHEDULE FOR DEFINITIONS OF FINISHES CODES

FRAME TYPE

APGS AS PER GLAZING SYSTEM
JRY JOINERY
FEN01 TO MATCH SPECIFICATIONS OF FEN01
HR03 TO MATCH SPECIFICATIONS OF HR03

FRAME FINISH

APGS AS PER GLAZING SYSTEM
CA CLEAR ANODISED
PT PAINT FINISH
ST STEEL FRAME
MSP MANUFACTURER'S SPECIFICATION
PC## POWDER COAT TYPE ##, REFER TO SCHEDULE
JRY JOINERY
FEN01 TO MATCH SPECIFICATIONS OF FEN01
HR03 TO MATCH SPECIFICATIONS OF HR03

DOOR LEAF TYPE

HC HOLLOW CORE
SC SOLID CORE
ALG ALUMINIUM FRAMED GLASS
FEN01 TO MATCH SPECIFICATIONS OF FEN01
BFD01 AS SPECIFIED UNDER BFD01 IN THE MISC. ITEMS SCHEDULE
JRY JOINERY
HR03 TO MATCH SPECIFICATIONS OF HR03

DOOR LEAF FINISH

CA CLEAR ANODISED
PT PAINT FINISH
EXG AS EXTERNAL GLAZING SYSTEM
JRY JOINERY
FEN01 TO MATCH SPECIFICATIONS OF FEN01
HR03 TO MATCH SPECIFICATIONS OF HR03

GLASS TYPE

GLS01 6mm CLEAR TOUGHENED GLASS

APPLIED FINISH/ASSOCIATED ITEMS

FLM01 FROSTED GLASS FILM
RPLB01 RECESSED PELMET BLINDS TO INSIDE (SINGLE ROLL)

GRILLE TYPE

RG01 AS SPECIFIED BY THE MECHANICAL CONSULTANT

LOCK/SECURITY / ELECTRONIC

EMG ELECTROMAGNETIC LOCK
GMK GRAND MASTER KEY SYSTEM
KD KEYED DIFFERENTLY
IB INDICATOR BOLT
PR PRIVACY SET

LOCK / LATCH

CL CLASSROOM LOCK - EXTERNAL UNLOCK.
INTERNAL SNIB LOCK
PL PASSAGE LATCH
SL STOREROOM LOCK - KEY OPEN & LOCK

HANDLES

LE LEVER HANDLE

HINGES

BB BARREL BOLT
LO LIFT OFF HINGES
MSP MANUFACTURER'S SPECIFICATIONS

DOOR SEALS

AS ACOUSTIC SEAL
WS WEATHERPROOF SEAL

DOOR CLOSER

DA DELAYED ACTION CLOSER [AS1428.1]
FMDS FLOOR MOUNTED DOOR STOP
WMDS WALL MOUNTED DOOR STOP

DOOR STOP

FMDS FLOOR MOUNTED DOOR STOP
WMDS WALL MOUNTED DOOR STOP

OTHER

RBK ALUMINIUM REBATE KIT

Notes

The information contained in this document is copyright and may not be used or reproduced for any other project or purpose.

Verify all dimensions and levels on site and report any discrepancies to dwp for direction prior to the commencement of work.

Drawings are to be read in conjunction with all other contract documents.

Use figured dimensions only. Do not scale from drawings. dwp cannot guarantee the accuracy of content and format for copies of drawings issued electronically. The completion of the Issue Details Checked and Authorised section is confirmation of the status of the drawing. The drawing shall not be used for construction unless endorsed 'For Construction' and authorised for issue.

© Copyright 2011 dwp.
ALL RIGHTS RESERVED.
Reproduction prohibited unless authorised in writing by dwp.

NOTES:

1. DOOR LEAF SIZES SPECIFIED IN THE SCHEDULE ARE EXCLUSIVE OF FRAMES, LININGS AND INSTALLATION TOLERANCES.
2. ALL DOOR OPENING SIZES SHOULD BE CHECKED ON SITE FOR TRUE DIMENSIONS.
3. HEIGHTS AND SPECIFICATIONS MAY VARY IN DIFFERENT AREAS, PARTICULARLY WHERE RAISED ACCESS FLOORS ARE INSTALLED.
4. REFER TO PLANS FOR DOOR SWINGS.
5. FRAME DEPTH VARIES TO SUIT FINISHED WALL THICKNESS UNLESS NOTED OTHERWISE.
6. EXTERNAL PROTECTION PLATES ARE LOCATED ON THE SIDE THE DOOR SWINGS INTO WHILE INTERNAL PROTECTION PLATES ARE LOCATED ON THE SIDE THE DOOR SWINGS AWAY FROM.
7. OUTSIDE (OUT) OF DOOR IS:
-ENTRANCE FACE (EXTERNAL DOOR)
-CORRIDOR FACE (ROOM DOOR)
-ROOM FACE (CUPBOARD DOOR)
-THE SIDE THE HINGES ARE NOT SEEN (DOOR JOINING TWO ROOMS)
8. ALL HINGES TO BE HIGH QUALITY STAINLESS STEEL UNLESS NOTED OTHERWISE.
9. DOOR SETOUT AS DRAWN. SET OUT FRAMES TO SUIT THE CLEARANCES REQUIRED BY THE BCA AND AS1428.1 & ADJACENT SPACE TO THE CLEAR OPENINGS.
10. ALL LEAF SIZES ARE OVERALL AND THE CONTRACTOR SHOULD REDUCE LEAF SIZE TO SUIT UNDERCUTS OR OVERCUTS AS REQUIRED.

FOR TENDER

NOT TO BE USED DURING CONSTRUCTION

A	TENDER ISSUE	23.12.2021	FK	DB
Issue	Description	Date	Chk	Auth

Architect/ Designer

dwp

www.dwp.com

Client

Bolton Clarke

Project

Galleon Gardens Club House

Location

126-134 Galleon Way
Currumbin Waters, QLD

Project Number

21-0511

Drawing Session

DRAWING SESSION

Drawing

DOOR SCHEDULE

SHEET NAME (LOCAL LANGUAGE)

Scale (A1)

1 : 50

Drawing Number

A6001

Date Printed

23/12/2021 11:03:16 AM

Issue

A

